

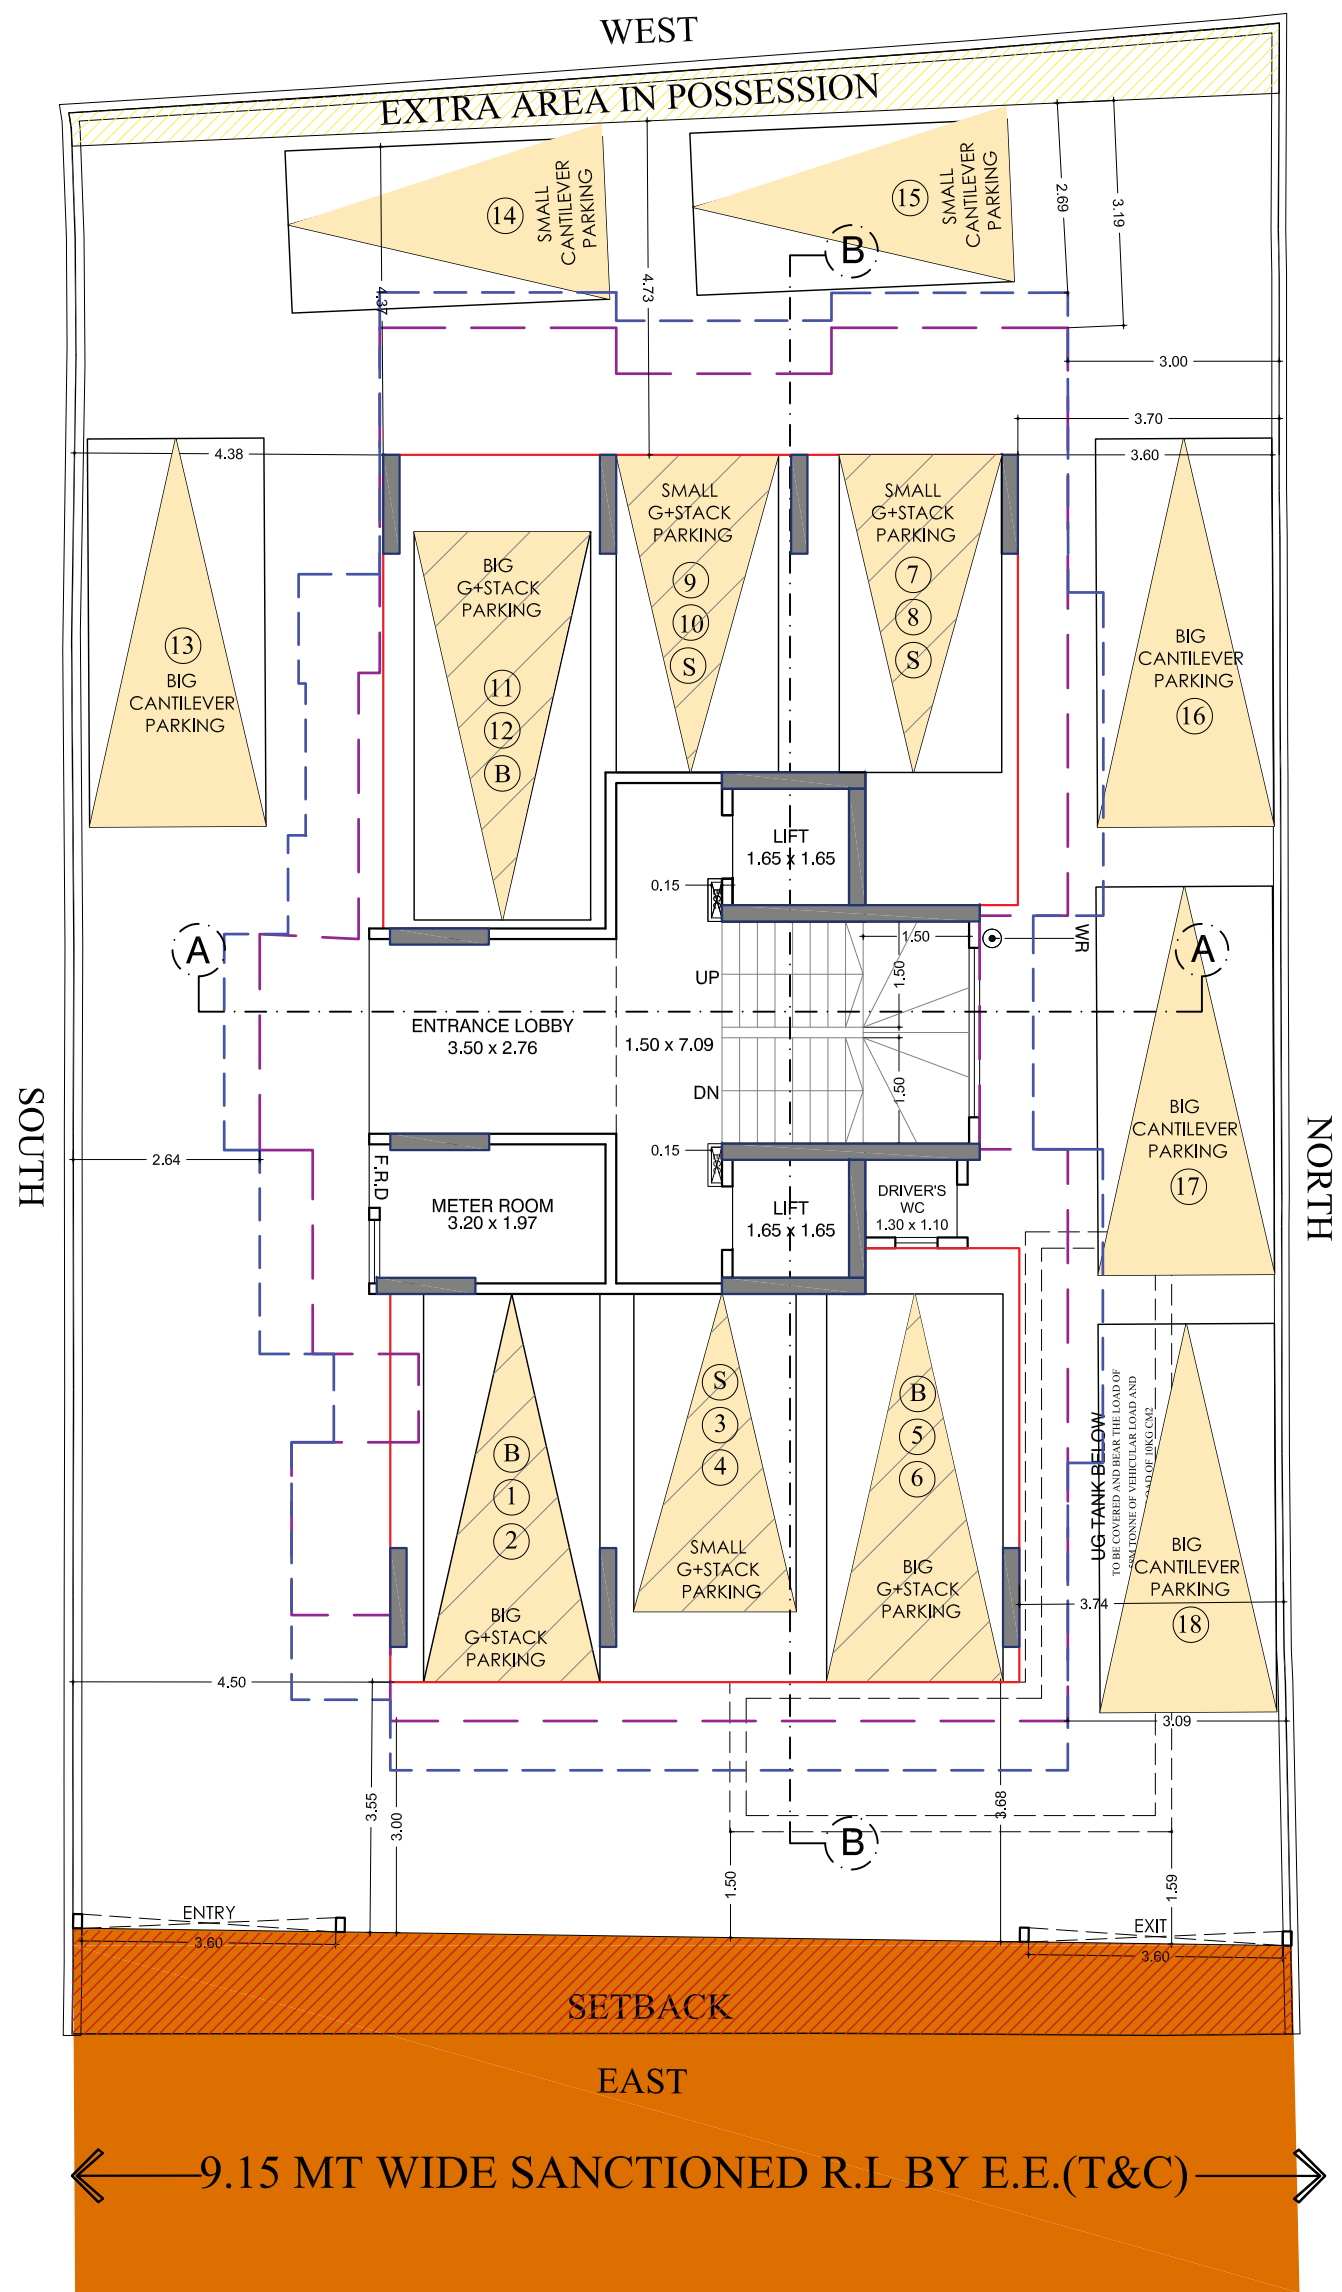



TABLE NO - I								
PROPOSED BUILT UP AREA STATEMENT								
Sr. No.	Wing	Floor No.	Proposed Built up Area (in sq.mt.)		Total (4 + 5) (in sqmt)	Staircase/ lift/ lift lobby area (in sq.mt.)		Flat/NR/Society Office/ Fitness Centre/Refuge area
			Commercial	Residential		Commercial	Residential	
(1)	(2)	(3)	(4)	(5)	(6)	(7)	(8)	(9)
1	A	GR	0.00		0.00			
		1ST FLOOR		147.3	147.30		30.6	FLAT
		2nd FLOOR		147.3	147.30		25.15	FLAT
		3rd FLOOR		147.3	147.30		25.15	FLAT
		4th FLOOR		164.44	164.44		25.15	FLAT
		5th FLOOR		167.73	167.73		25.15	FLAT
		6th FLOOR		167.73	167.73		25.15	FLAT
		7th FLOOR		167.73	167.73		25.15	FLAT
		8th FLOOR		167.73	167.73		25.15	FLAT
		9th FLOOR		167.73	167.73		25.15	FLAT
2	Total BUA Proposed		0.00	1444.99	1444.99	0	231.80	
3	Net BUA Proposed (2 – 3)		0.00	1070.36	1070.36			
4	Fungible Compensatory Area Proposed:		0.00	374.63	374.63			
7	Fitness Centre	Permissible 2 X 2%	=					
8		Provided	=					
8	Society Office	Permissible	= 20 sqmt					
9		Provided						
9	Refuge Area	FLOOR	REQUIRED	PROPOSED	EXCESS	BUA AREA		
			4%	4.25%				

TABLE NO - IV											
PARKING SPACES STATEMENT											
Sr No.	Wing	Floor	Carpet Area of Tenement in sq.mt.			No of Tenements proposed per floor	No of Tenements in Group of Required Parking Spaces				Total Parking
			Flat No. 1	Flat No. 2	Flat No. 3		Below 45 sqm	Above 45 to 60 sqm	Above 60 to 90 sqm	Above 90	
WING A											
							(1 for 4 T/s)	(1 for 2 T/s)	(1 for every T/s)	(2 for 1 T/s)	
11	1	1st	54.03	30.56	45.34	3	1	2			0.00
(A) Residential:-											
		2nd	54.03	30.56	45.34	3	1	2			
		3rd	54.03	30.56	45.34	3	1	2			
		4th	54.03	30.56	42.64	3	2	1			
		5th	54.03	36.38	42.64	3	2	1			
		6th	54.03	36.38	42.64	3	2	1			
		7th	54.03	36.38	49.38	3	1	2			
		8th	54.03	36.38	49.38	3	1	2			
		9th	54.03	36.38	49.38	3	1	2			
2	Total Residential Tenements (For Tenement Density)					27	12	35			
3	Required Parking Spaces (From 2 Above)						3	75	0	0	10.5
4	10% Visitors parking (3 X 10%)										1.05
5	Total Required Parking Spaces for Residential Tenements (3 + 4)										11.55
6	Total Parking Spaces Permissible (Tenement wise & Shall not be more than Nos of T/s)										27
7	(B) Commercial:-										
8	Description		Parking Requirement				BUA in sq.mt.		No. of Parkings Required		
9	a) Mercantile (Market, departmental store, shops & other commercial uses)		i) 01 for every 40.00 sq.mt. Up to 800 sq.mt				ii) 01 for every 80 sq.mt exceeding 800 sq.mt		0	0.00	
10	b) Government or public or private office business building		i) 01 for every 37.50 sq.mt. Up to 1500 sq.mt				ii) 01 for every 75 sq.mt exceeding 1500 sq.mt		0	0.00	
11	c) Others		i)				ii)				
12	d) 10% Visitors (Min 2 Nos.)									0.00	
13	Total Required Parking Spaces for Commercial User										0.00
14	Total Parking Spaces Required for Res + Comm. = (5 + 13)										11.55
15	Maximum free permissible [No of Tenants having Carpet area less than 90.00 sqm + Parking spaces required for parking spaces Tenements having carpet area more than 90.00 sqm + Sr No 19] or [Sr No 14 + Sr No 19] whichever is more.										17.33
16	Total Parking Spaces provided										32
17	10% Additional Parking Spaces for Vehicle holding Area in case of mechanized parking										-
18	Excess to required Parking Spaces Provided= (16- 14)										0.00
19	50% of required Parking Spaces Permissible free of FSI/ without charging premium = 14 X 50%										5.78
DETAILS OF PARKING SPACES PROVIDED											
Sr No		Floor	Nos of Parking Spaces Provided				Total				
5			Small	Big		18					
		Total	8	10		18					
		% Ratio to Total	44.44%	55.56%		100%					

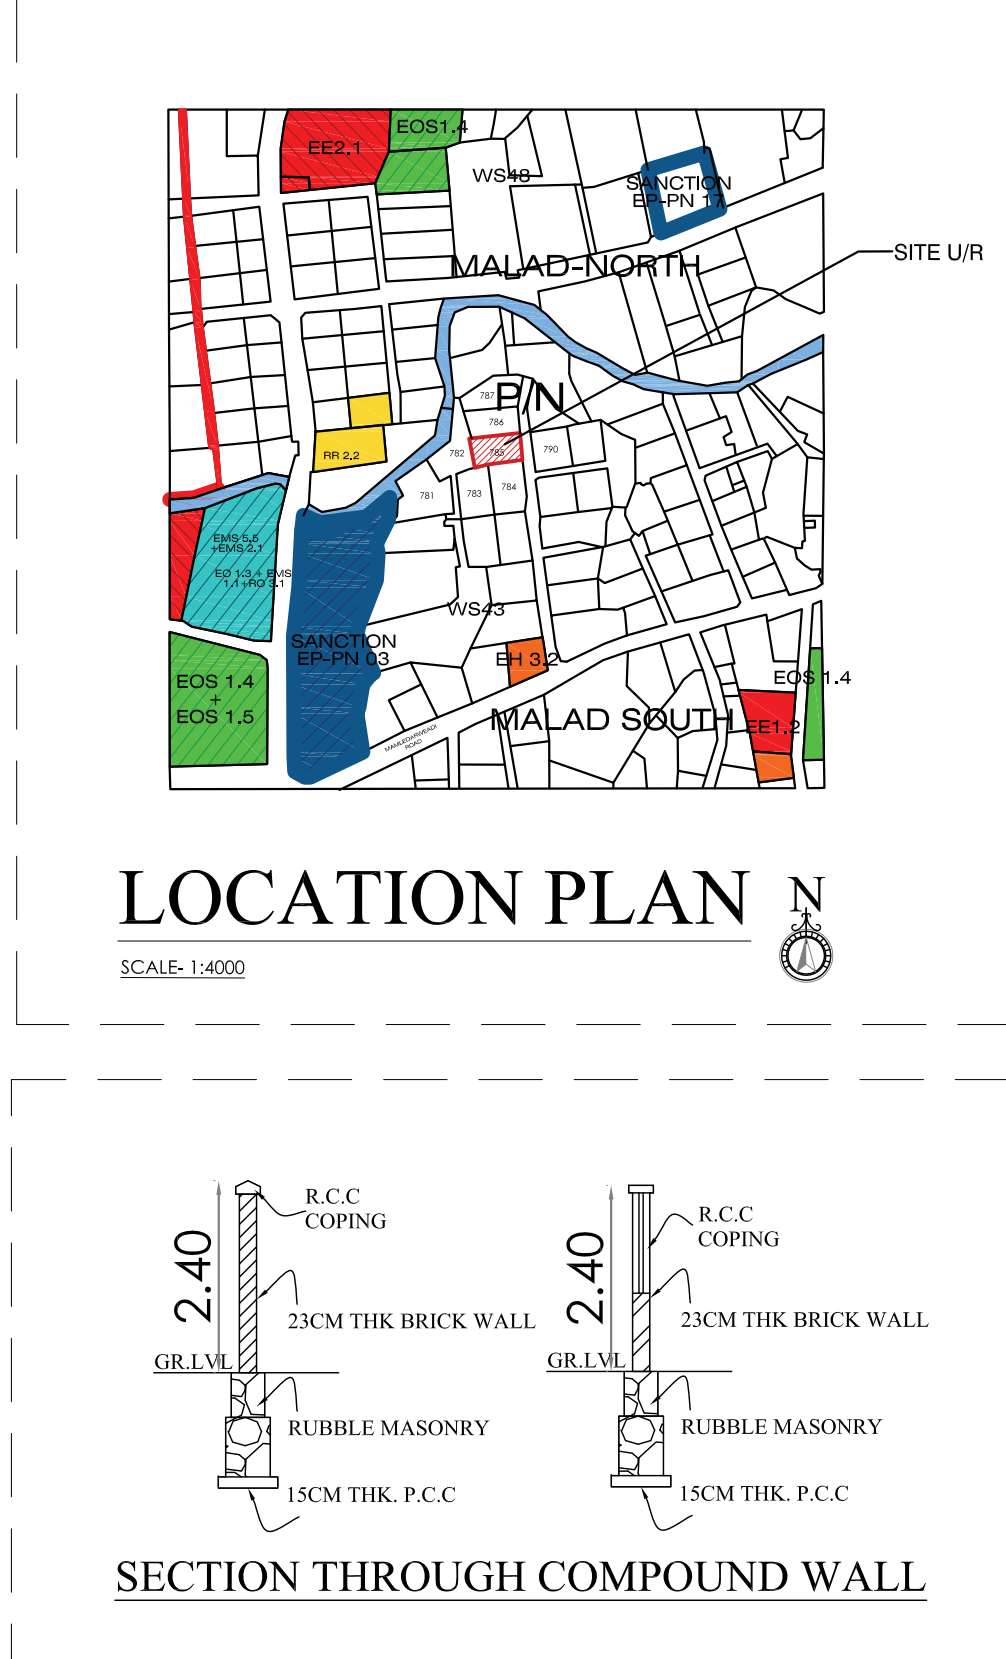


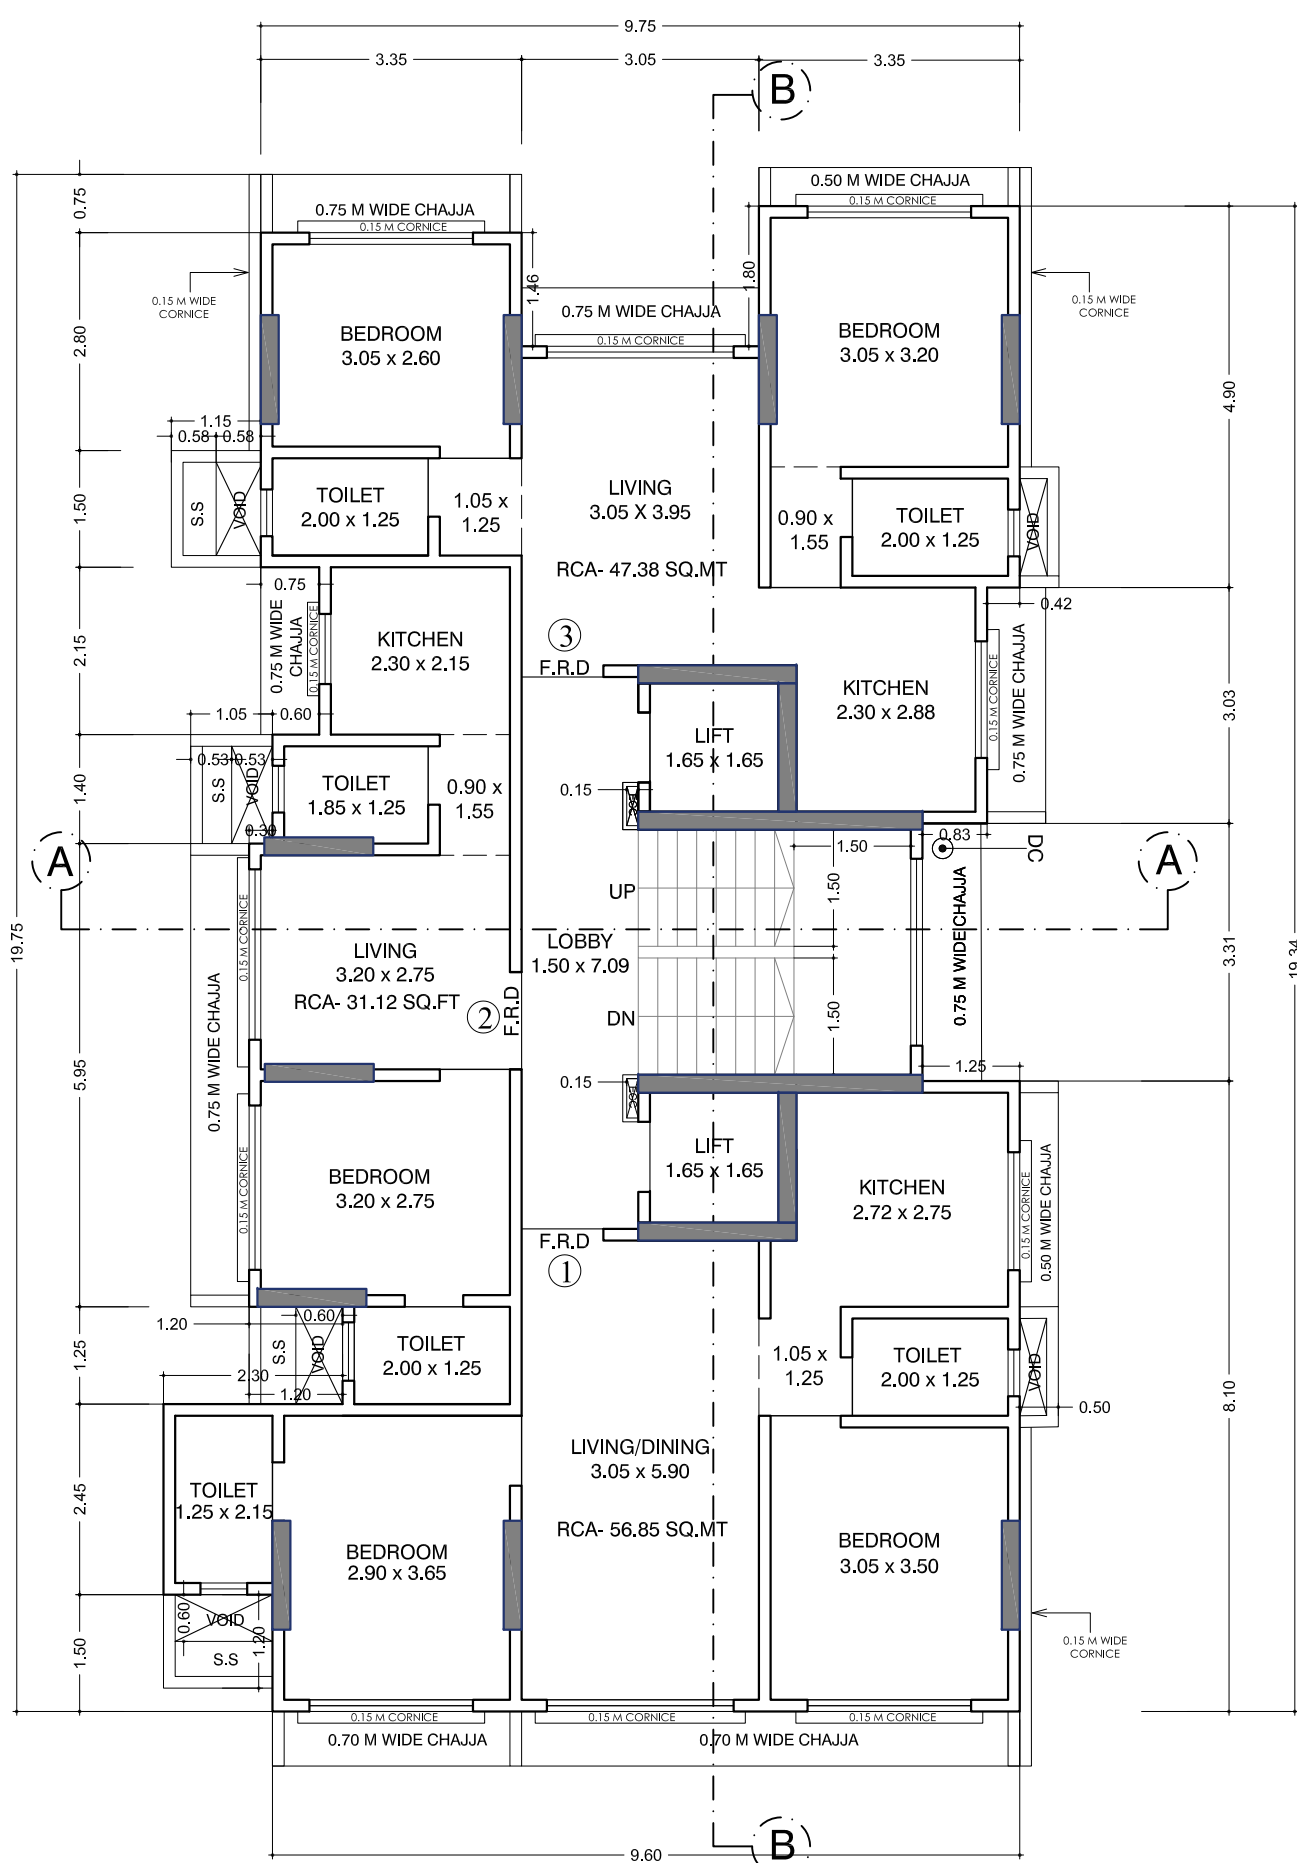


1ST - 3RD FLOOR PLAN

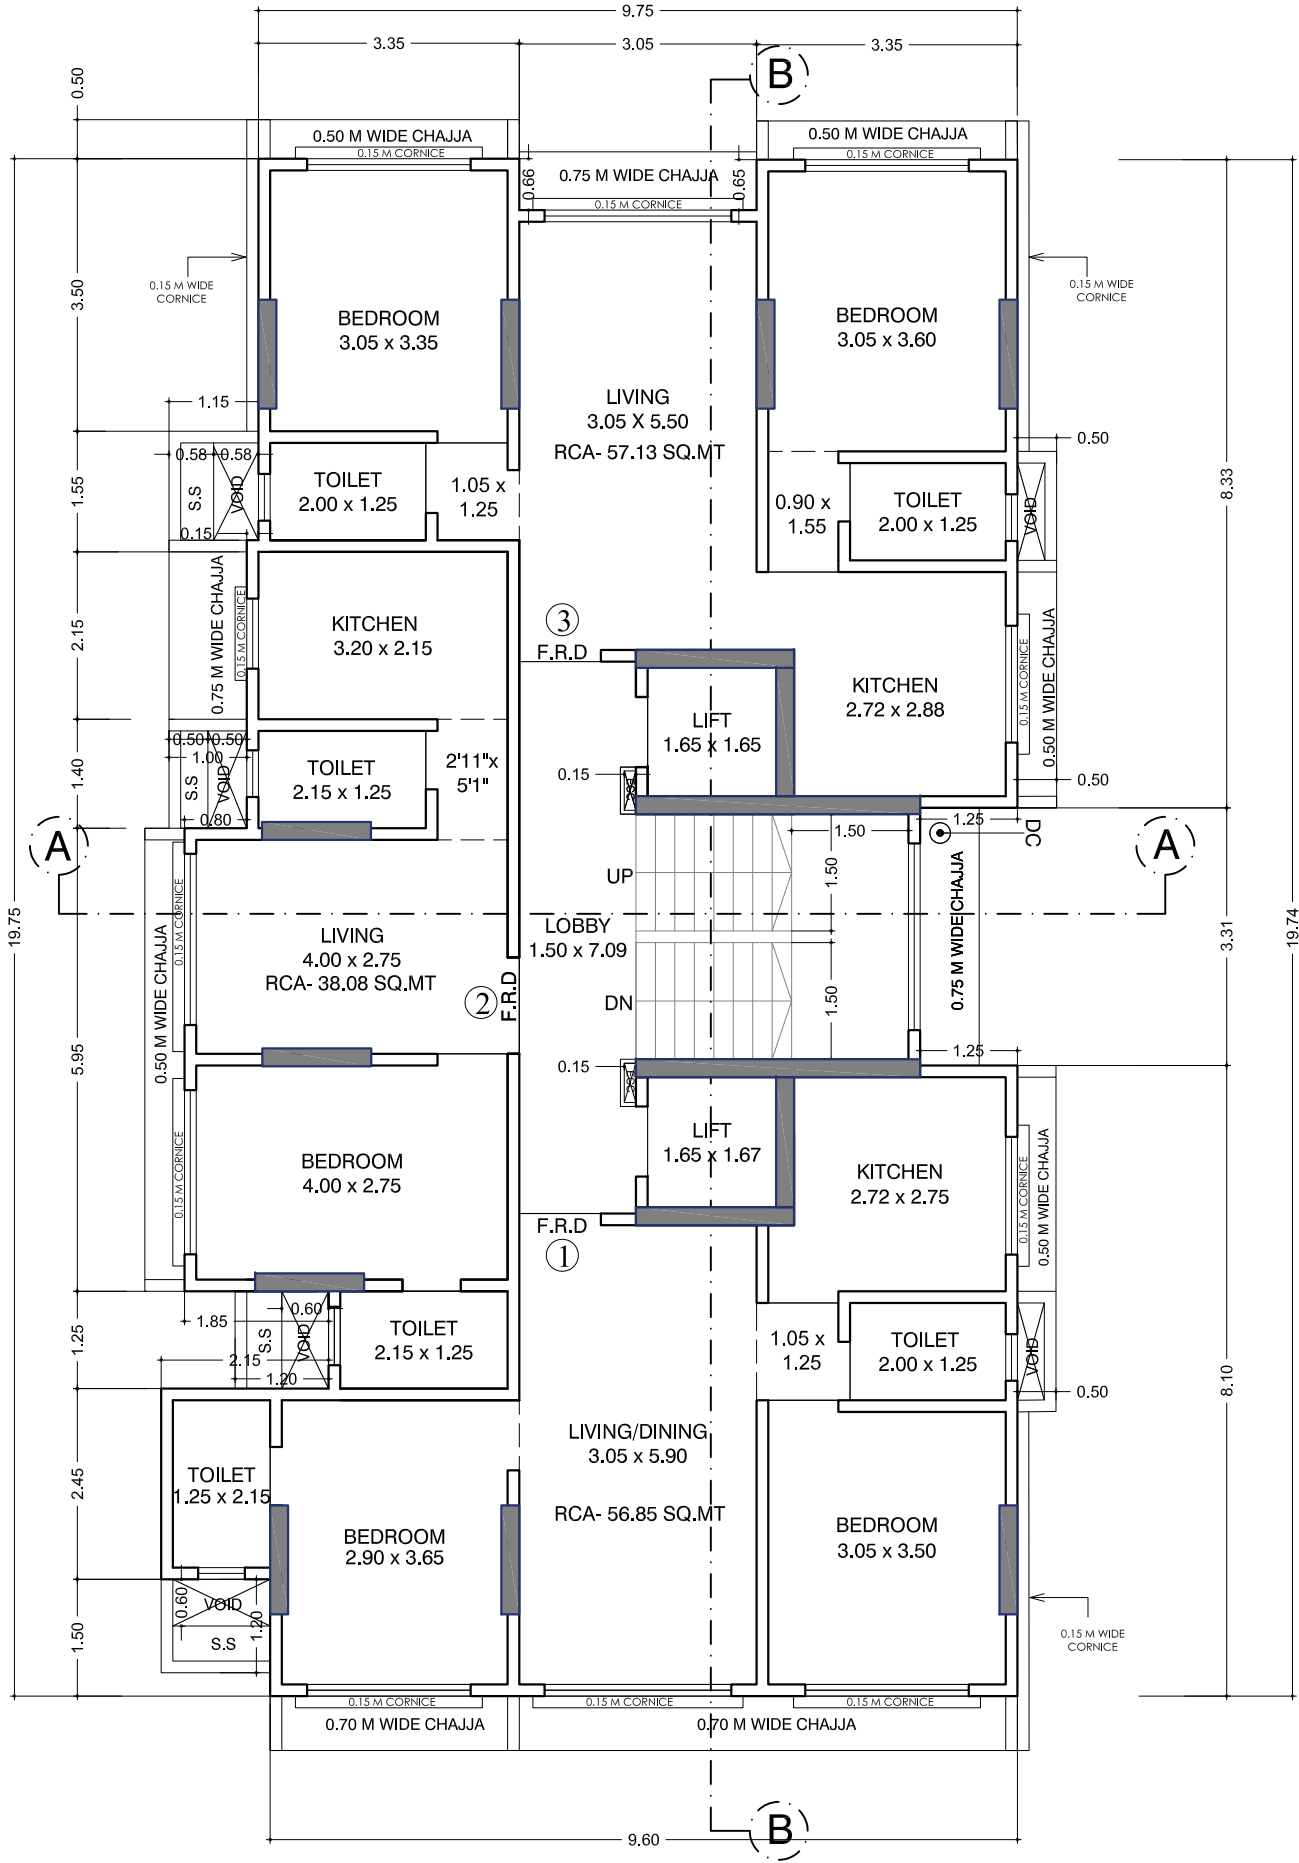

4TH FLOOR PLAN



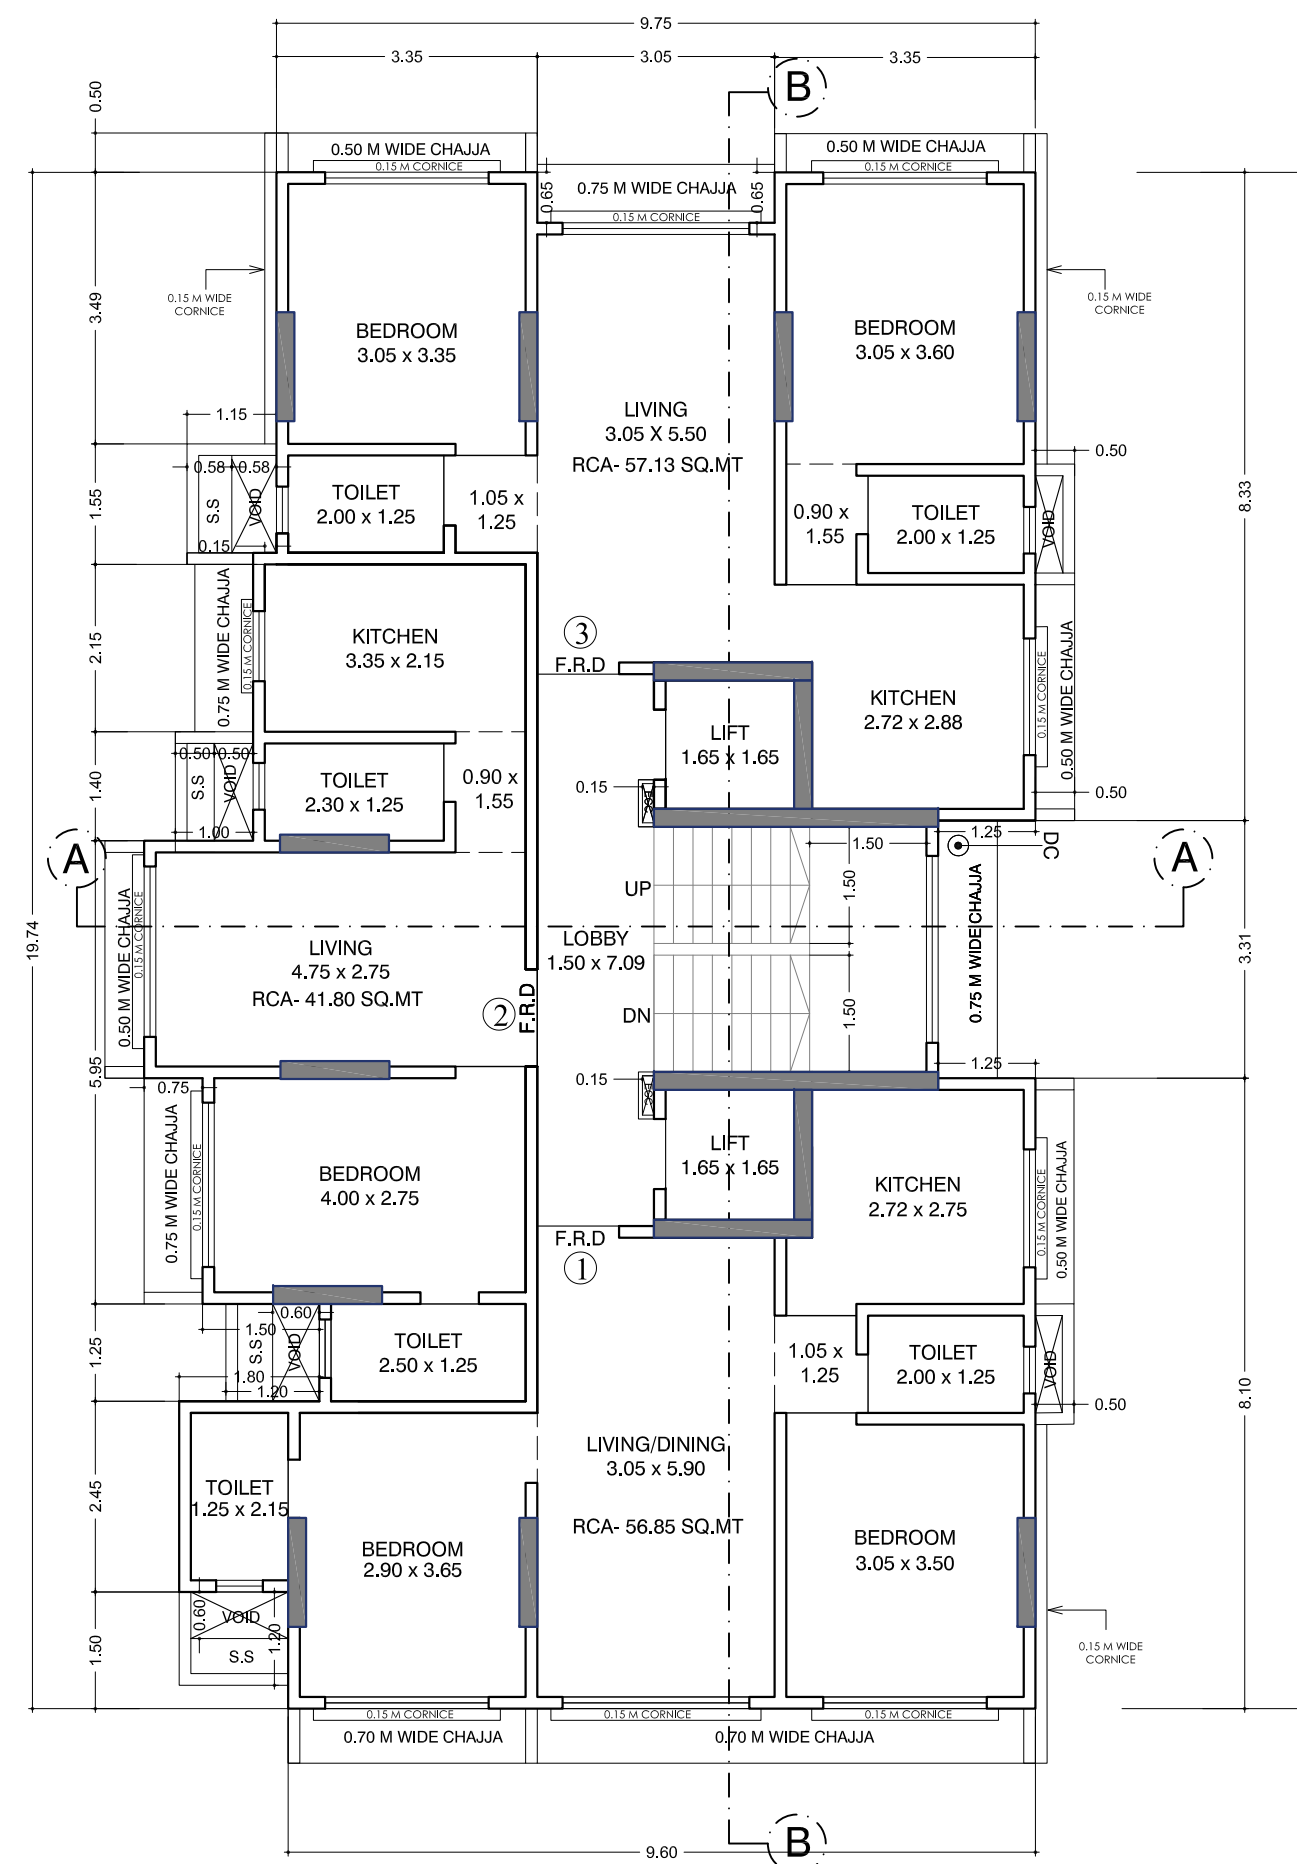


5TH TO 9TH FLOOR PLAN

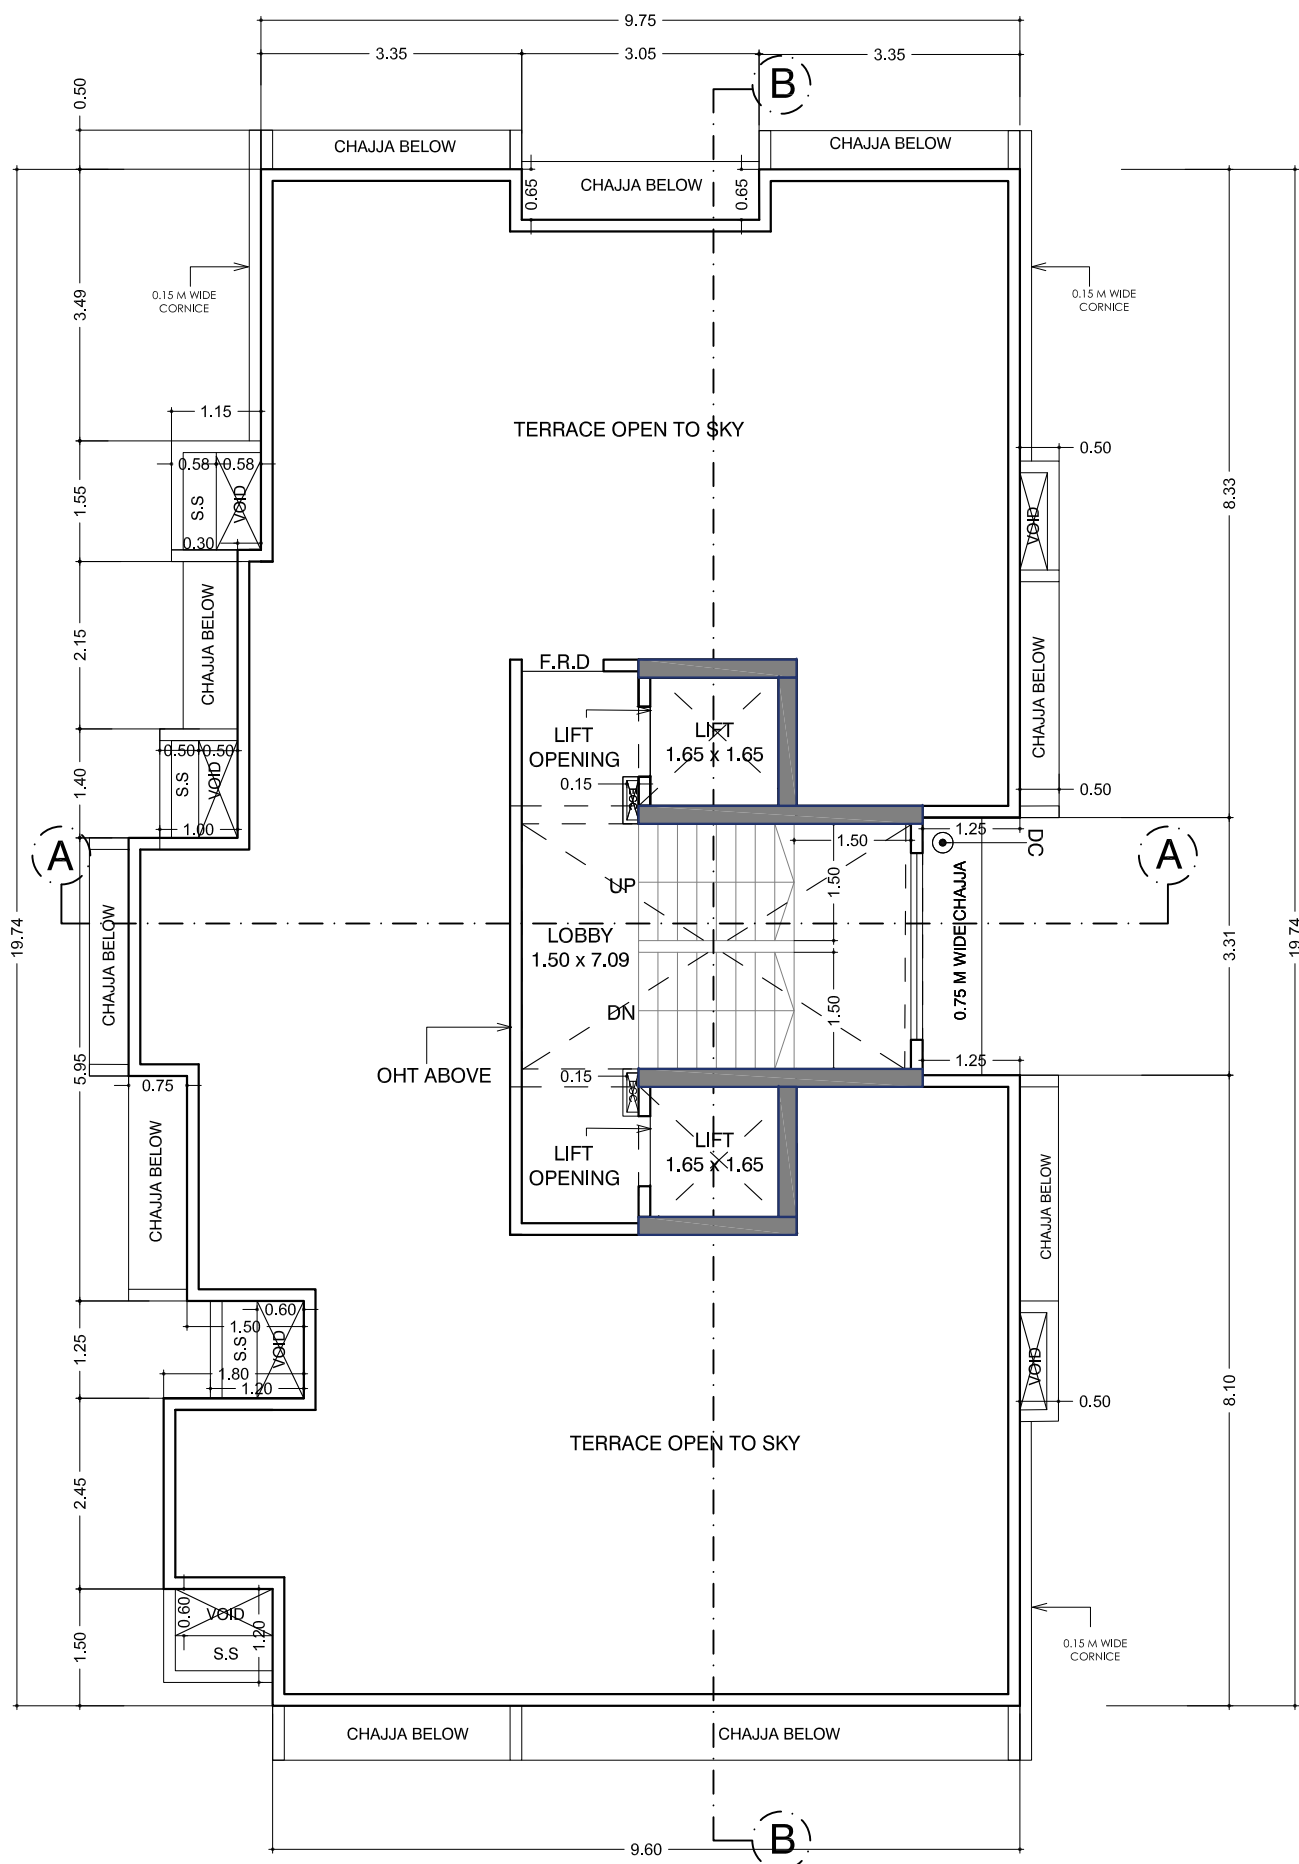


TERRACE FLOOR PLAN

FORM - II				
CONTENTS OF SHEET :				
1ST TO 9TH FLOOR PLANS				
DESCRIPTION OF PROPOSAL AND PROPERTY				
Proposed redevelopment of building known "Swavalamban Building" on plot bearing C.T.S No. (s) 785 , 785/ 1 to 785/6 of village Malad-North, Mamletdar Wadi, 6 th Cross Road, situated in P,LN Ward, Malad (W), and Mumbai.				
NAME ADDRESS & SIGNATURE OF OWNER / DEVELOPER				
Mr. Nitin Vasudev Bhandarkar, Partner of M/s. Prime Group LLP				
Level 2, Vini Elegance, Above Tanishq Jewellers, L.T.Road, Borivali (West),Mumbai-400092				
NORTH	Job no.	Drawing No.	Scale No.	Dawn By
			1:100	CHARMY
	NAME, ADDRESS & SIGNATURE OF ARCHITECT			Date No.
	MEHUL J. KANAKIA LICENSE NO. CA/2014/62291			18.11.2024
1001, BLDG NO.5 GARDEN, GROVE COMPLEX, CHIKUWADI, BORIVALI(W),MUMBAI-400092.				
SIGNATURE				
THIS DOCUMENT IS DIGITALLY SIGNED AND NO PHYSICAL SIGN IS REQUIRED				
THE PLANS FOR CONSIDERATION				
DFO		CFO		

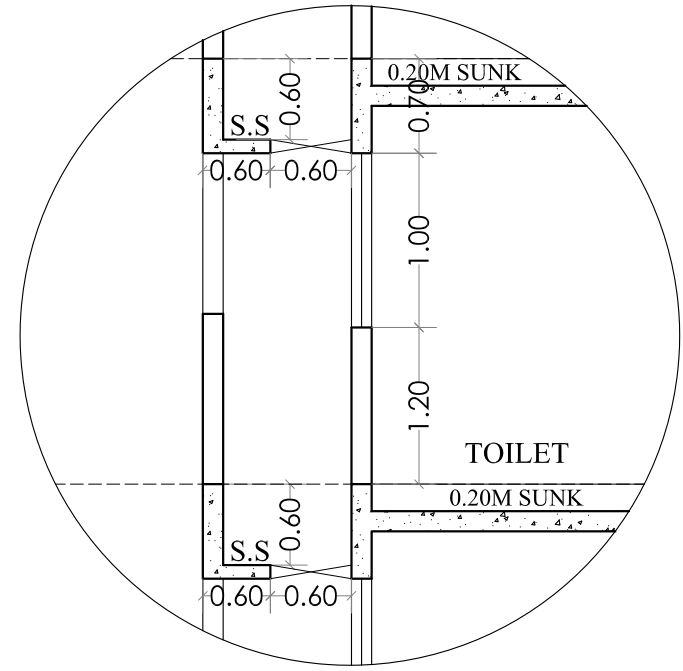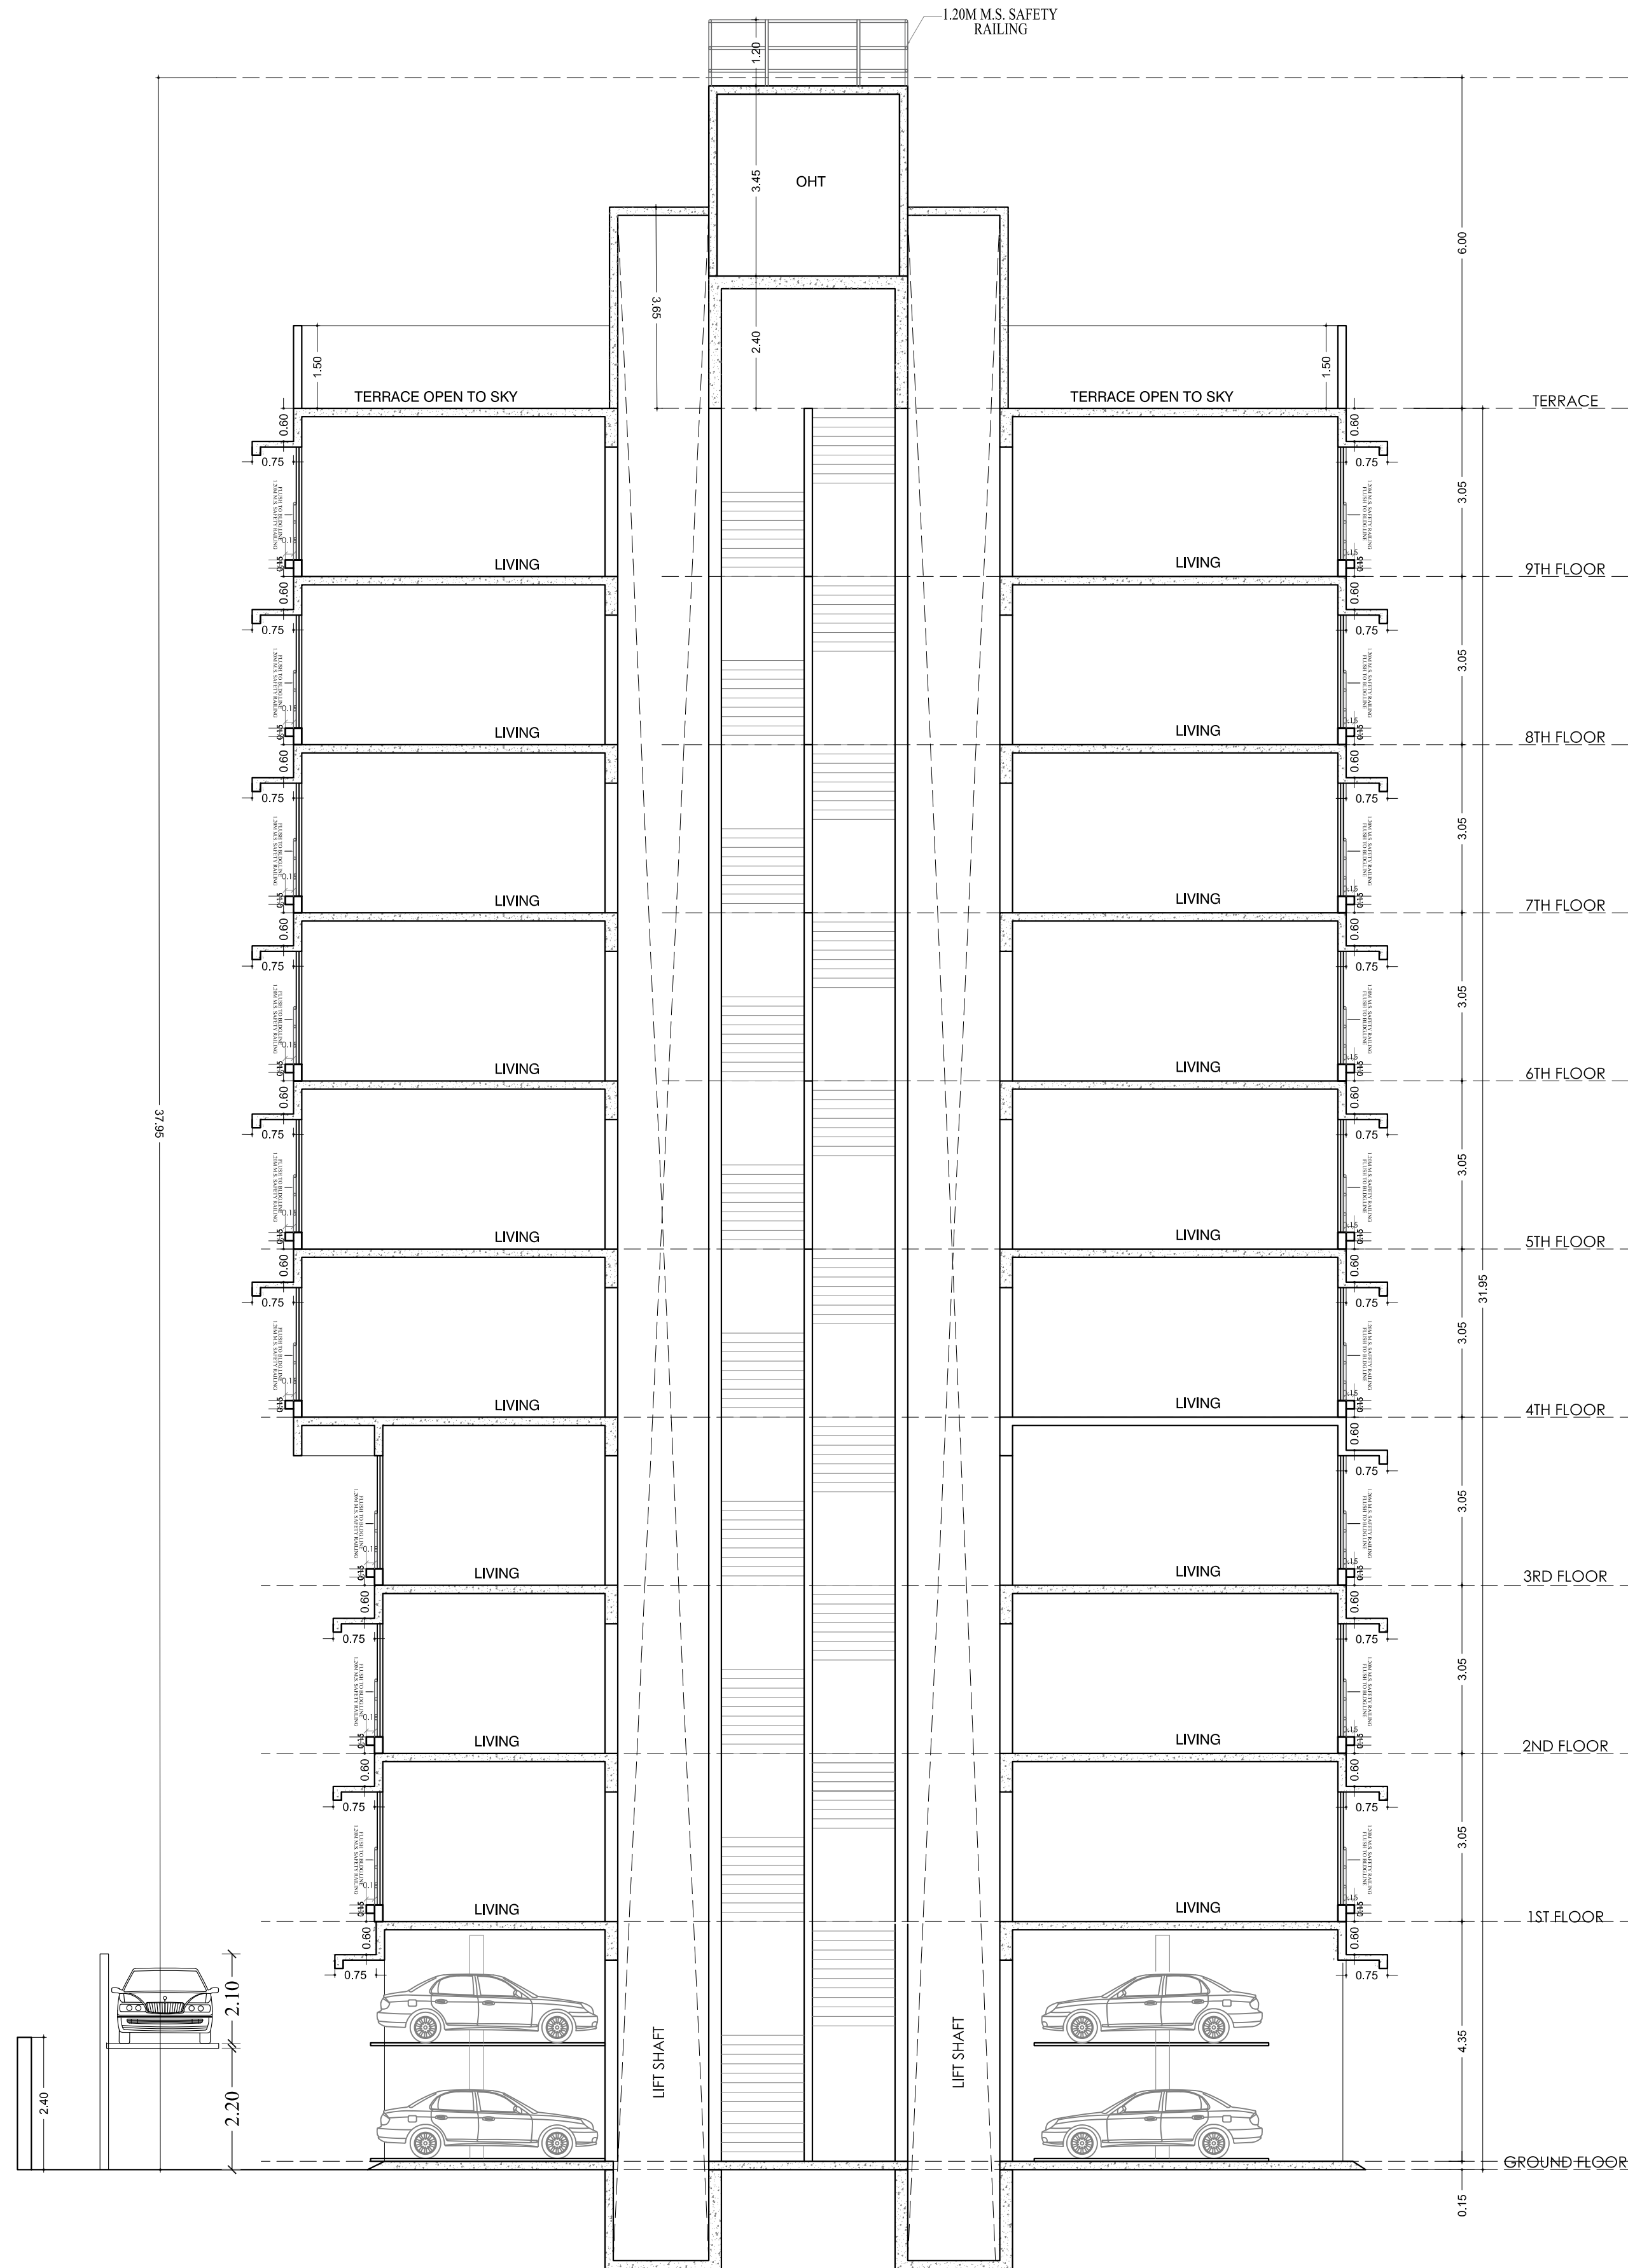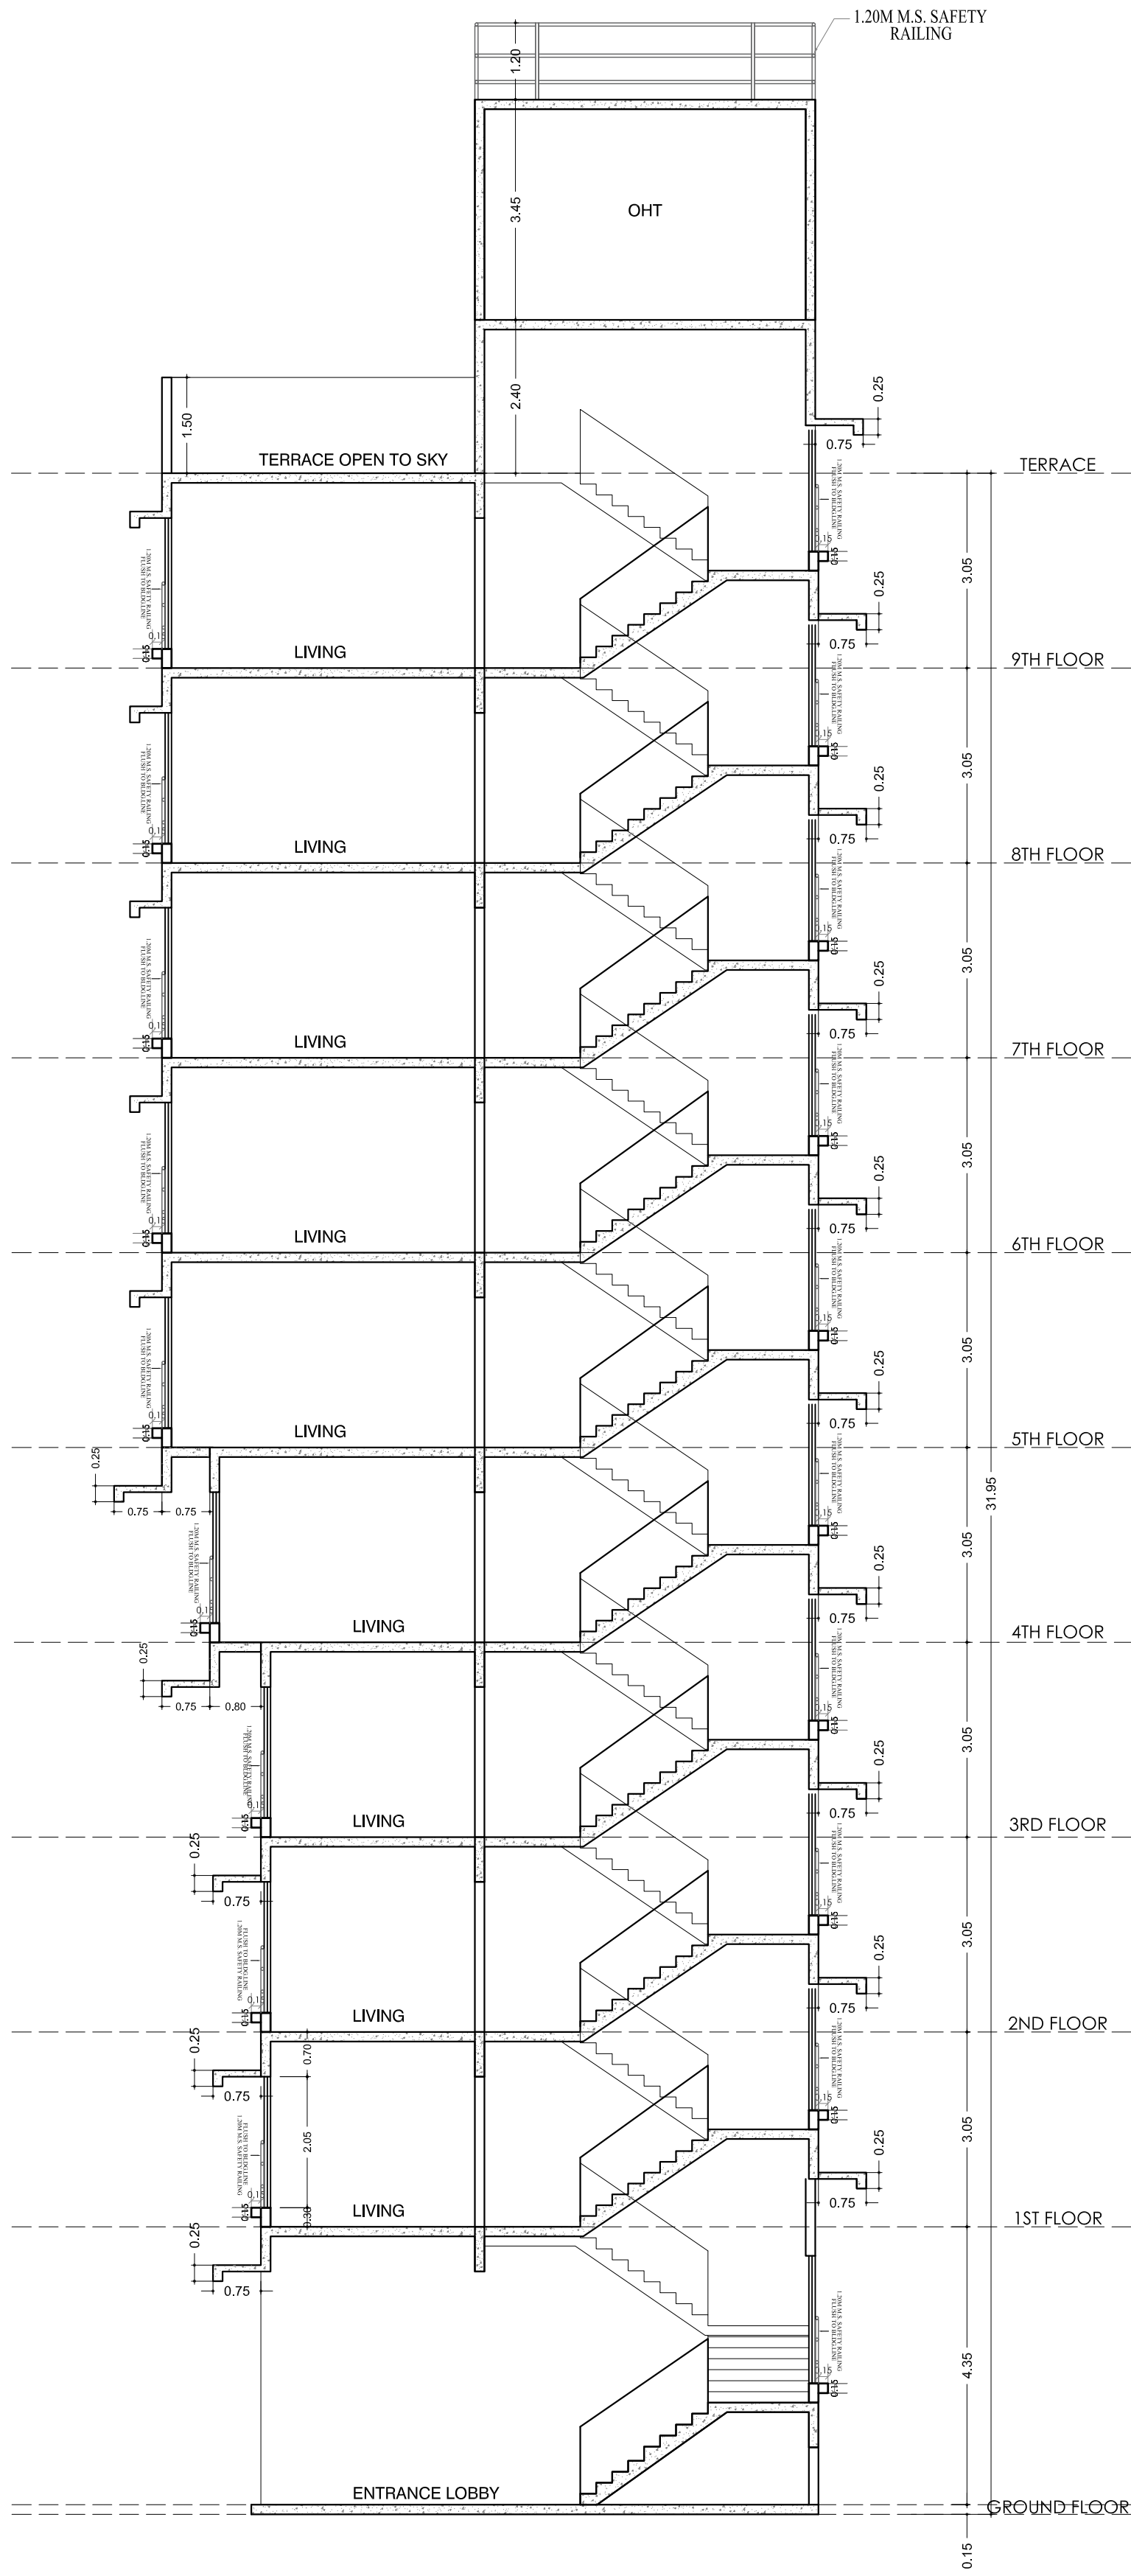

SECTION THROUGH TOILET DUCT
DETAIL A-A
SCALE 1:50

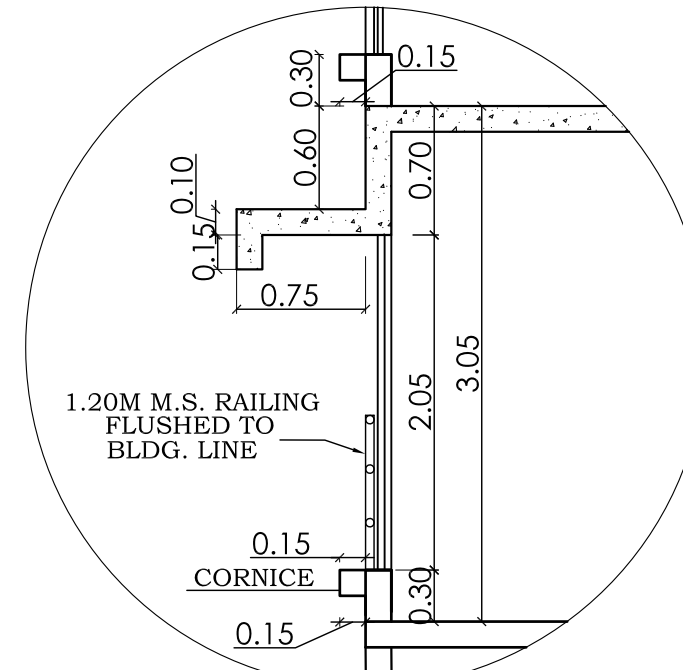

DETAILS OF B-B
SCALE - 1:50

FORM - II

CONTENTS OF SHEET :

1ST TO 9TH FLOOR PLANS

DESCRIPTION OF PROPOSAL AND PROPERTY


Proposed redevelopment of building known "Swavalamban Building" on plot bearing C.T.S No. (s) 785 , 785/ 1 to 785/6 of village Malad-North, Mamletdar Wadi, 6 th Cross Road, situated in P,LN Ward, Malad (W), and Mumbai.

NAME ADDRESS & SIGNATURE OF OWNER / DEVELOPER

Mr. Nitin Vasudev Bhandarkar, Partner of M/s.
Prime Group LLP

Level 2, Vini Elegance, Above Tanishq Jewellers,
L.T.Road, Borivali (West),Mumbai-400092

NORTH

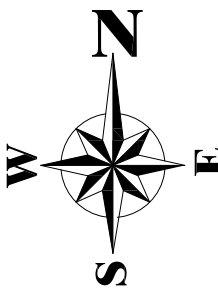

Job no.	Drawing No.	Scale No.	Dawn By	Date No.
		1:100	CHARMY	18.11.2024

NAME, ADDRESS & SIGNATURE OF ARCHITECT

MEHUL J. KANAKIA
LICENSE NO. CA/2014/62291

1001, BLDG NO.5 GARDEN,
GROVE COMPLEX, CHIKUWADI,
BORIVALI(W),MUMBAI-400092.

SIGNATURE

THIS DOCUMENT IS DIGITALLY SIGNED AND NO PHYSICAL SIGN IS REQUIRED

THE PLANS FOR CONSIDERATION

DFO

CFO