


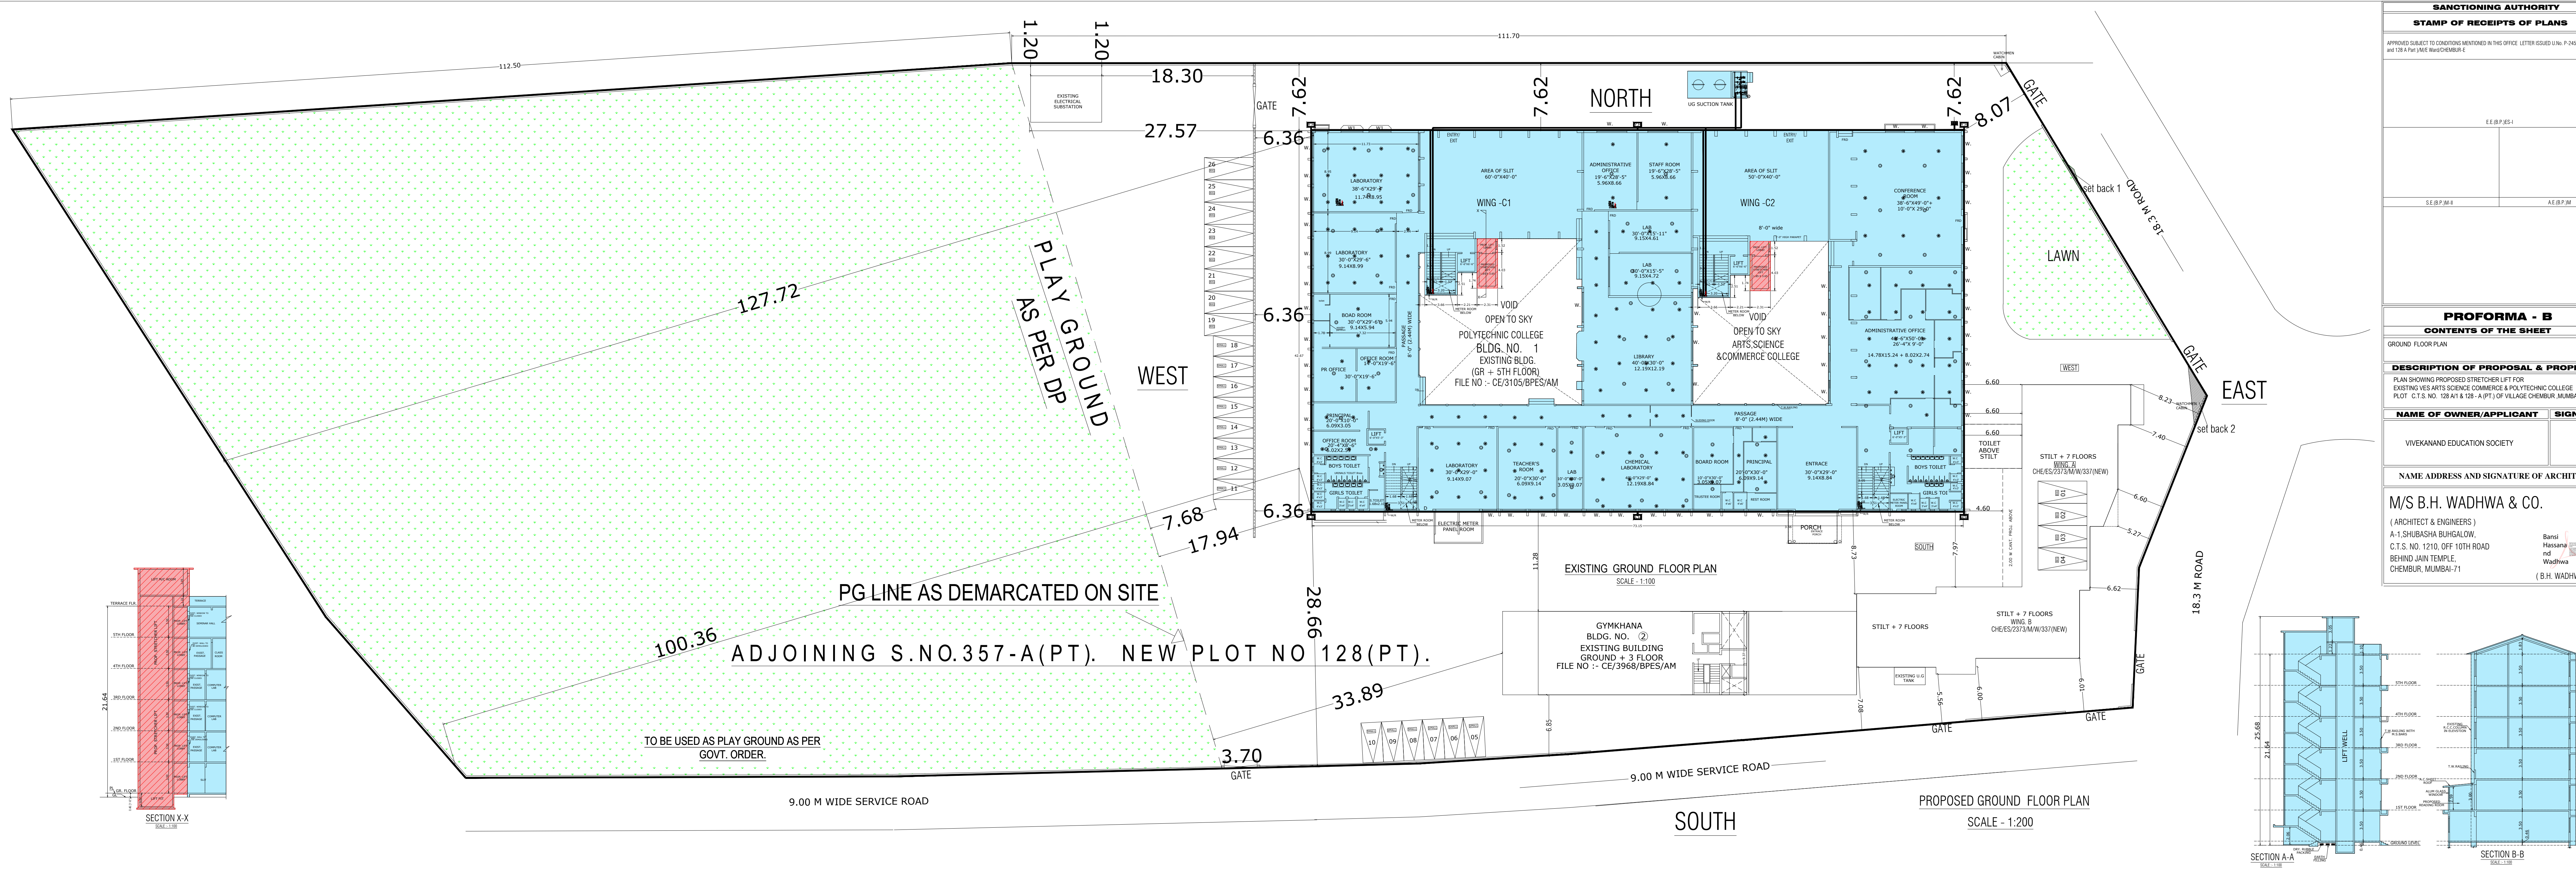


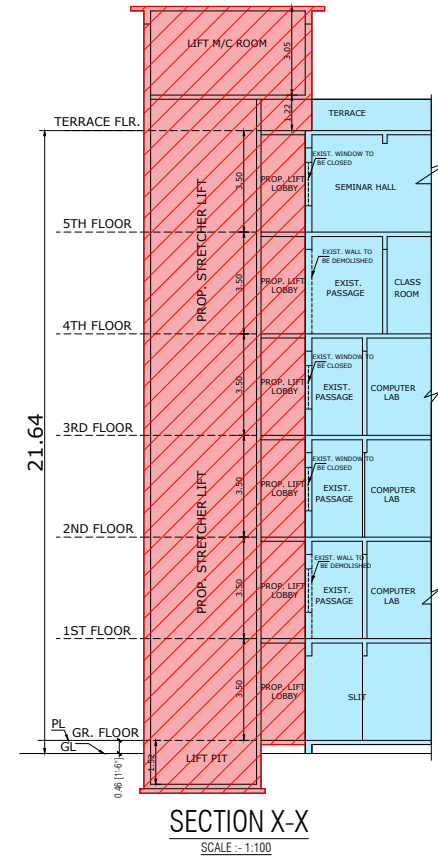


SANCTIONING AUTHORITY		2/8
STAMP OF RECEIPTS OF PLANS		
APPROVED SUBJECT TO CONDITIONS MENTIONED IN THIS OFFICE LETTER ISSUED U.No. P-24534/2024/(128 A/1 and 128 A Part I/M/E Ward/CHEMBUR E		
E.E.(B.P.)ES-I		
S.E.(B.P.)JM-I		A.E.(B.P.)JM

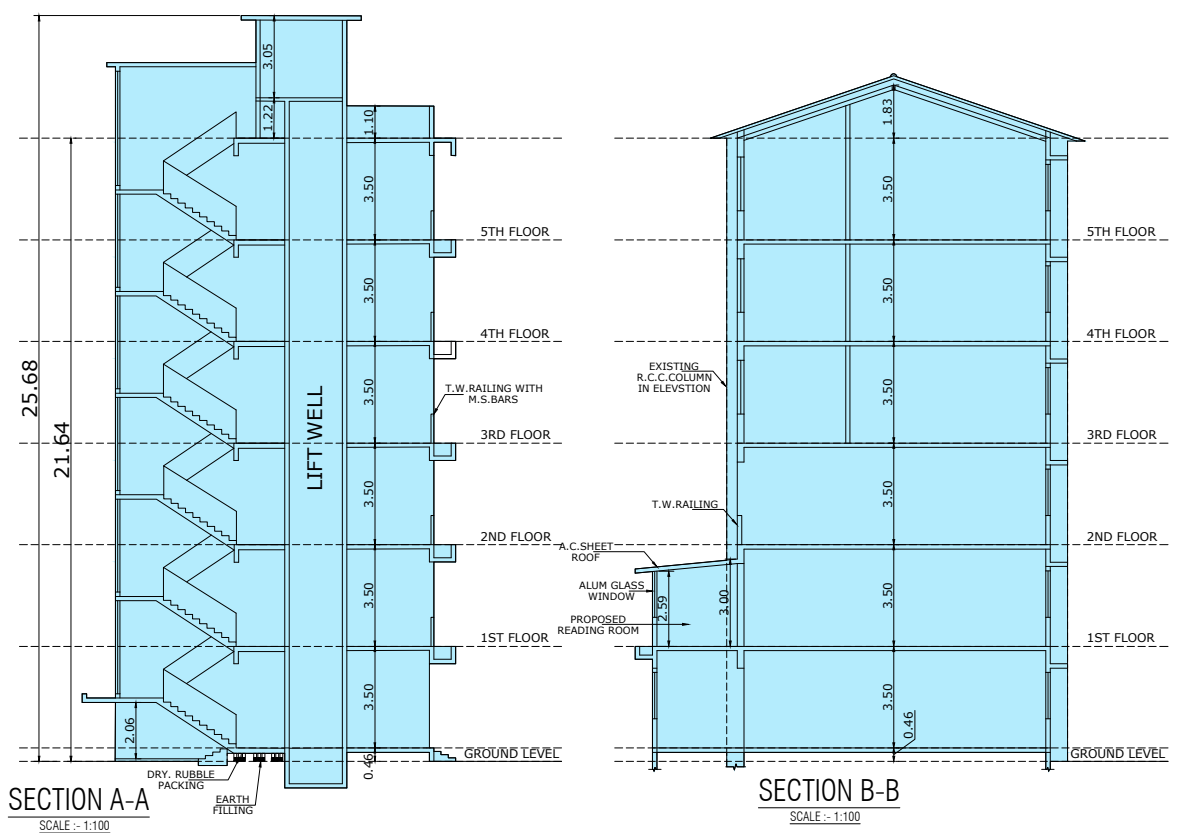

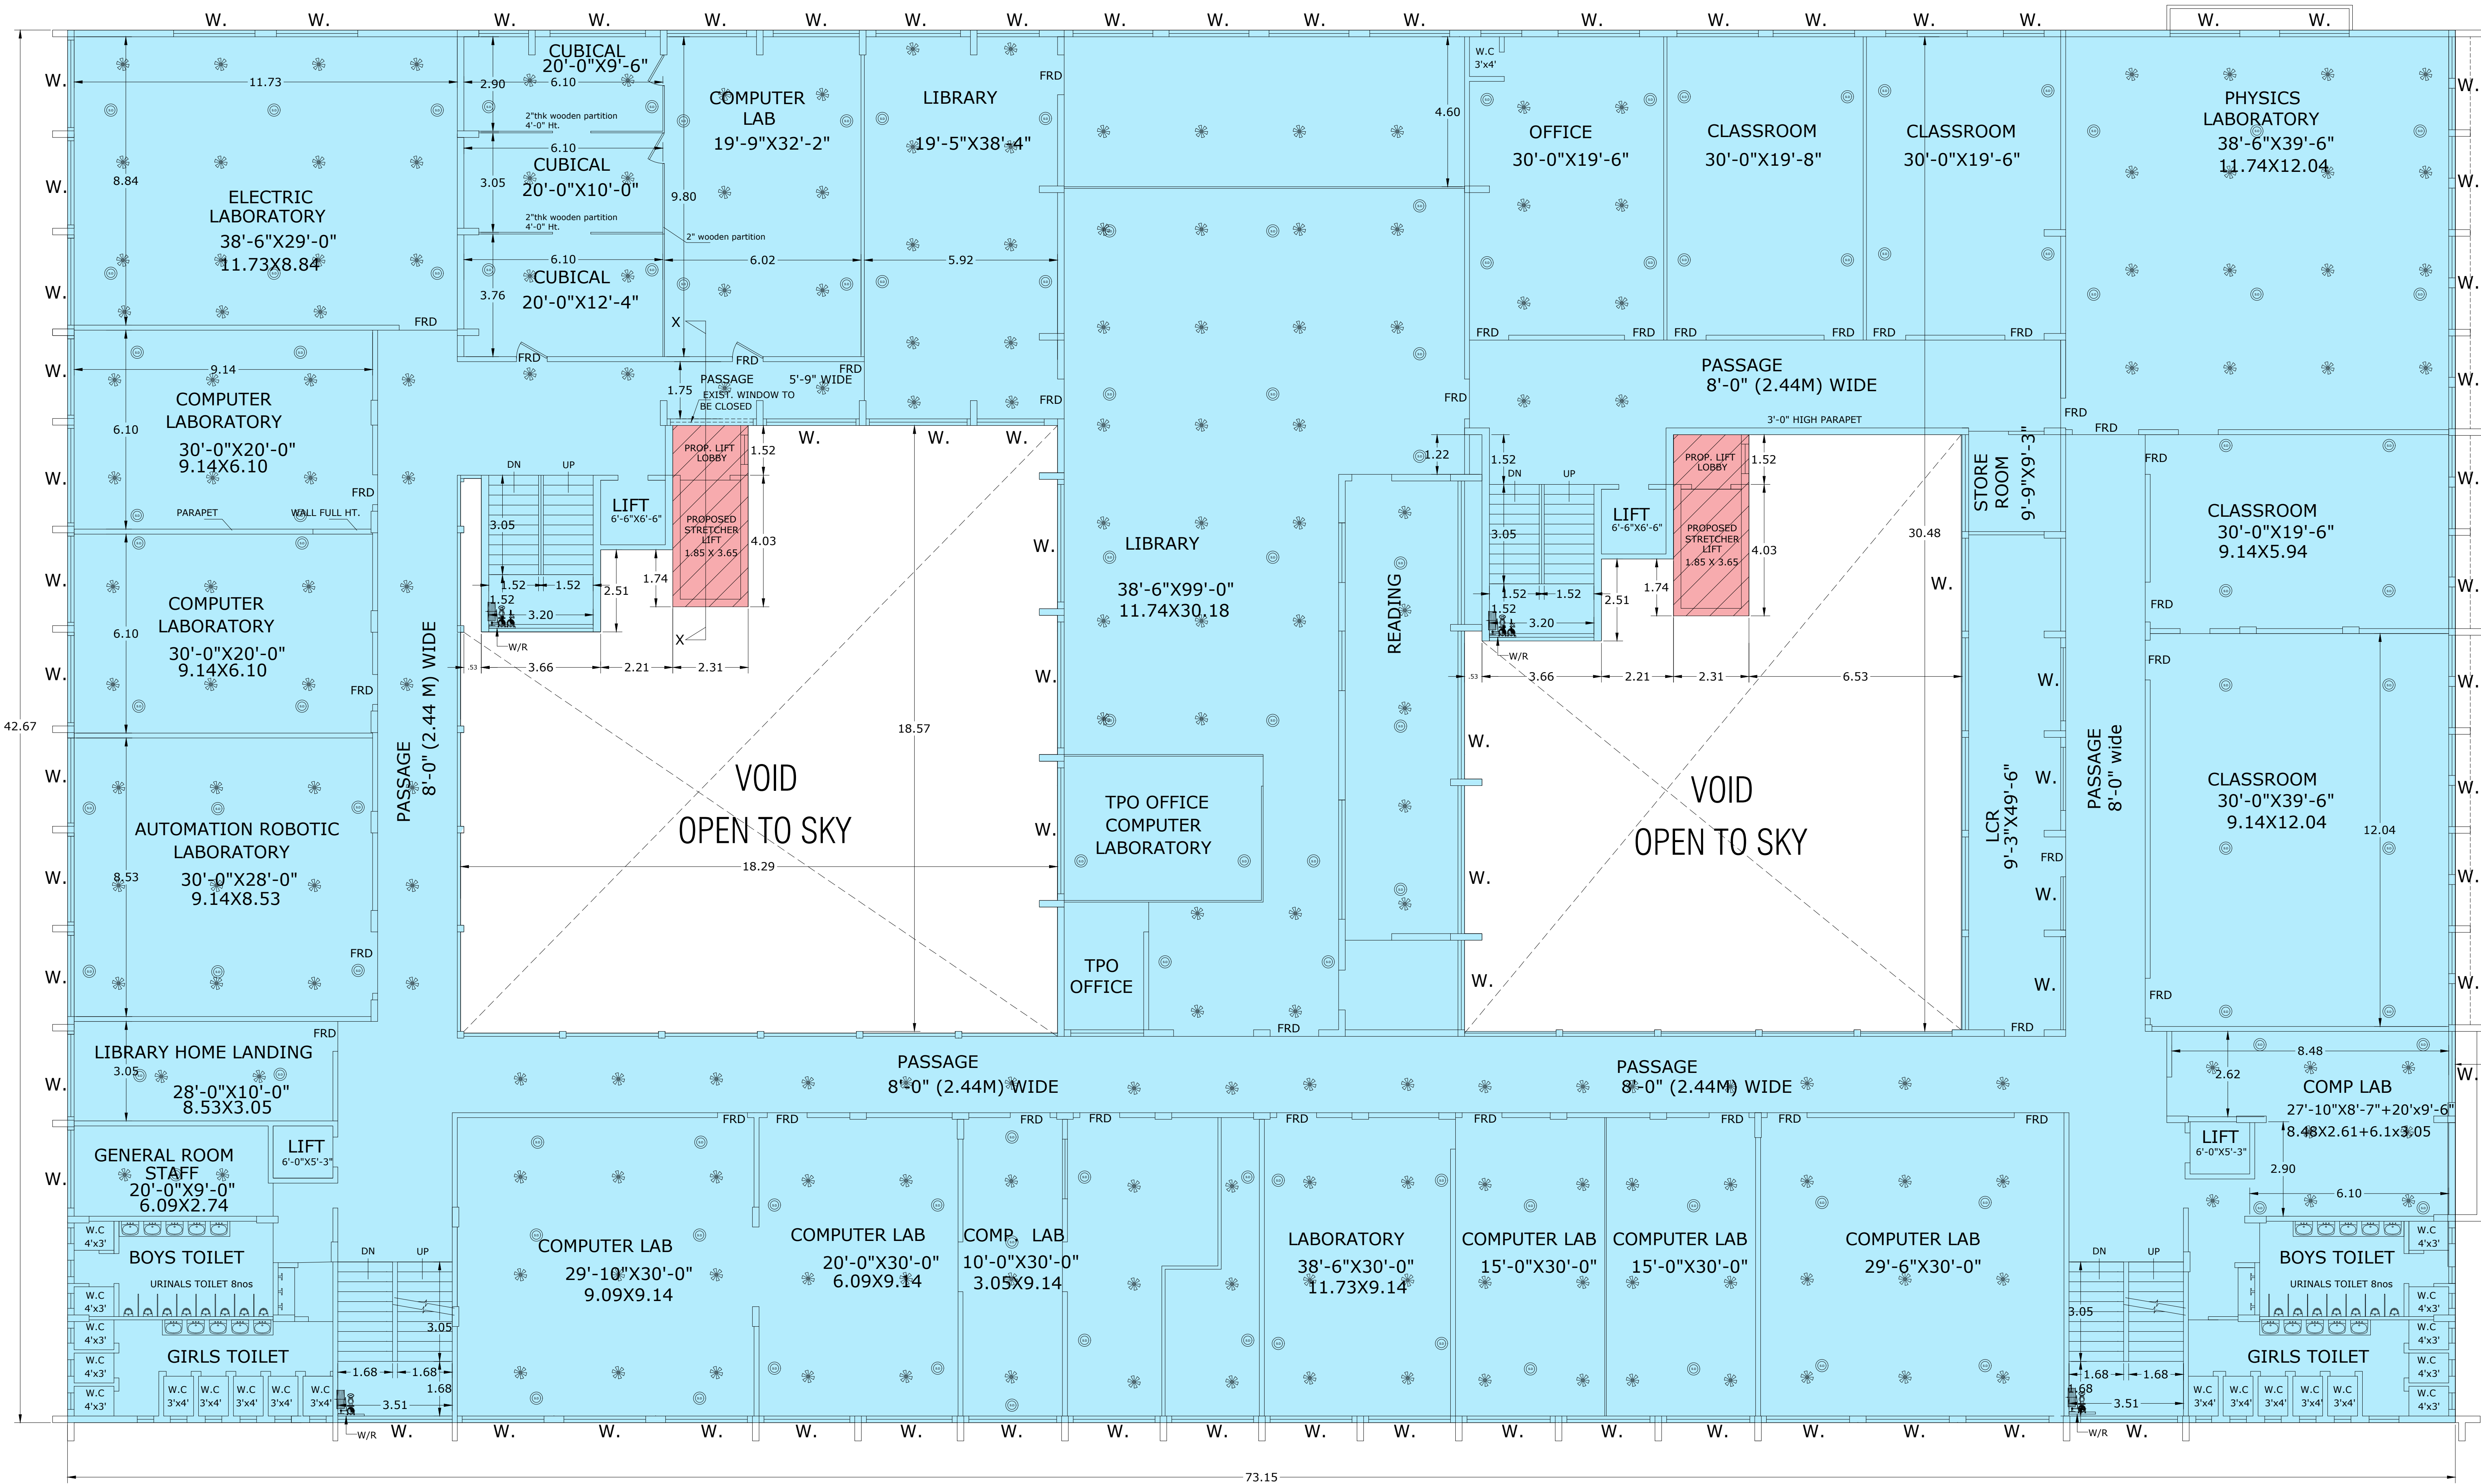

EXISTING FIRST FLOOR PLAN
SCALE : 1:100

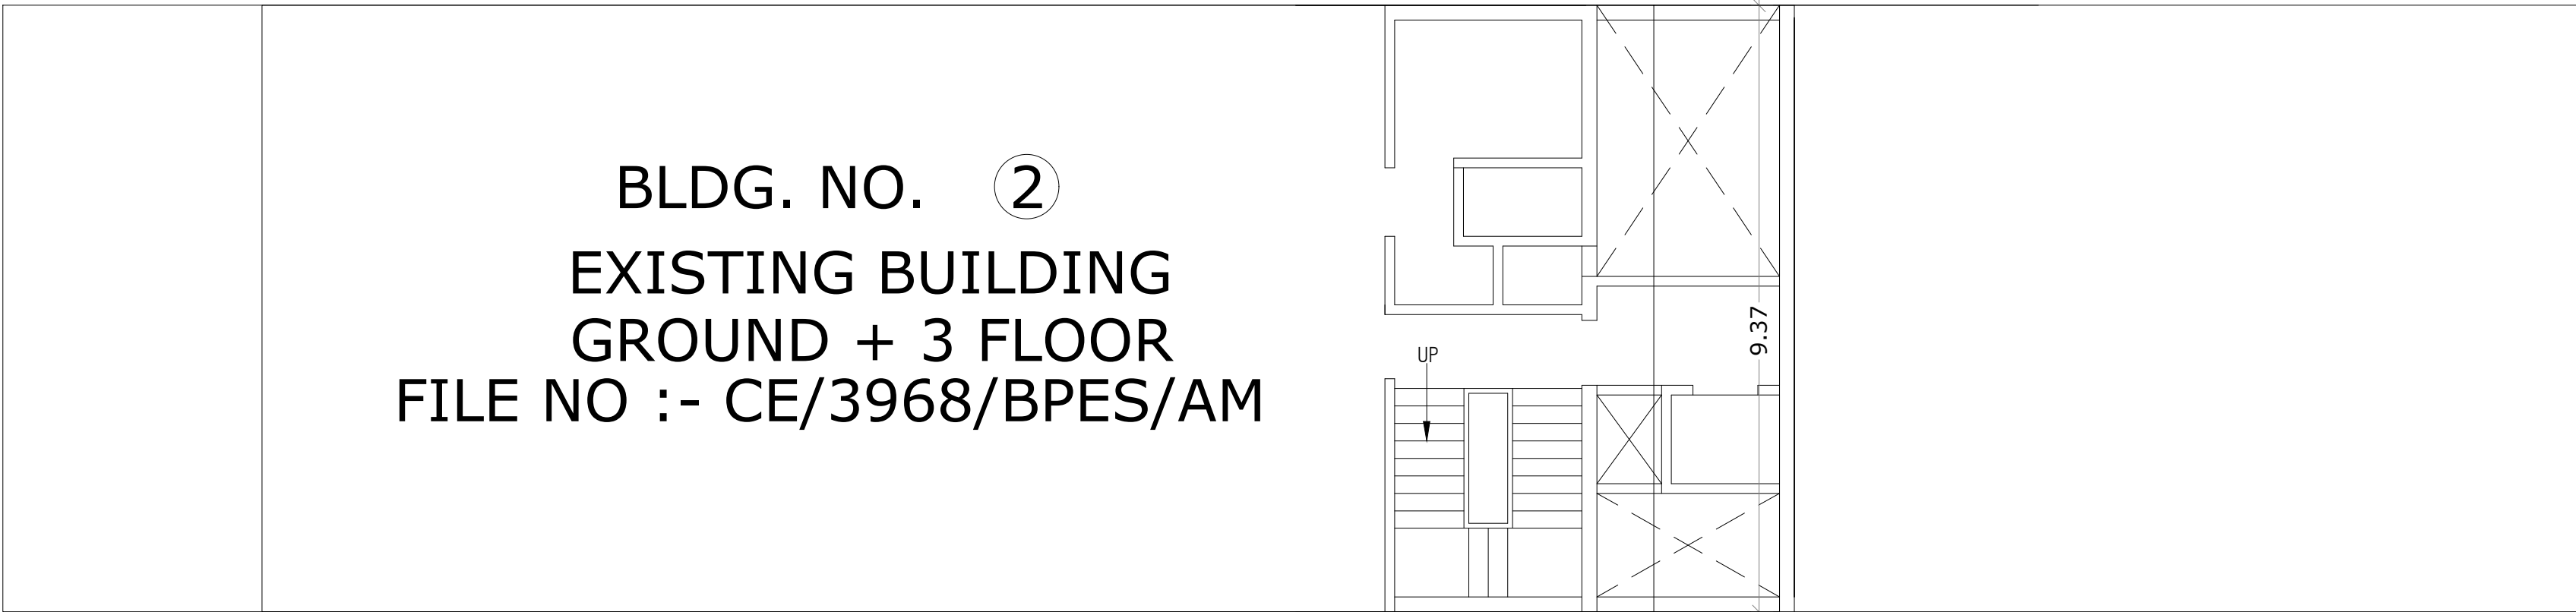


PROPOSED FIRST FLOOR PLAN
SCALE :- 1:100


SANCTIONING AUTHORITY		3/8
STAMP OF RECEIPTS OF PLANS		
APPROVED SUBJECT TO CONDITIONS MENTIONED IN THIS OFFICE LETTER ISSUED U.No. P-24534/2024/(128 A/1 and 128 A Part)/M/E Ward/CHEMBUR-E		
E.E.(B.P.)ES-I		
S.E.(B.P.)M-II		A.E.(B.P.)M
PROFORMA - B		
CONTENTS OF THE SHEET		
FIRST FLOOR PLAN		
DESCRIPTION OF PROPOSAL & PROPERTY		
PLAN SHOWING PROPOSED STRETCHER LIFT FOR EXISTING VES ARTS SCIENCE COMMERCE & POLYTECHNIC COLLEGE. BUILDING AT PLOT C.T.S. NO. 128 A/1 & 128 - A (PT.) OF VILLAGE CHEMBUR, MUMBAI - 400 071		
NAME OF OWNER/APPLICANT	SIGNATURE	
VIVEKANAND EDUCATION SOCIETY		
NAME ADDRESS AND SIGNATURE OF ARCHITECT		
M/S B.H. WADHWA & CO.		
(ARCHITECT & ENGINEERS)		
A-1,SHUBASHA BUNHALOW, C.T.S. NO. 1210, OFF 10TH ROAD BEHIND JAIN TEMPLE, CHEMBUR, MUMBAI-71		
Bansi Hassanand Wadhwa (B.H. WADHWA)		

STILT + 7 FLOORS
WING. A
CHE/ES/2373/M/W/337(NEW)

STILT + 7 FLOORS
WING. B
CHE/ES/2373/M/W/337(NEW)

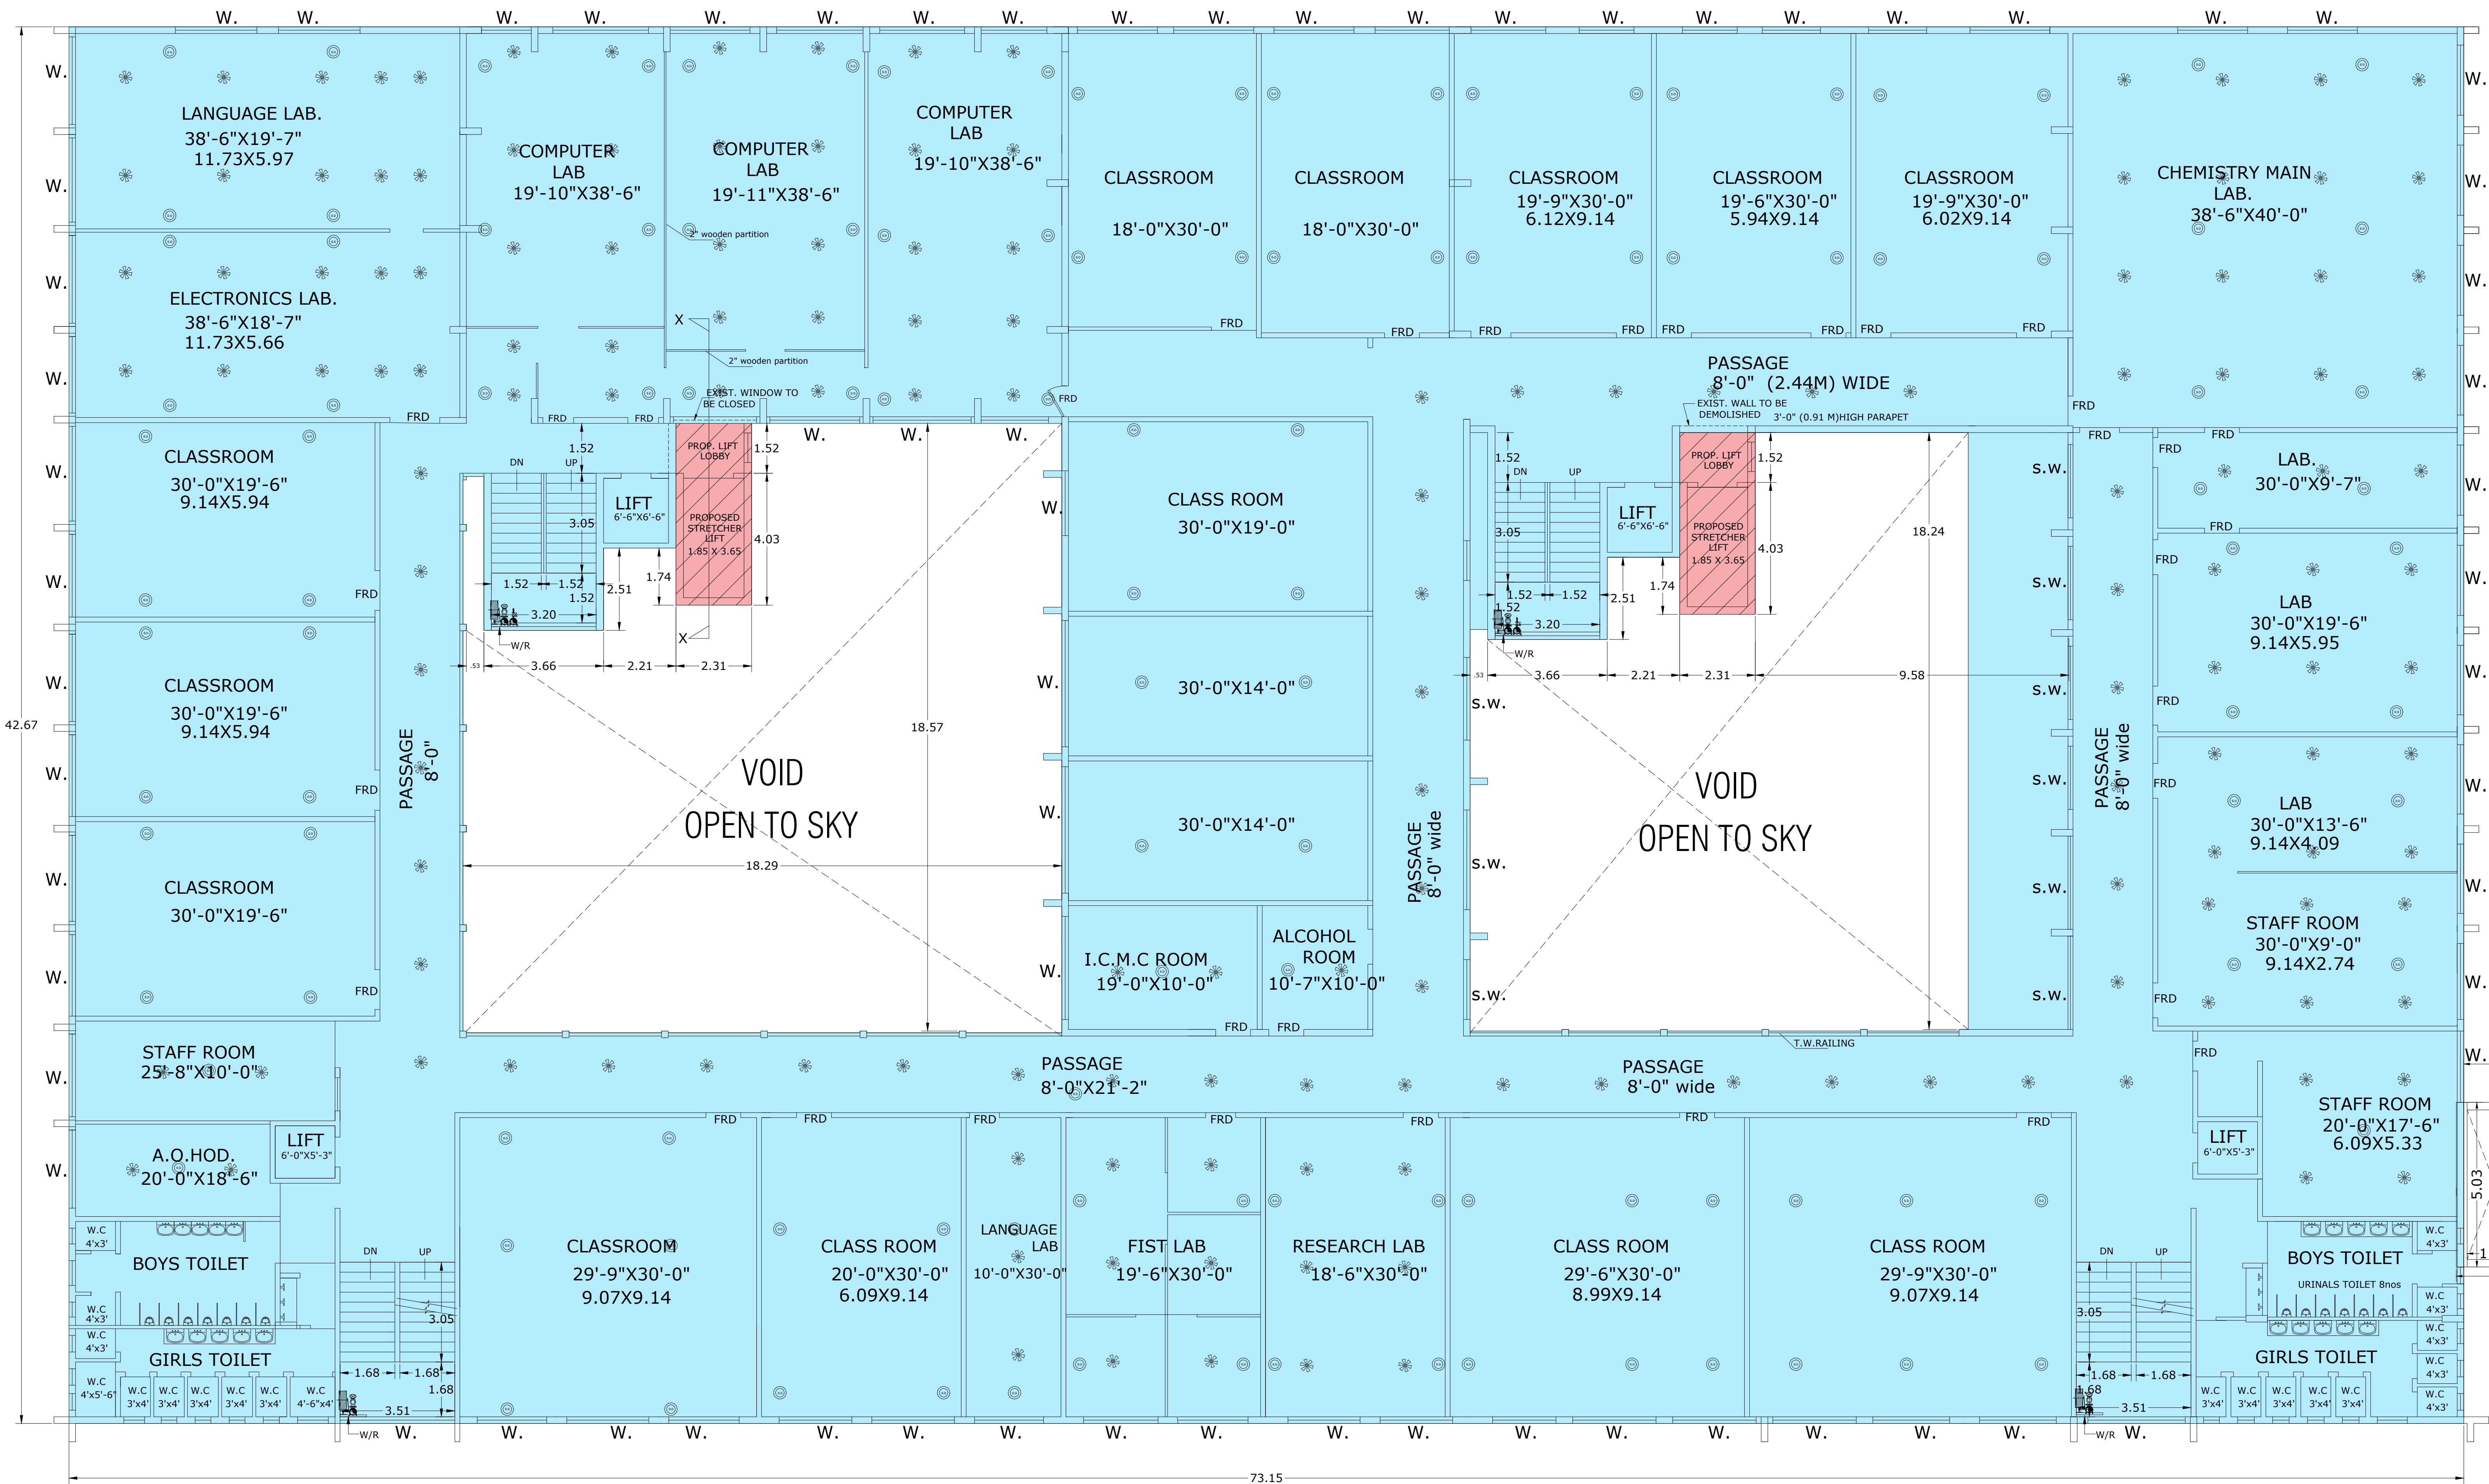


EXISTING SECOND FLOOR PLAN
SCALE : 1:100

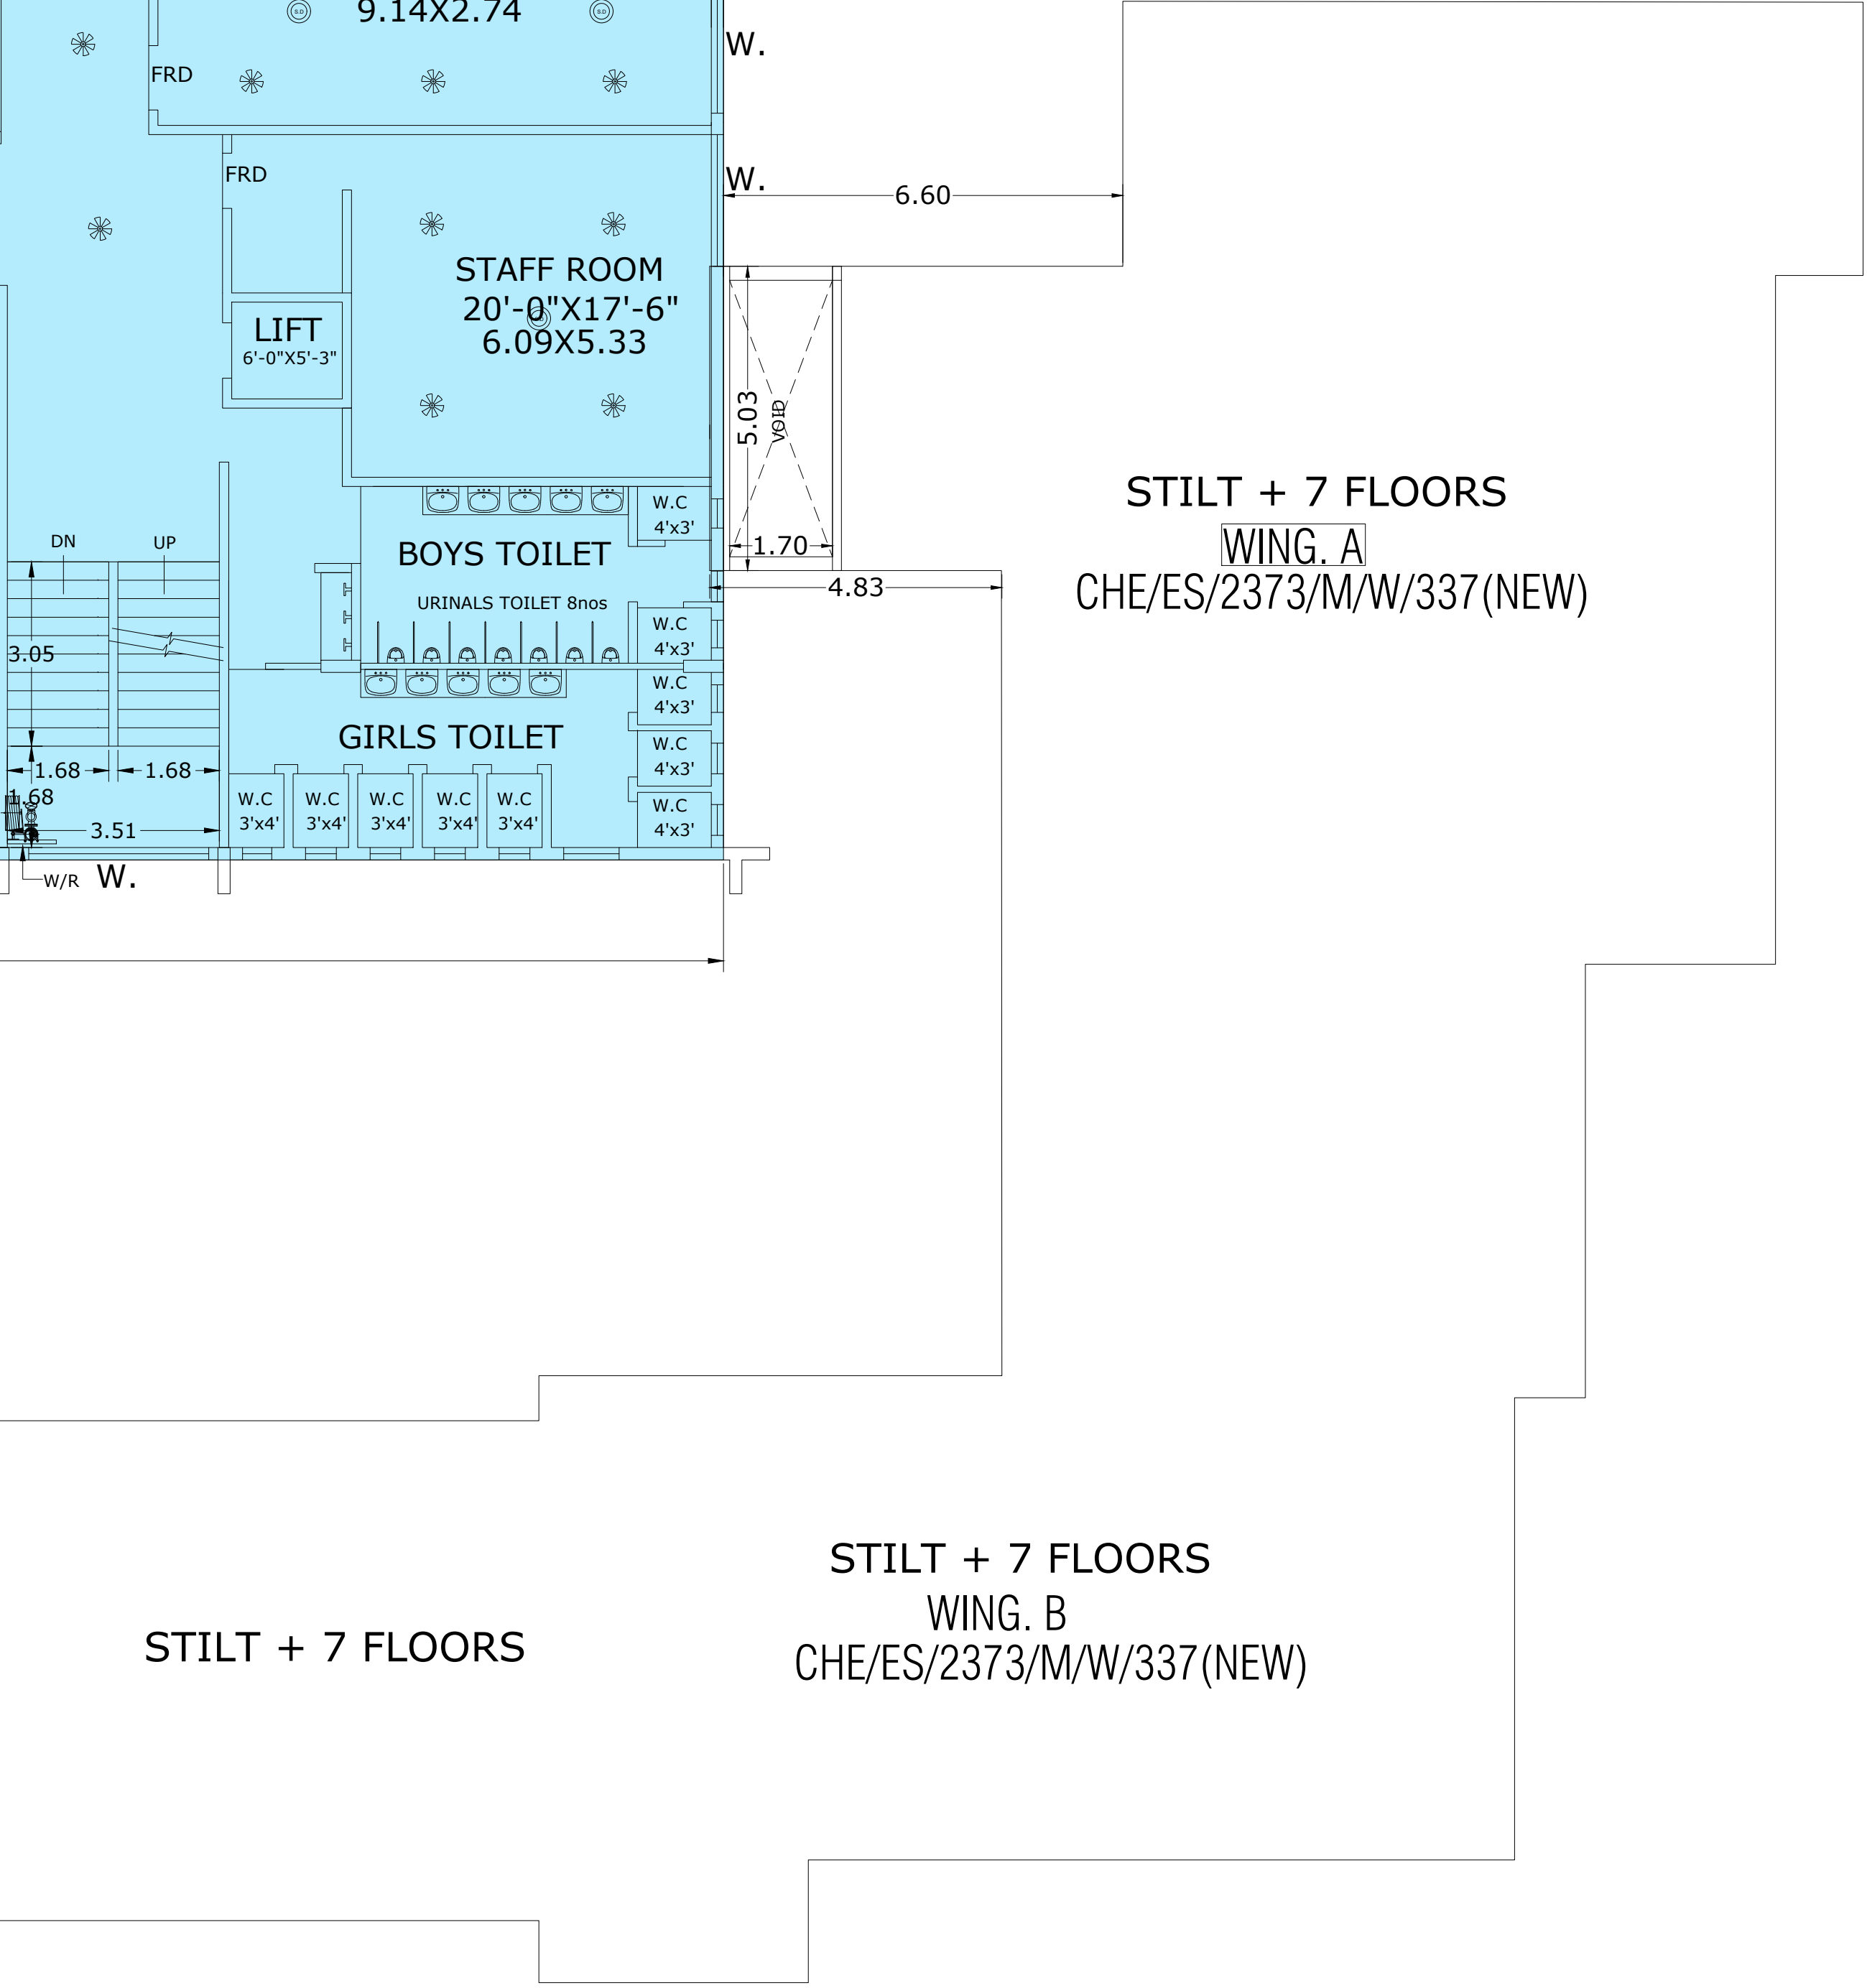


SECOND FLOOR PLAN
SCALE :- 1:100

SANCTIONING AUTHORITY		4/8
STAMP OF RECEIPTS OF PLANS		
APPROVED SUBJECT TO CONDITIONS MENTIONED IN THIS OFFICE LETTER ISSUED U.No. P-24534/2024/(128 A/1 and 128 A Part)/M/E Ward/CHEMBUR-E		
E.E.(B.P.)ES-I		
S.E.(B.P.)M-II		A.E.(B.P.)M
PROFORMA - B		
CONTENTS OF THE SHEET		
SECOND FLOOR PLAN		
DESCRIPTION OF PROPOSAL & PROPERTY		
PLAN SHOWING PROPOSED STRETCHER LIFT FOR EXISTING VES ARTS SCIENCE COMMERCE & POLYTECHNIC COLLEGE BUILDING AT PLOT C.T.S. NO. 128 A/1 & 128 - A (PT.) OF VILLAGE CHEMBUR, MUMBAI - 400 071		
NAME OF OWNER/APPLICANT	SIGNATURE	
VIVEKANAND EDUCATION SOCIETY		
NAME ADDRESS AND SIGNATURE OF ARCHITECT		
M/S B.H. WADHWA & CO.		
(ARCHITECT & ENGINEERS)		
A-1,SHUBASHA BUHGALOW, C.T.S. NO. 1210, OFF 10TH ROAD BEHIND JAIN TEMPLE, CHEMBUR, MUMBAI-71		
Bansi Hassana nd Wadhwa		(B.H. WADHWA)

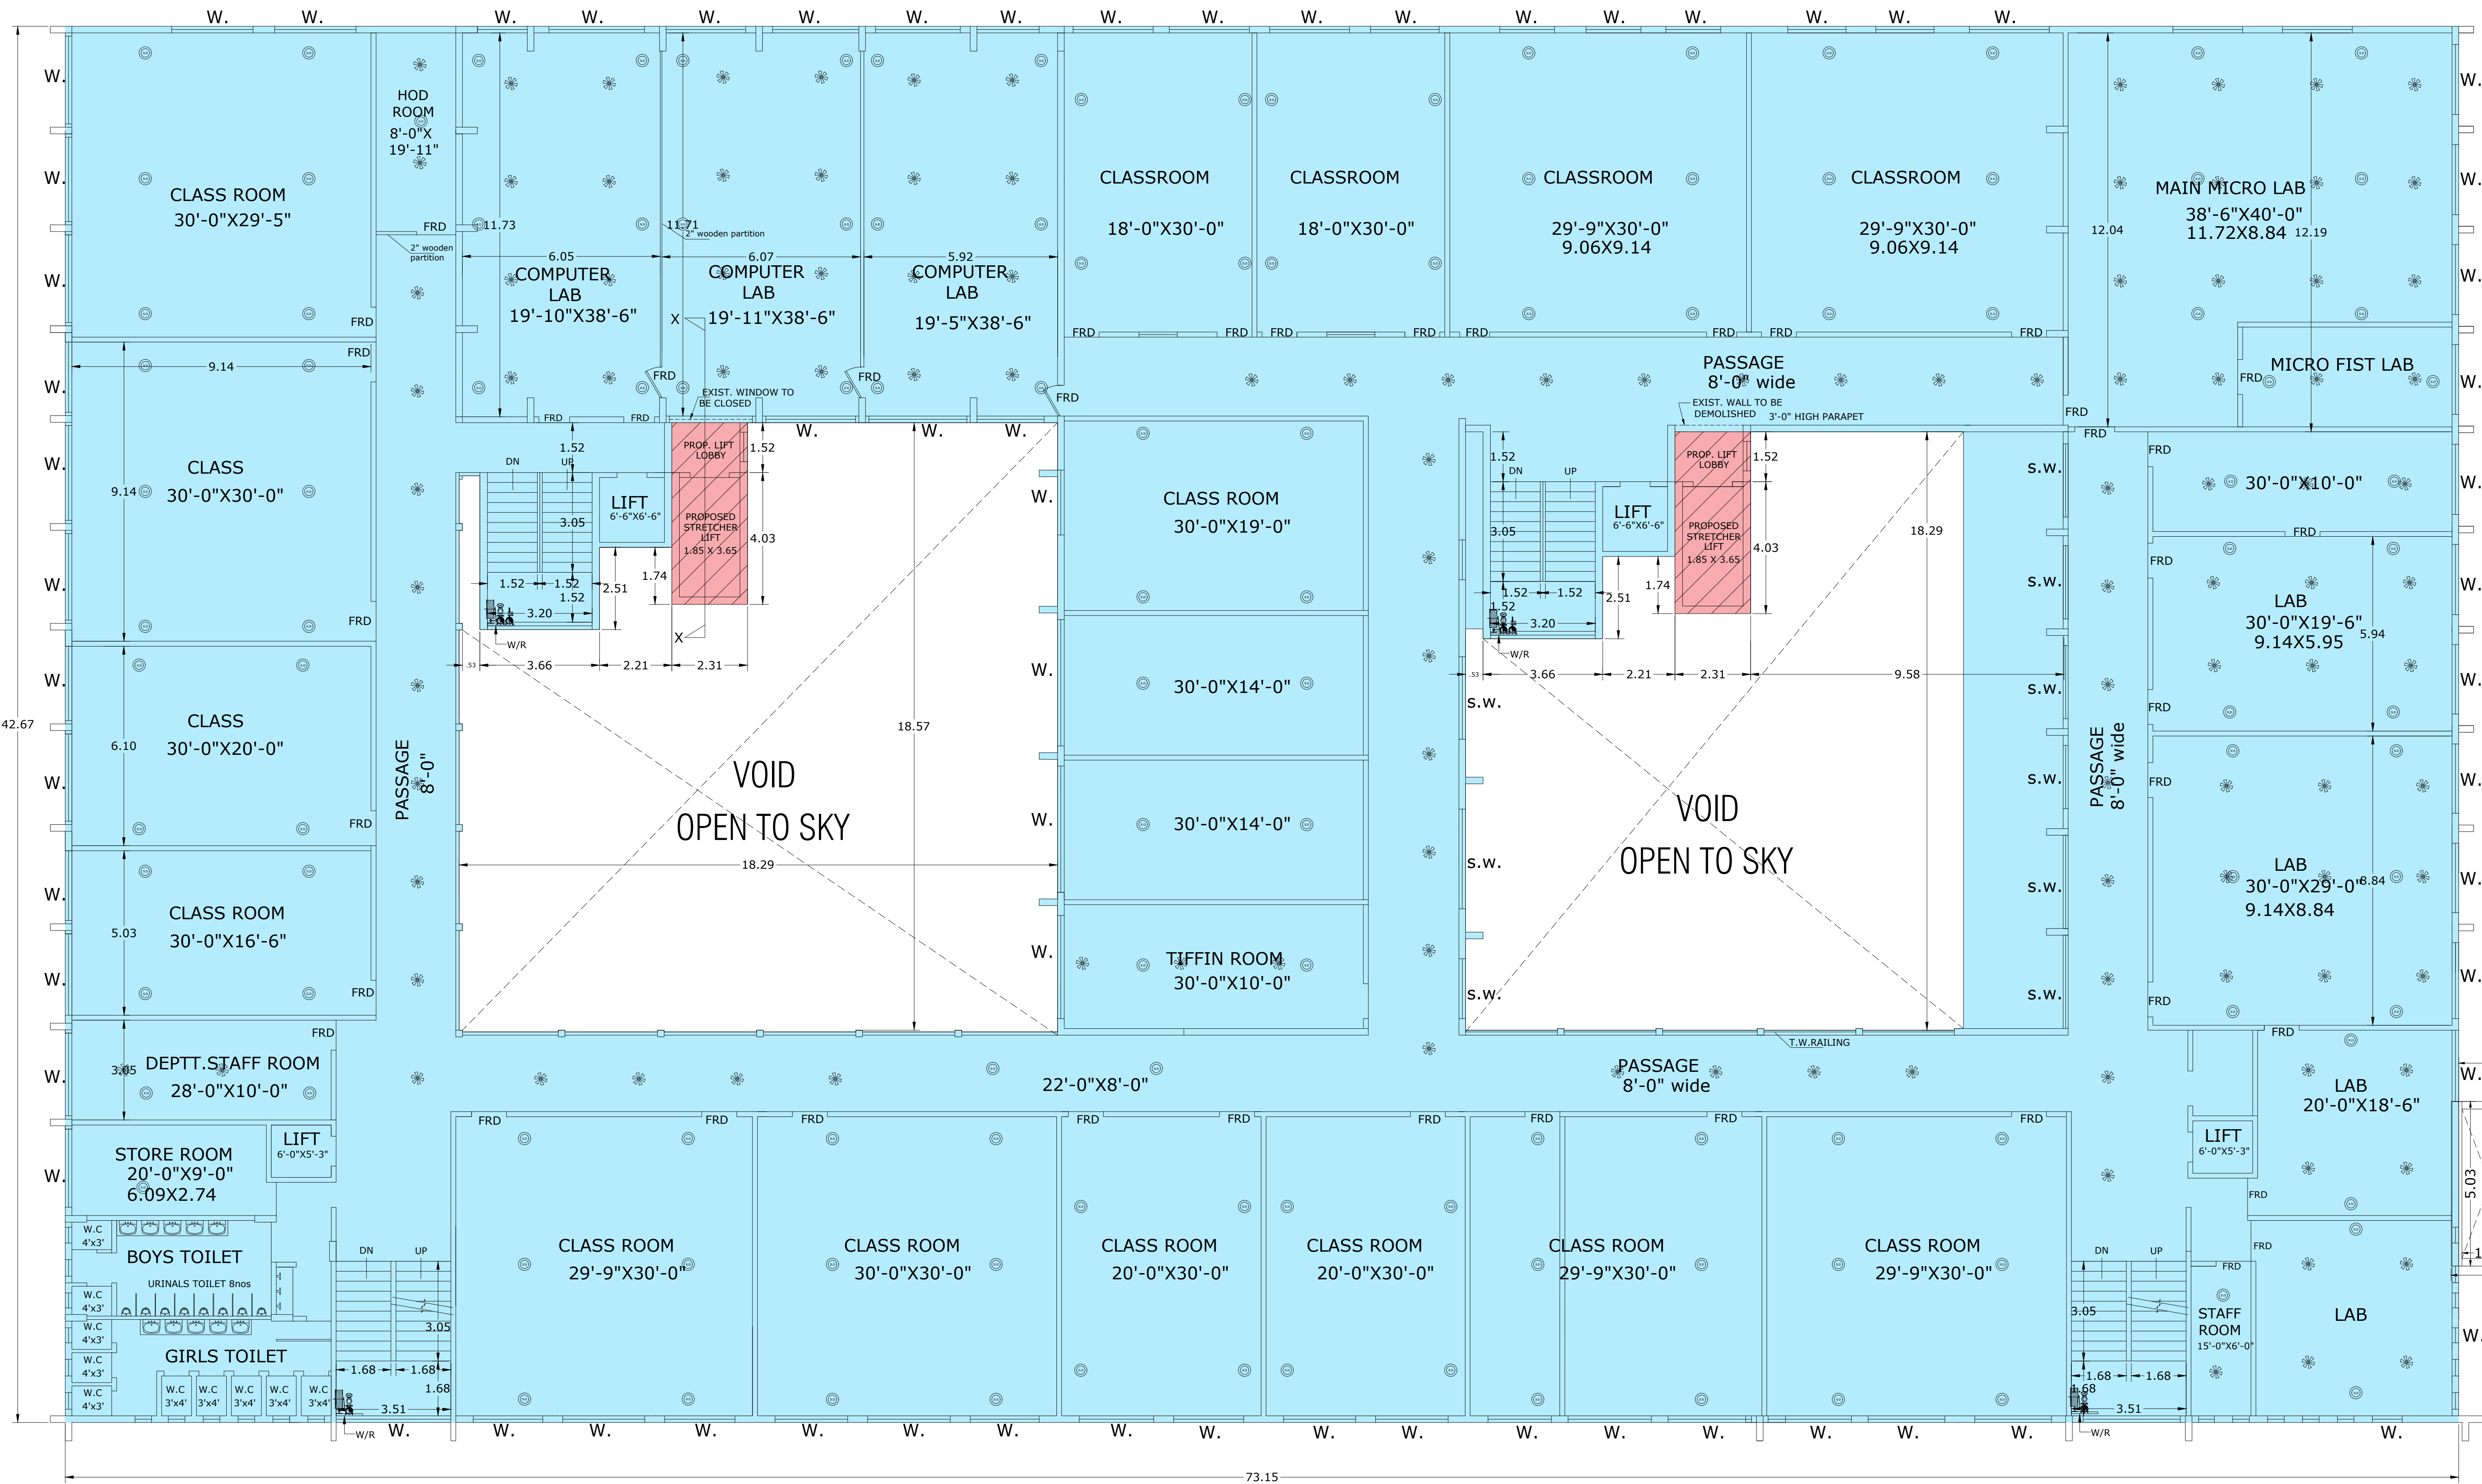


EXISTING THIRD FLOOR PLAN
SCALE : 1:100


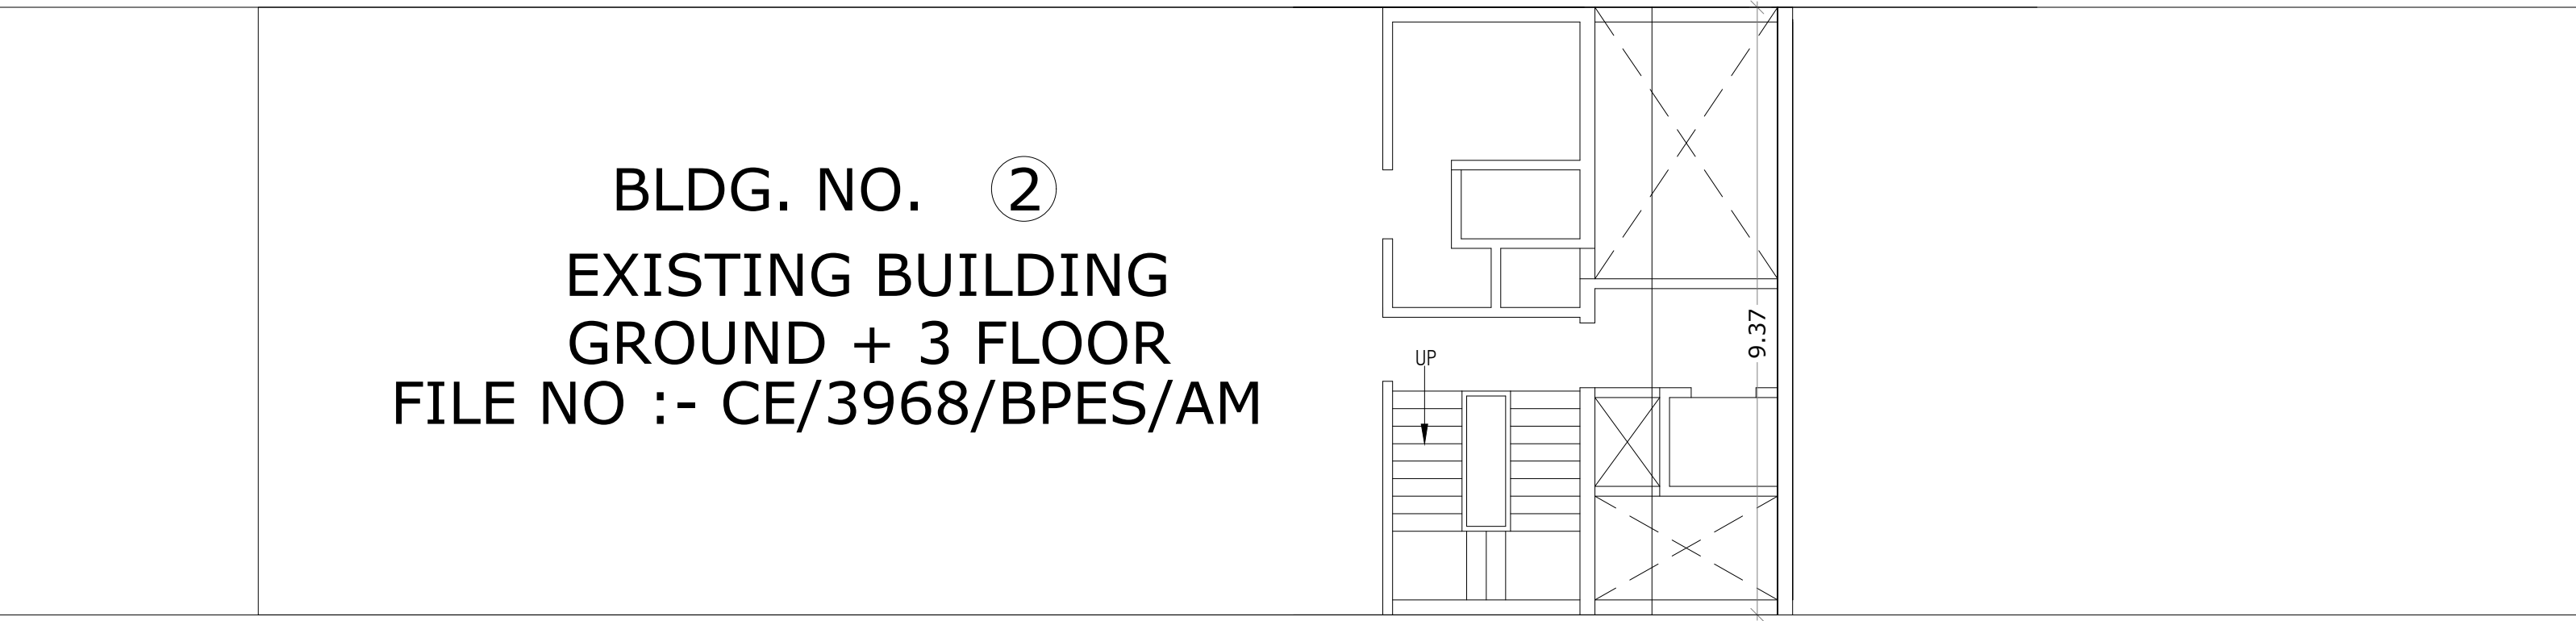


THIRD FLOOR PLAN
SCALE :- 1:100


SANCTIONING AUTHORITY		5/8
STAMP OF RECEIPTS OF PLANS		
APPROVED SUBJECT TO CONDITIONS MENTIONED IN THIS OFFICE LETTER ISSUED U.No. P-24534/2024/(128 A/1 and 128 A Part)/M/E Ward/CHEMBUR-E		
E.E.(B.P.)ES-I		
S.E.(B.P.)M-II	A.E.(B.P.)M	
PROFORMA - B		
CONTENTS OF THE SHEET		
THIRD FLOOR PLAN		
DESCRIPTION OF PROPOSAL & PROPERTY		
PLAN SHOWING PROPOSED STRETCHER LIFT FOR EXISTING VES ARTS SCIENCE COMMERCE & POLYTECHNIC COLLEGE BUILDING AT PLOT C.T.S. NO. 128 A/1 & 128 - A (PT.) OF VILLAGE CHEMBUR, MUMBAI - 400 071		
NAME OF OWNER/APPLICANT	SIGNATURE	
VIVEKANAND EDUCATION SOCIETY		
NAME ADDRESS AND SIGNATURE OF ARCHITECT		
M/S B.H. WADHWA & CO.		
(ARCHITECT & ENGINEERS) A-1,SHUBASHA BUHGALOW, C.T.S. NO. 1210, OFF 10TH ROAD BEHIND JAIN TEMPLE, CHEMBUR, MUMBAI-71		
Bansi Hassana nd Wadhwa		Registration Number: 1000

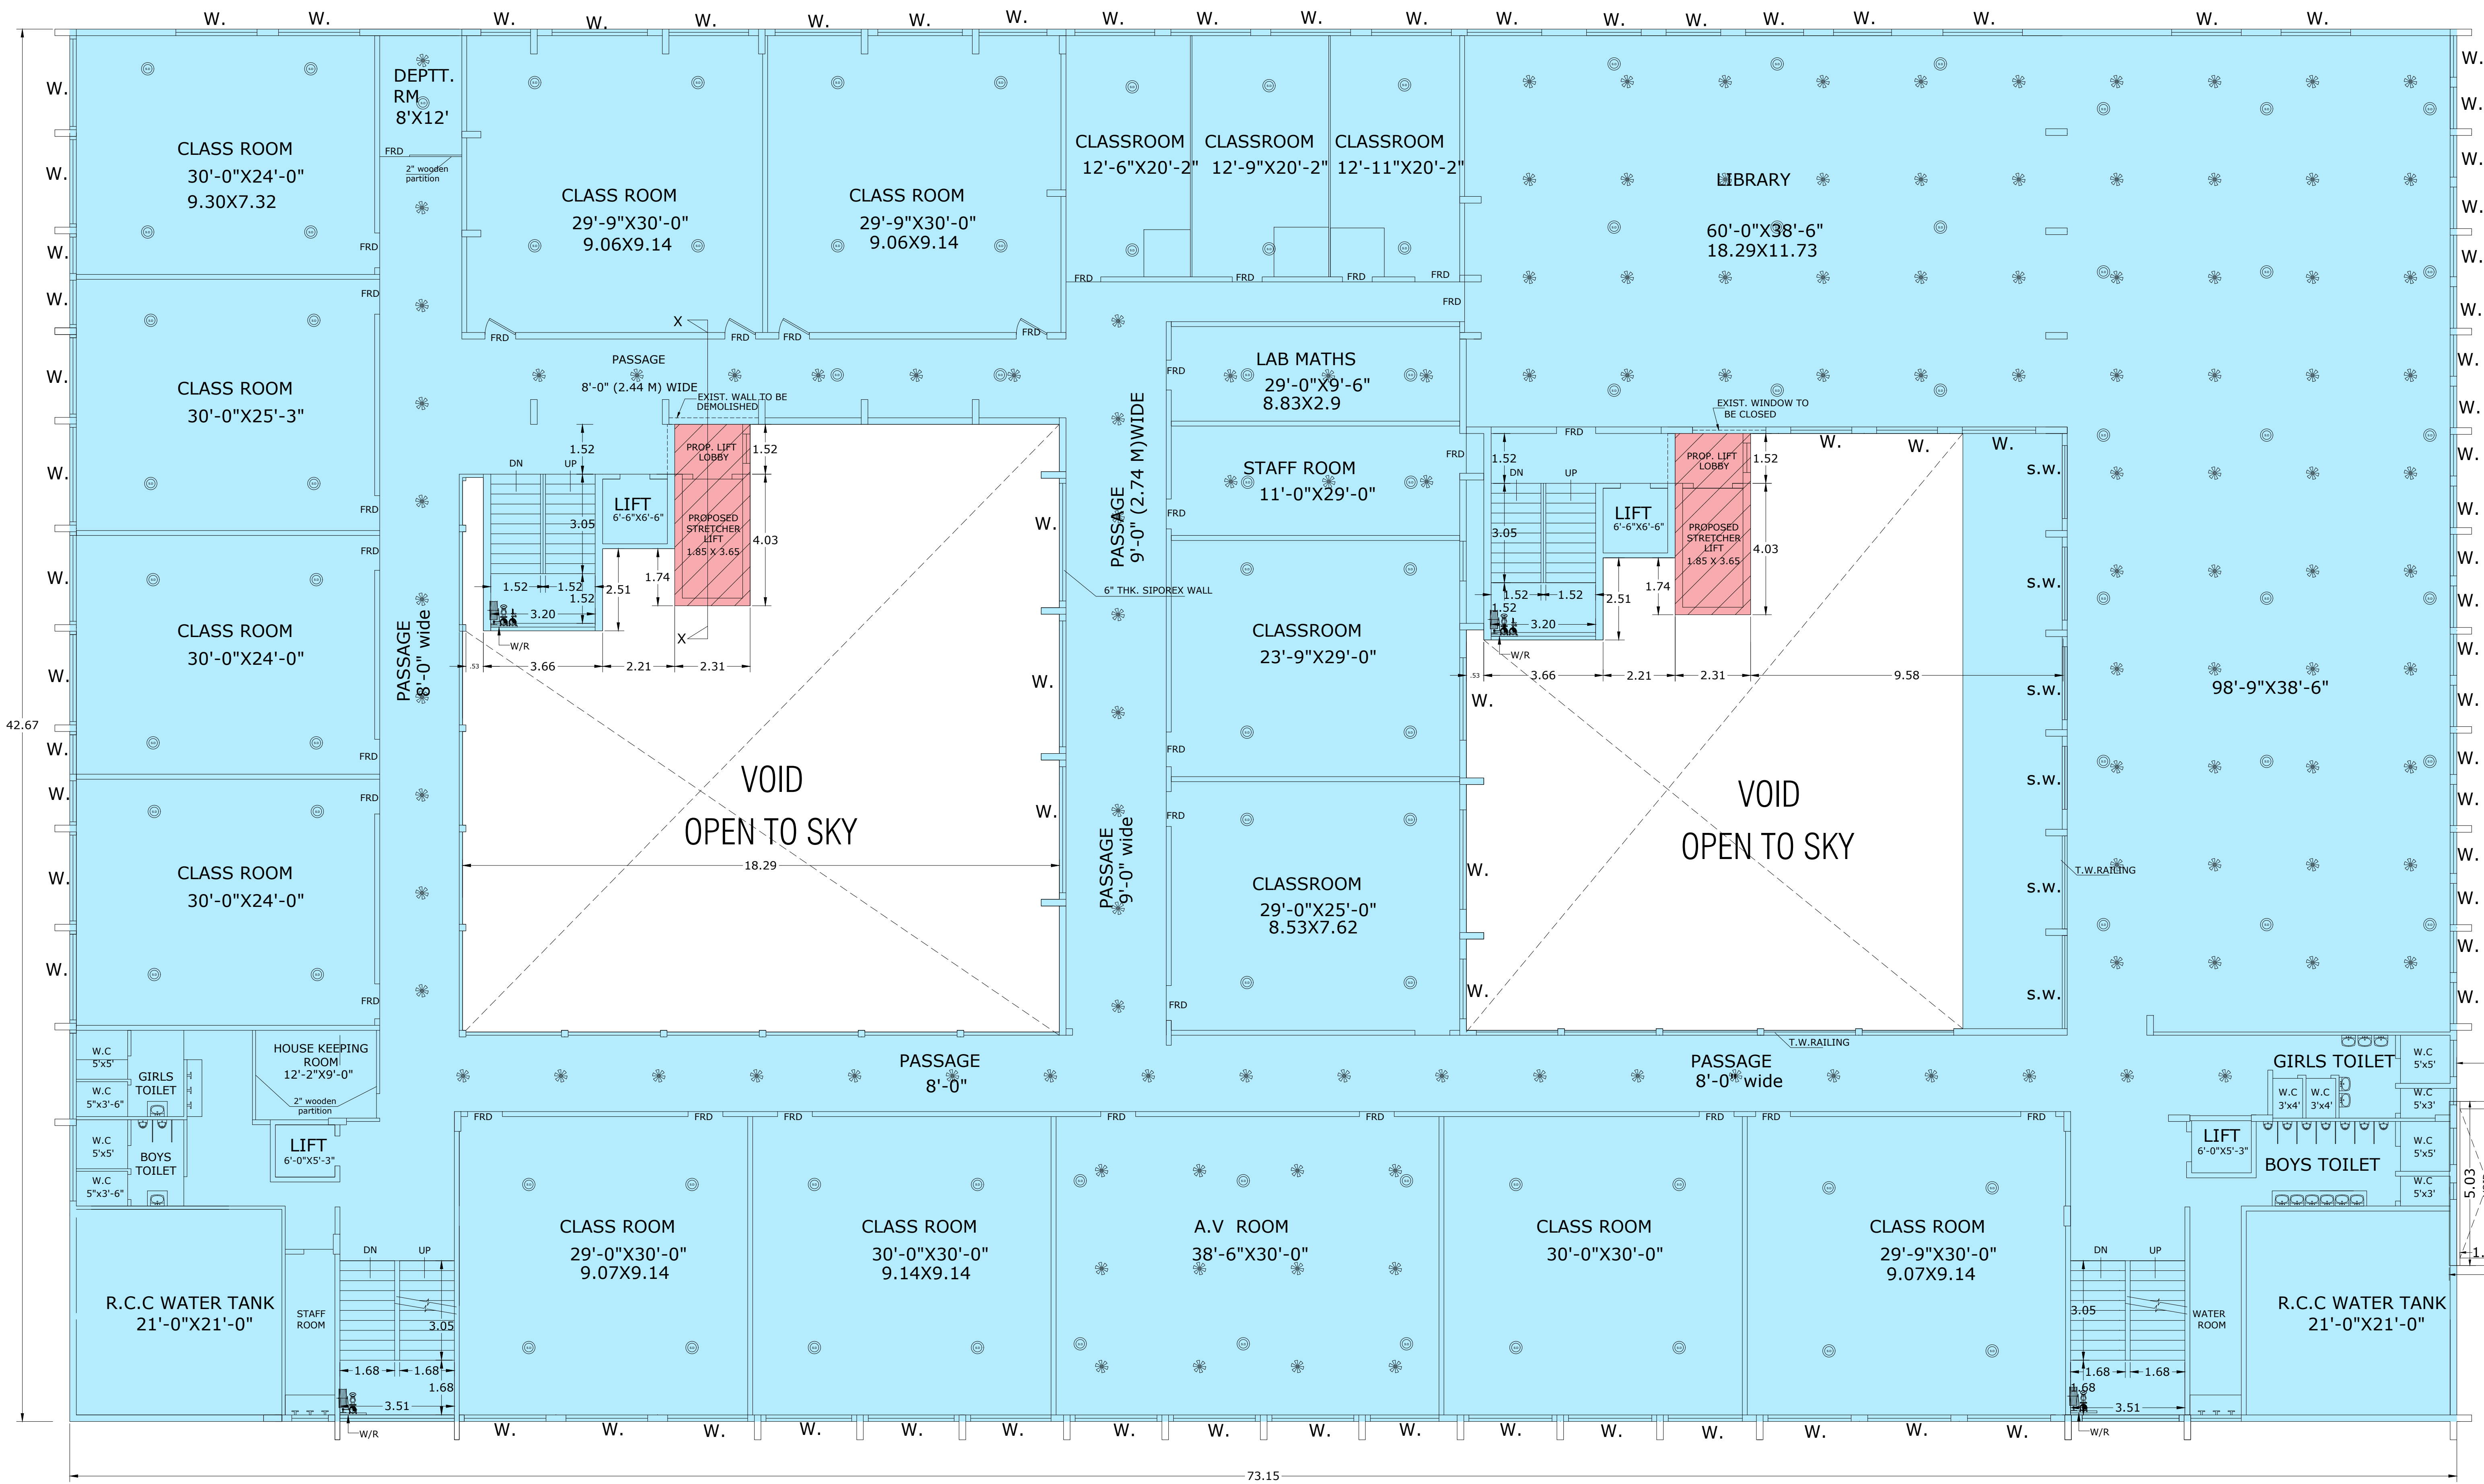



EXISTING FOURTH FLOOR PLAN
SCALE : 1:100

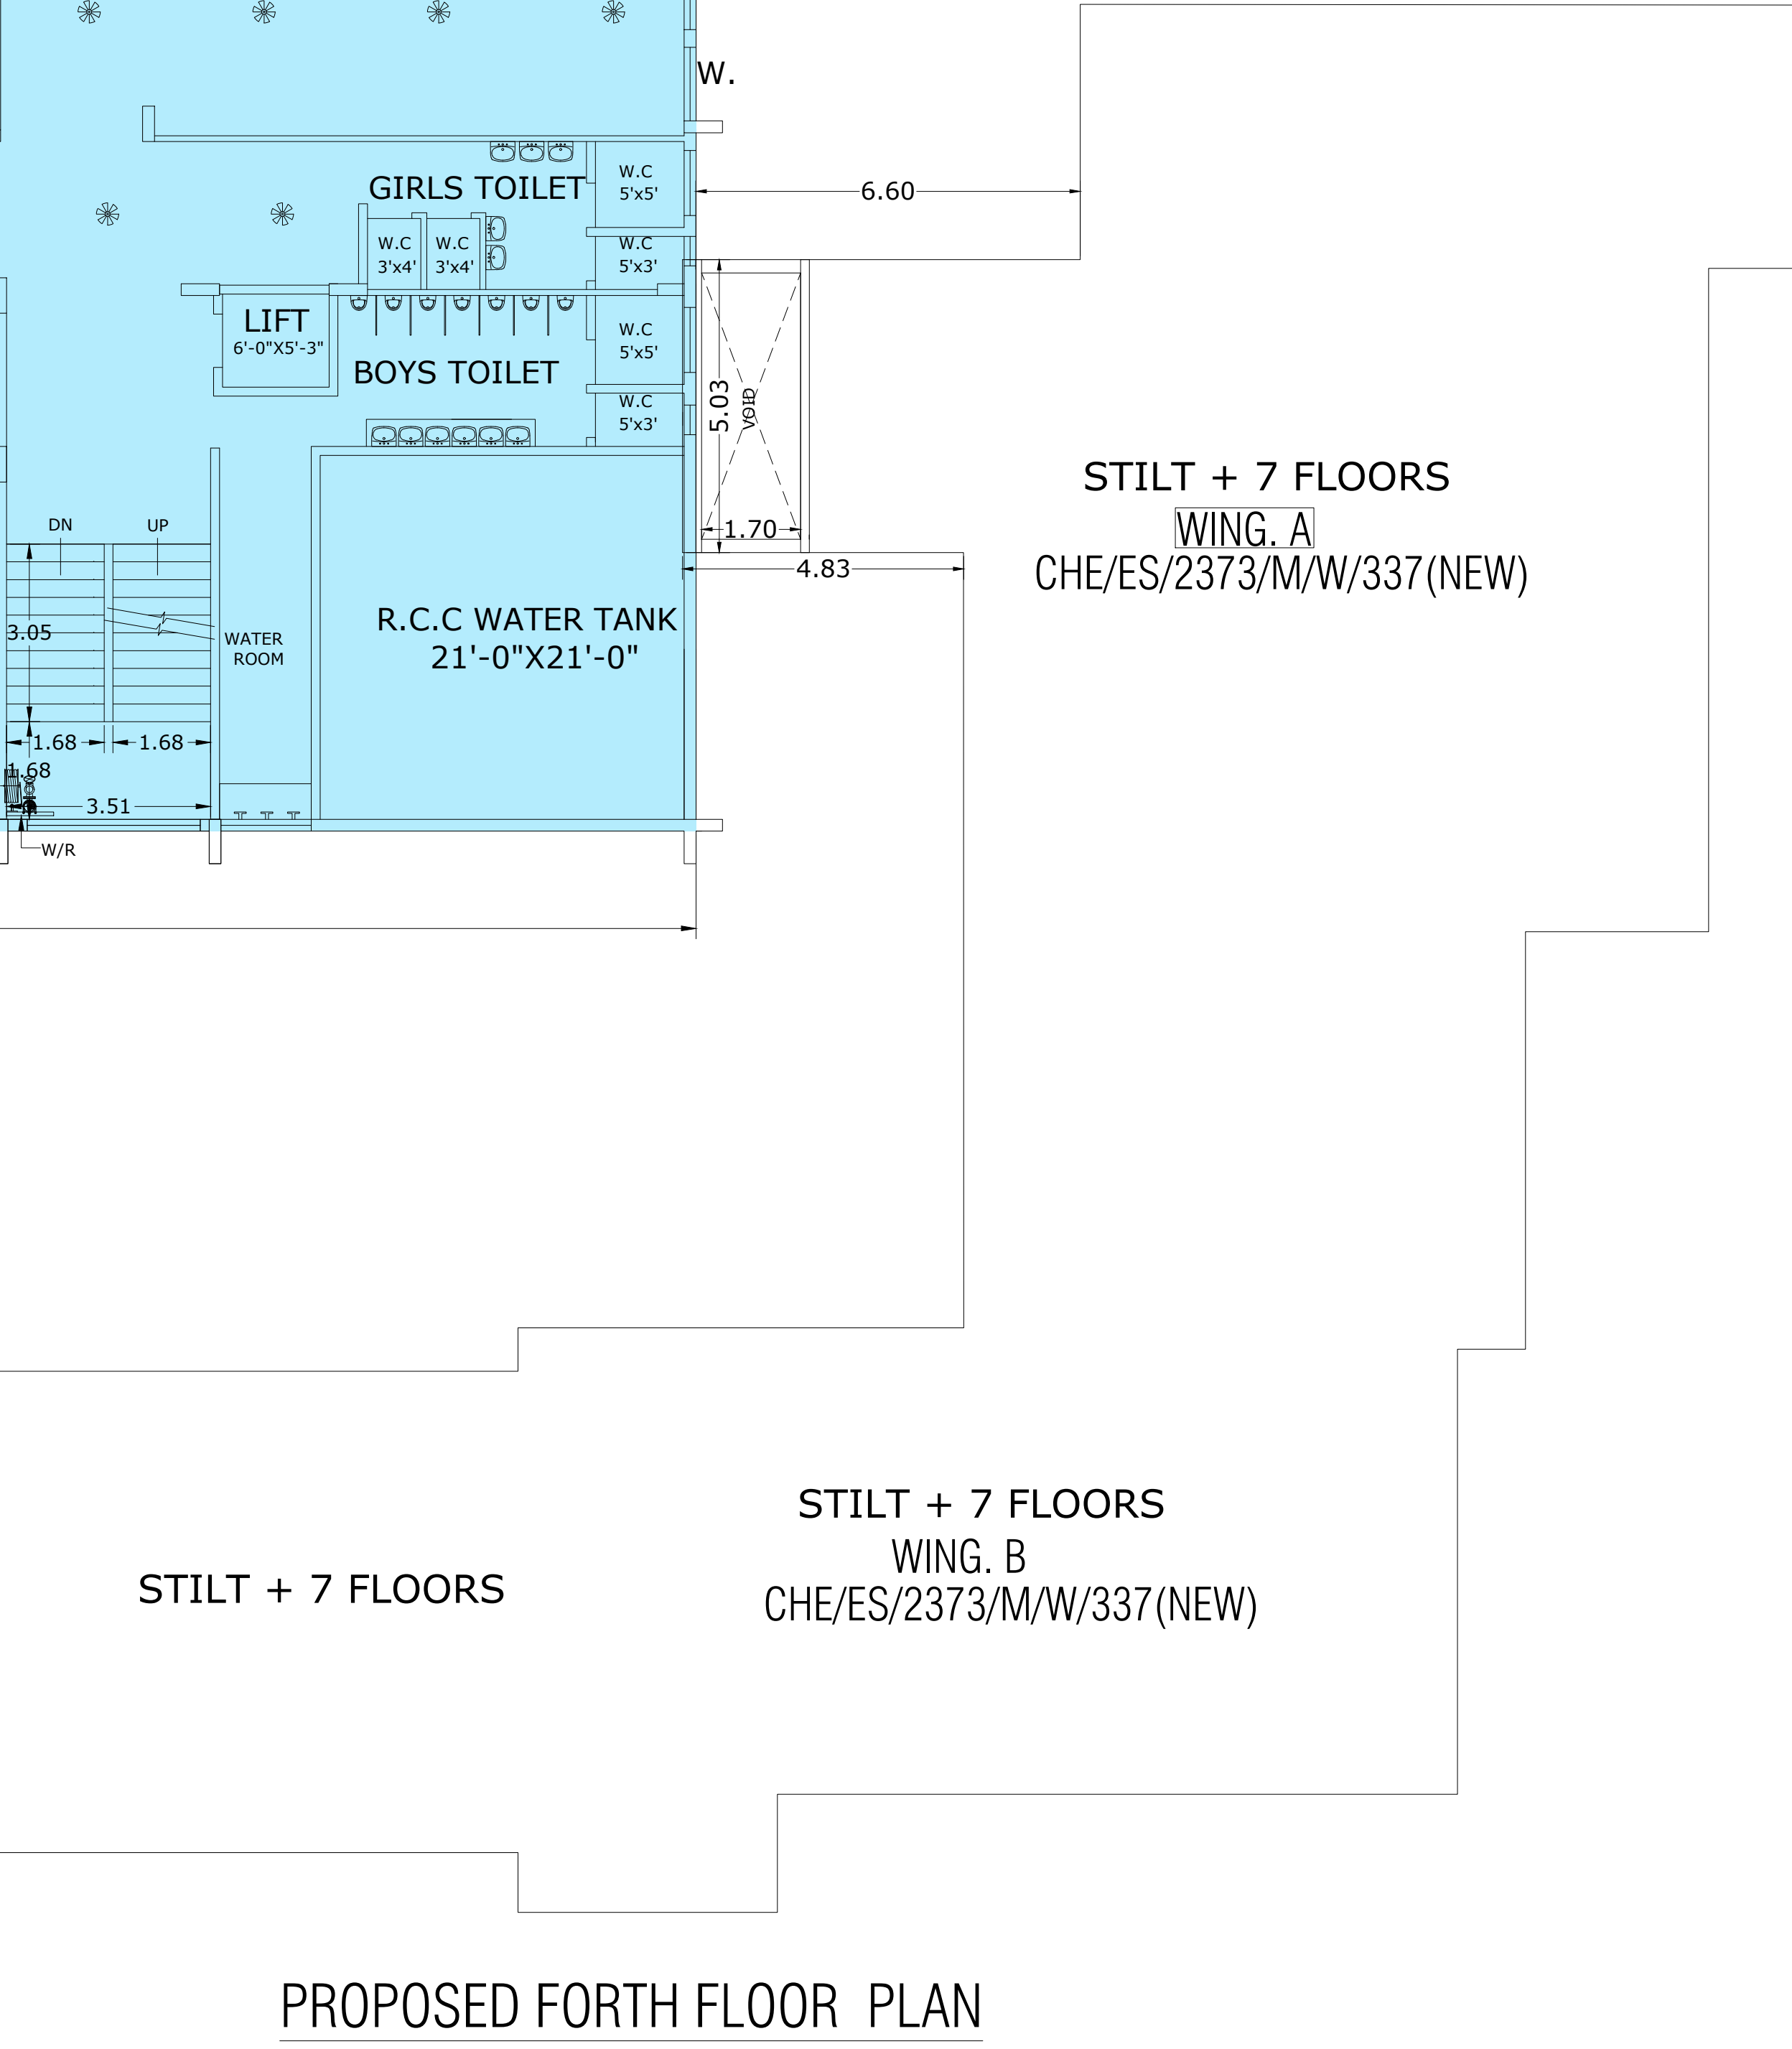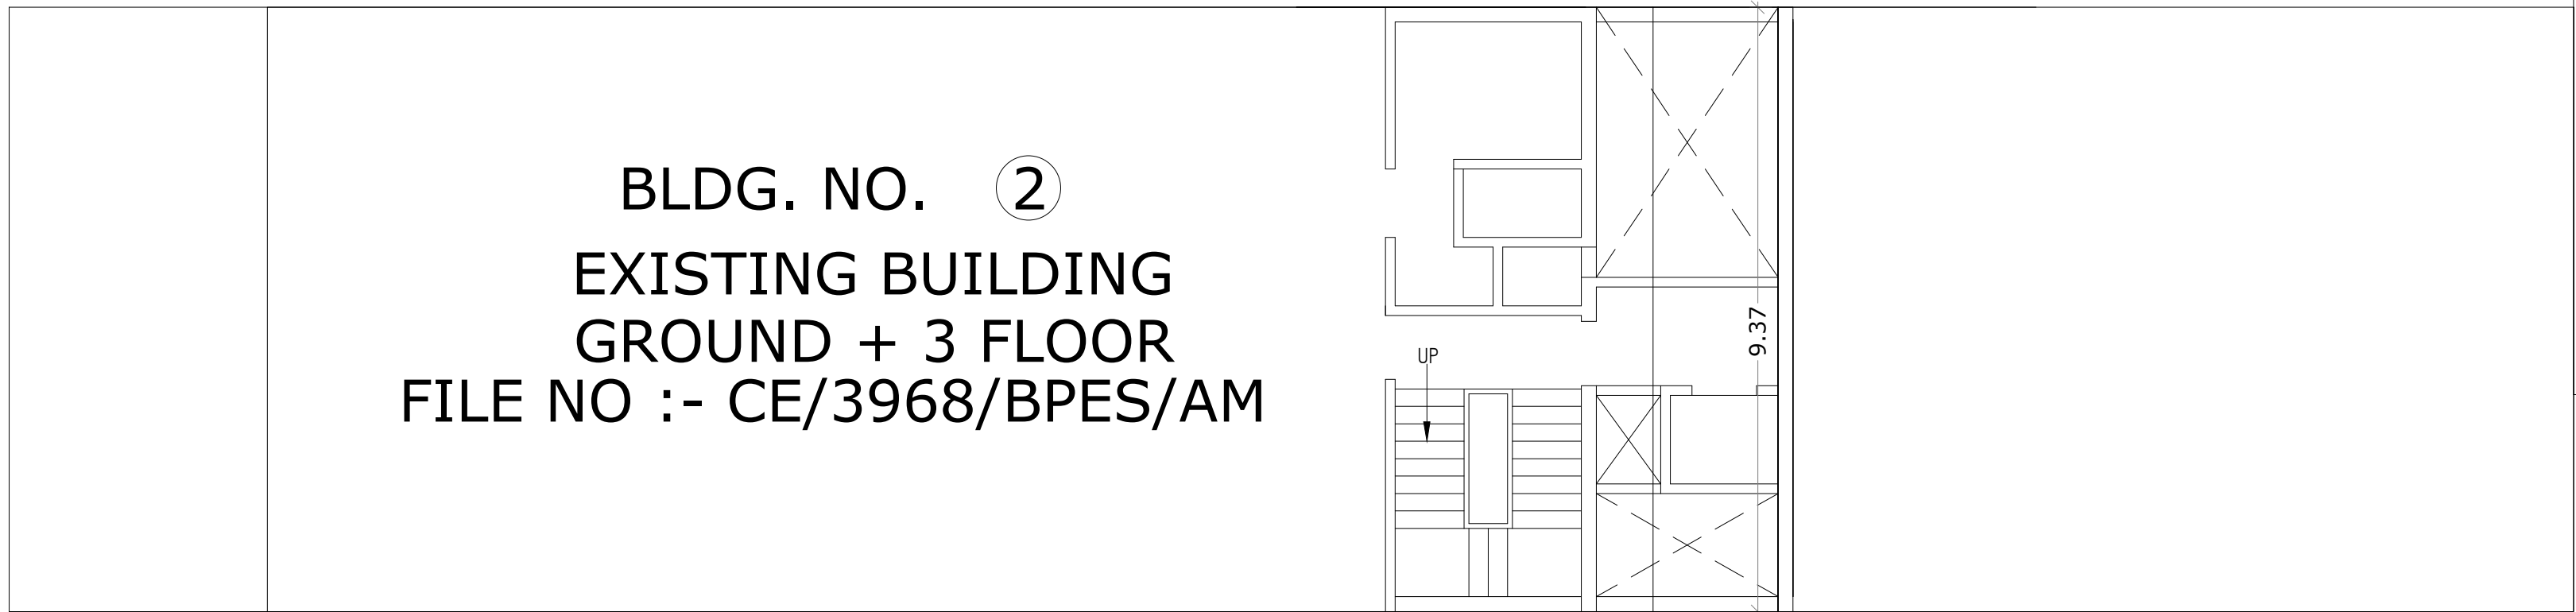


SANCTIONING AUTHORITY		6/8
STAMP OF RECEIPTS OF PLANS		
APPROVED SUBJECT TO CONDITIONS MENTIONED IN THIS OFFICE LETTER ISSUED U.No. P-24534/2024/(128 A/1 and 128 A Part Y)/M/E Ward/CHEMBUR-E		
E.E.(B.P.)ES-I		
S.E.(B.P.)M-II	A.E.(B.P.)M	
PROFORMA - B		
CONTENTS OF THE SHEET		
FOURTH FLOOR PLAN		
DESCRIPTION OF PROPOSAL & PROPERTY		
PLAN SHOWING PROPOSED STRETCHER LIFT FOR EXISTING VES ARTS SCIENCE COMMERCE & POLYTECHNIC COLLEGE BUILDING AT PLOT C.T.S. NO. 128 A/1 & 128 - A (PT.) OF VILLAGE CHEMBUR, MUMBAI - 400 071		
NAME OF OWNER/APPLICANT	SIGNATURE	
VIVEKANAND EDUCATION SOCIETY		
NAME ADDRESS AND SIGNATURE OF ARCHITECT		
M/S B.H. WADHWA & CO.		
(ARCHITECT & ENGINEERS)		
A-1,SHUBASHA BUH GALOW, C.T.S. NO. 1210, OFF 10TH ROAD BEHIND JAIN TEMPLE, CHEMBUR, MUMBAI-71		
Bansi Hassana nd Wadhwa (B.H. WADHWA)		

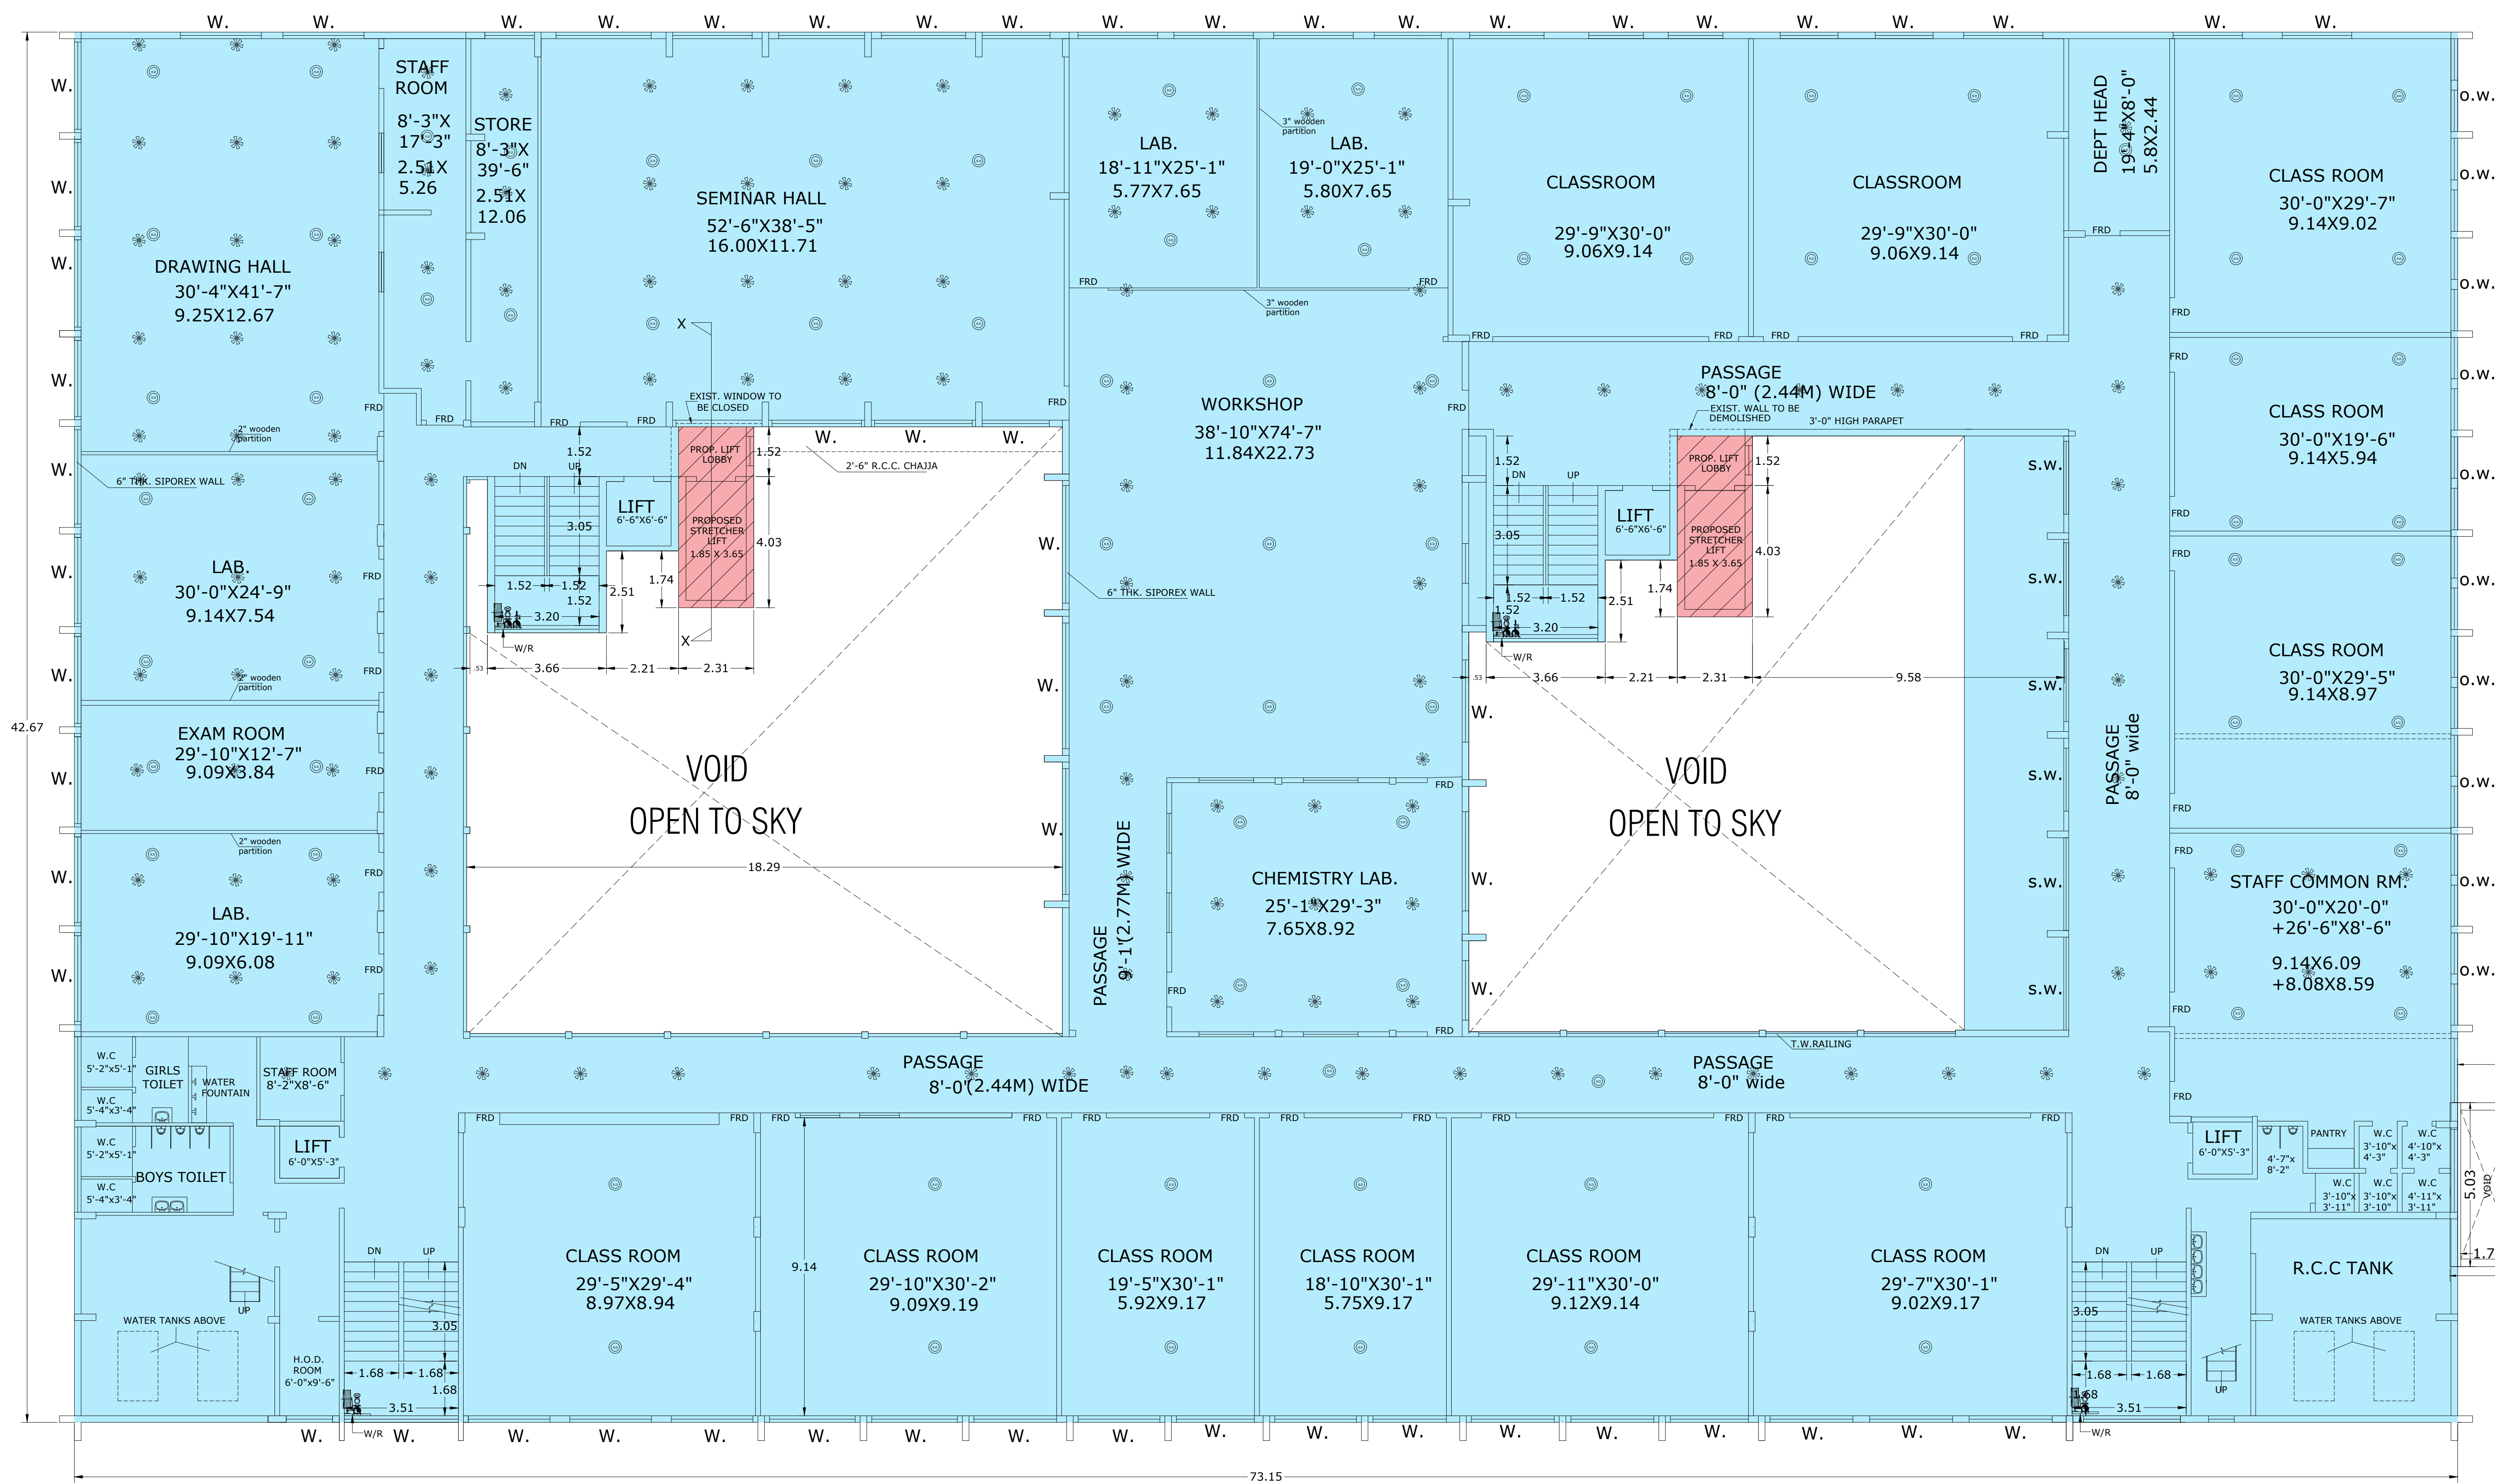


EXISTING FIFTH FLOOR PLAN
SCALE : 1:100

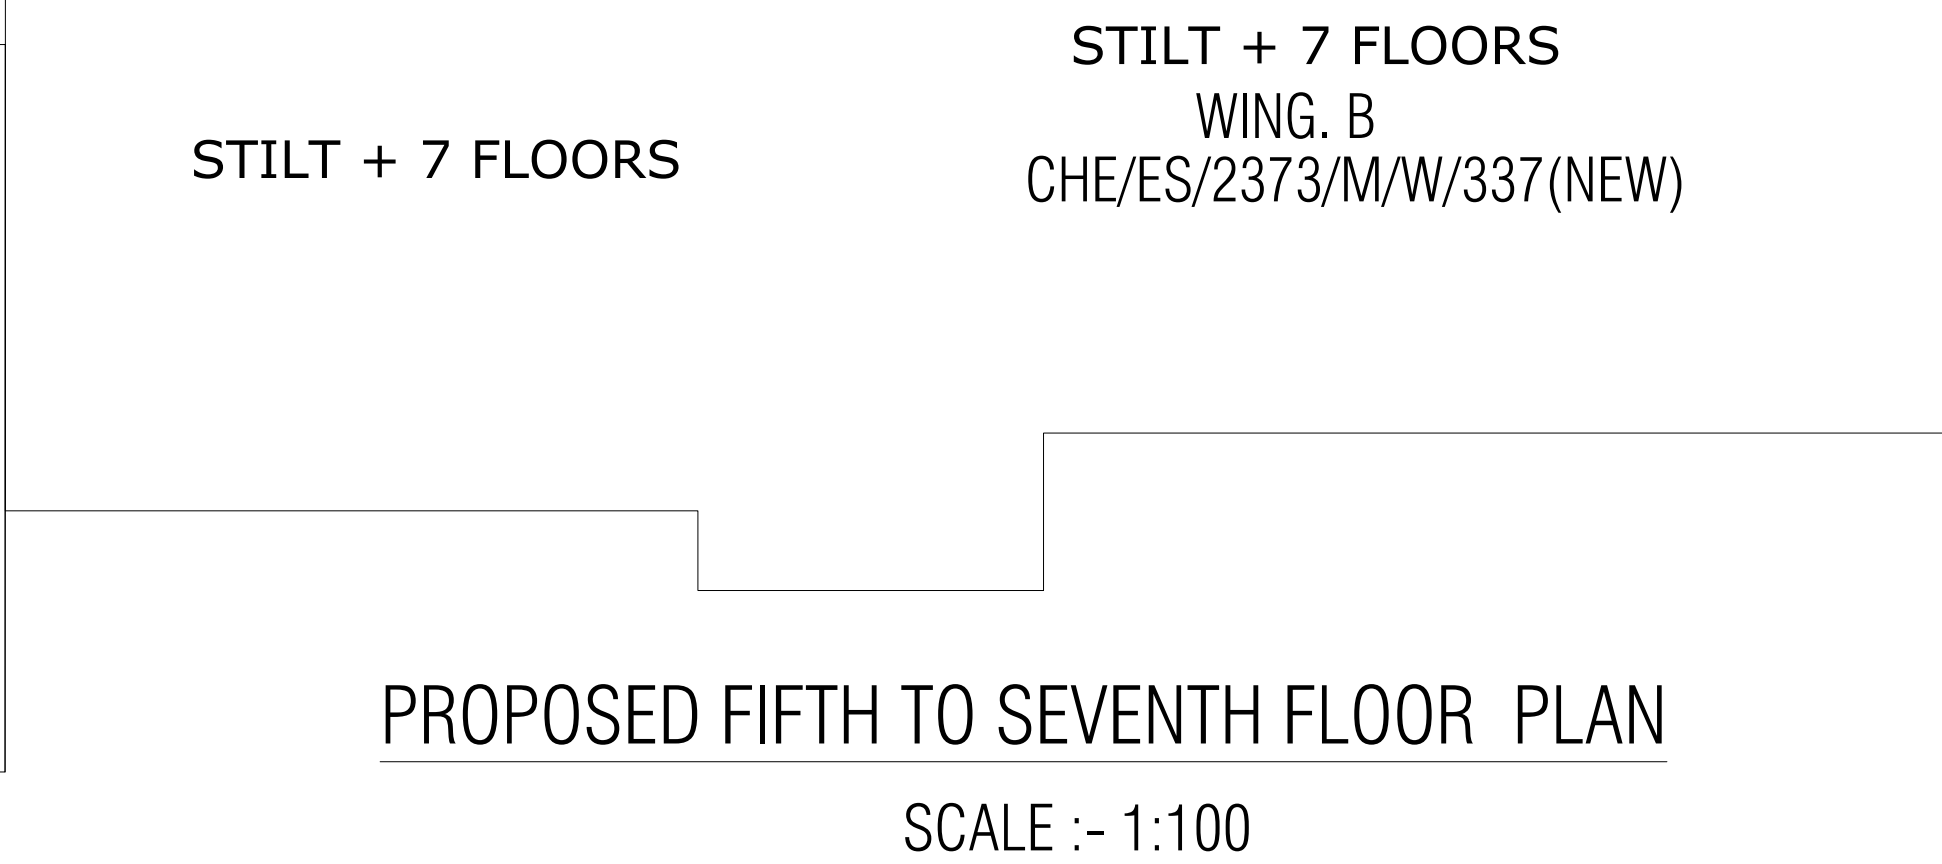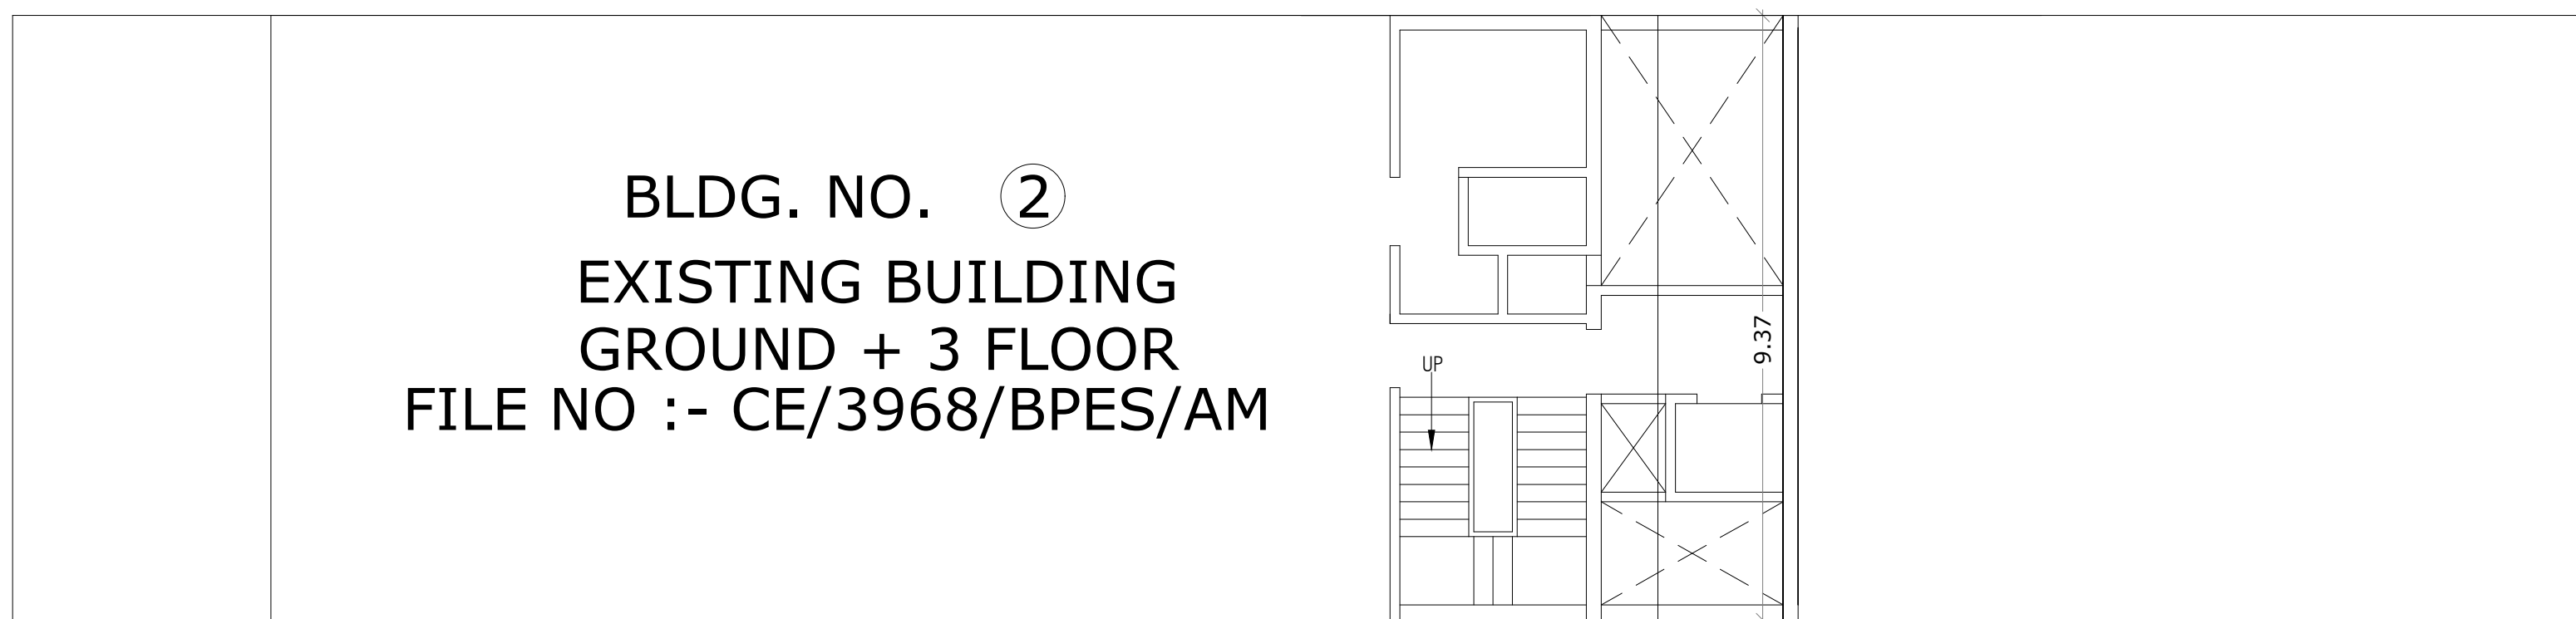

SANCTIONING AUTHORITY		7/8
STAMP OF RECEIPTS OF PLANS		
APPROVED SUBJECT TO CONDITIONS MENTIONED IN THIS OFFICE LETTER ISSUED U.No. P-24534/2024/(128 A/1 and 128 A Part)/M/E Ward/CHEMBUR-E		
E.E.(B.P.)ES-I		
S.E.(B.P.)M-II	A.E.(B.P.)M	
PROFORMA - B		
CONTENTS OF THE SHEET		
FIFTH FLOOR PLAN		
DESCRIPTION OF PROPOSAL & PROPERTY		
PLAN SHOWING PROPOSED STRETCHER LIFT FOR EXISTING VES ARTS SCIENCE COMMERCE & POLYTECHNIC COLLEGE. BUILDING AT PLOT C.T.S. NO. 128 A/1 & 128 - A (PT.) OF VILLAGE CHEMBUR, MUMBAI - 400 071		
NAME OF OWNER/APPLICANT	SIGNATURE	
VIVEKANAND EDUCATION SOCIETY		
NAME ADDRESS AND SIGNATURE OF ARCHITECT		
M/S B.H. WADHWA & CO.		
(ARCHITECT & ENGINEERS)		
A-1,SHUBASHA BHUGALOW,		
C.T.S. NO. 1210, OFF 10TH ROAD		
BEHIND JAIN TEMPLE,		
CHEMBUR, MUMBAI-71		
		Bansi Hassana nd Wadhwa (B.H. WADHWA)

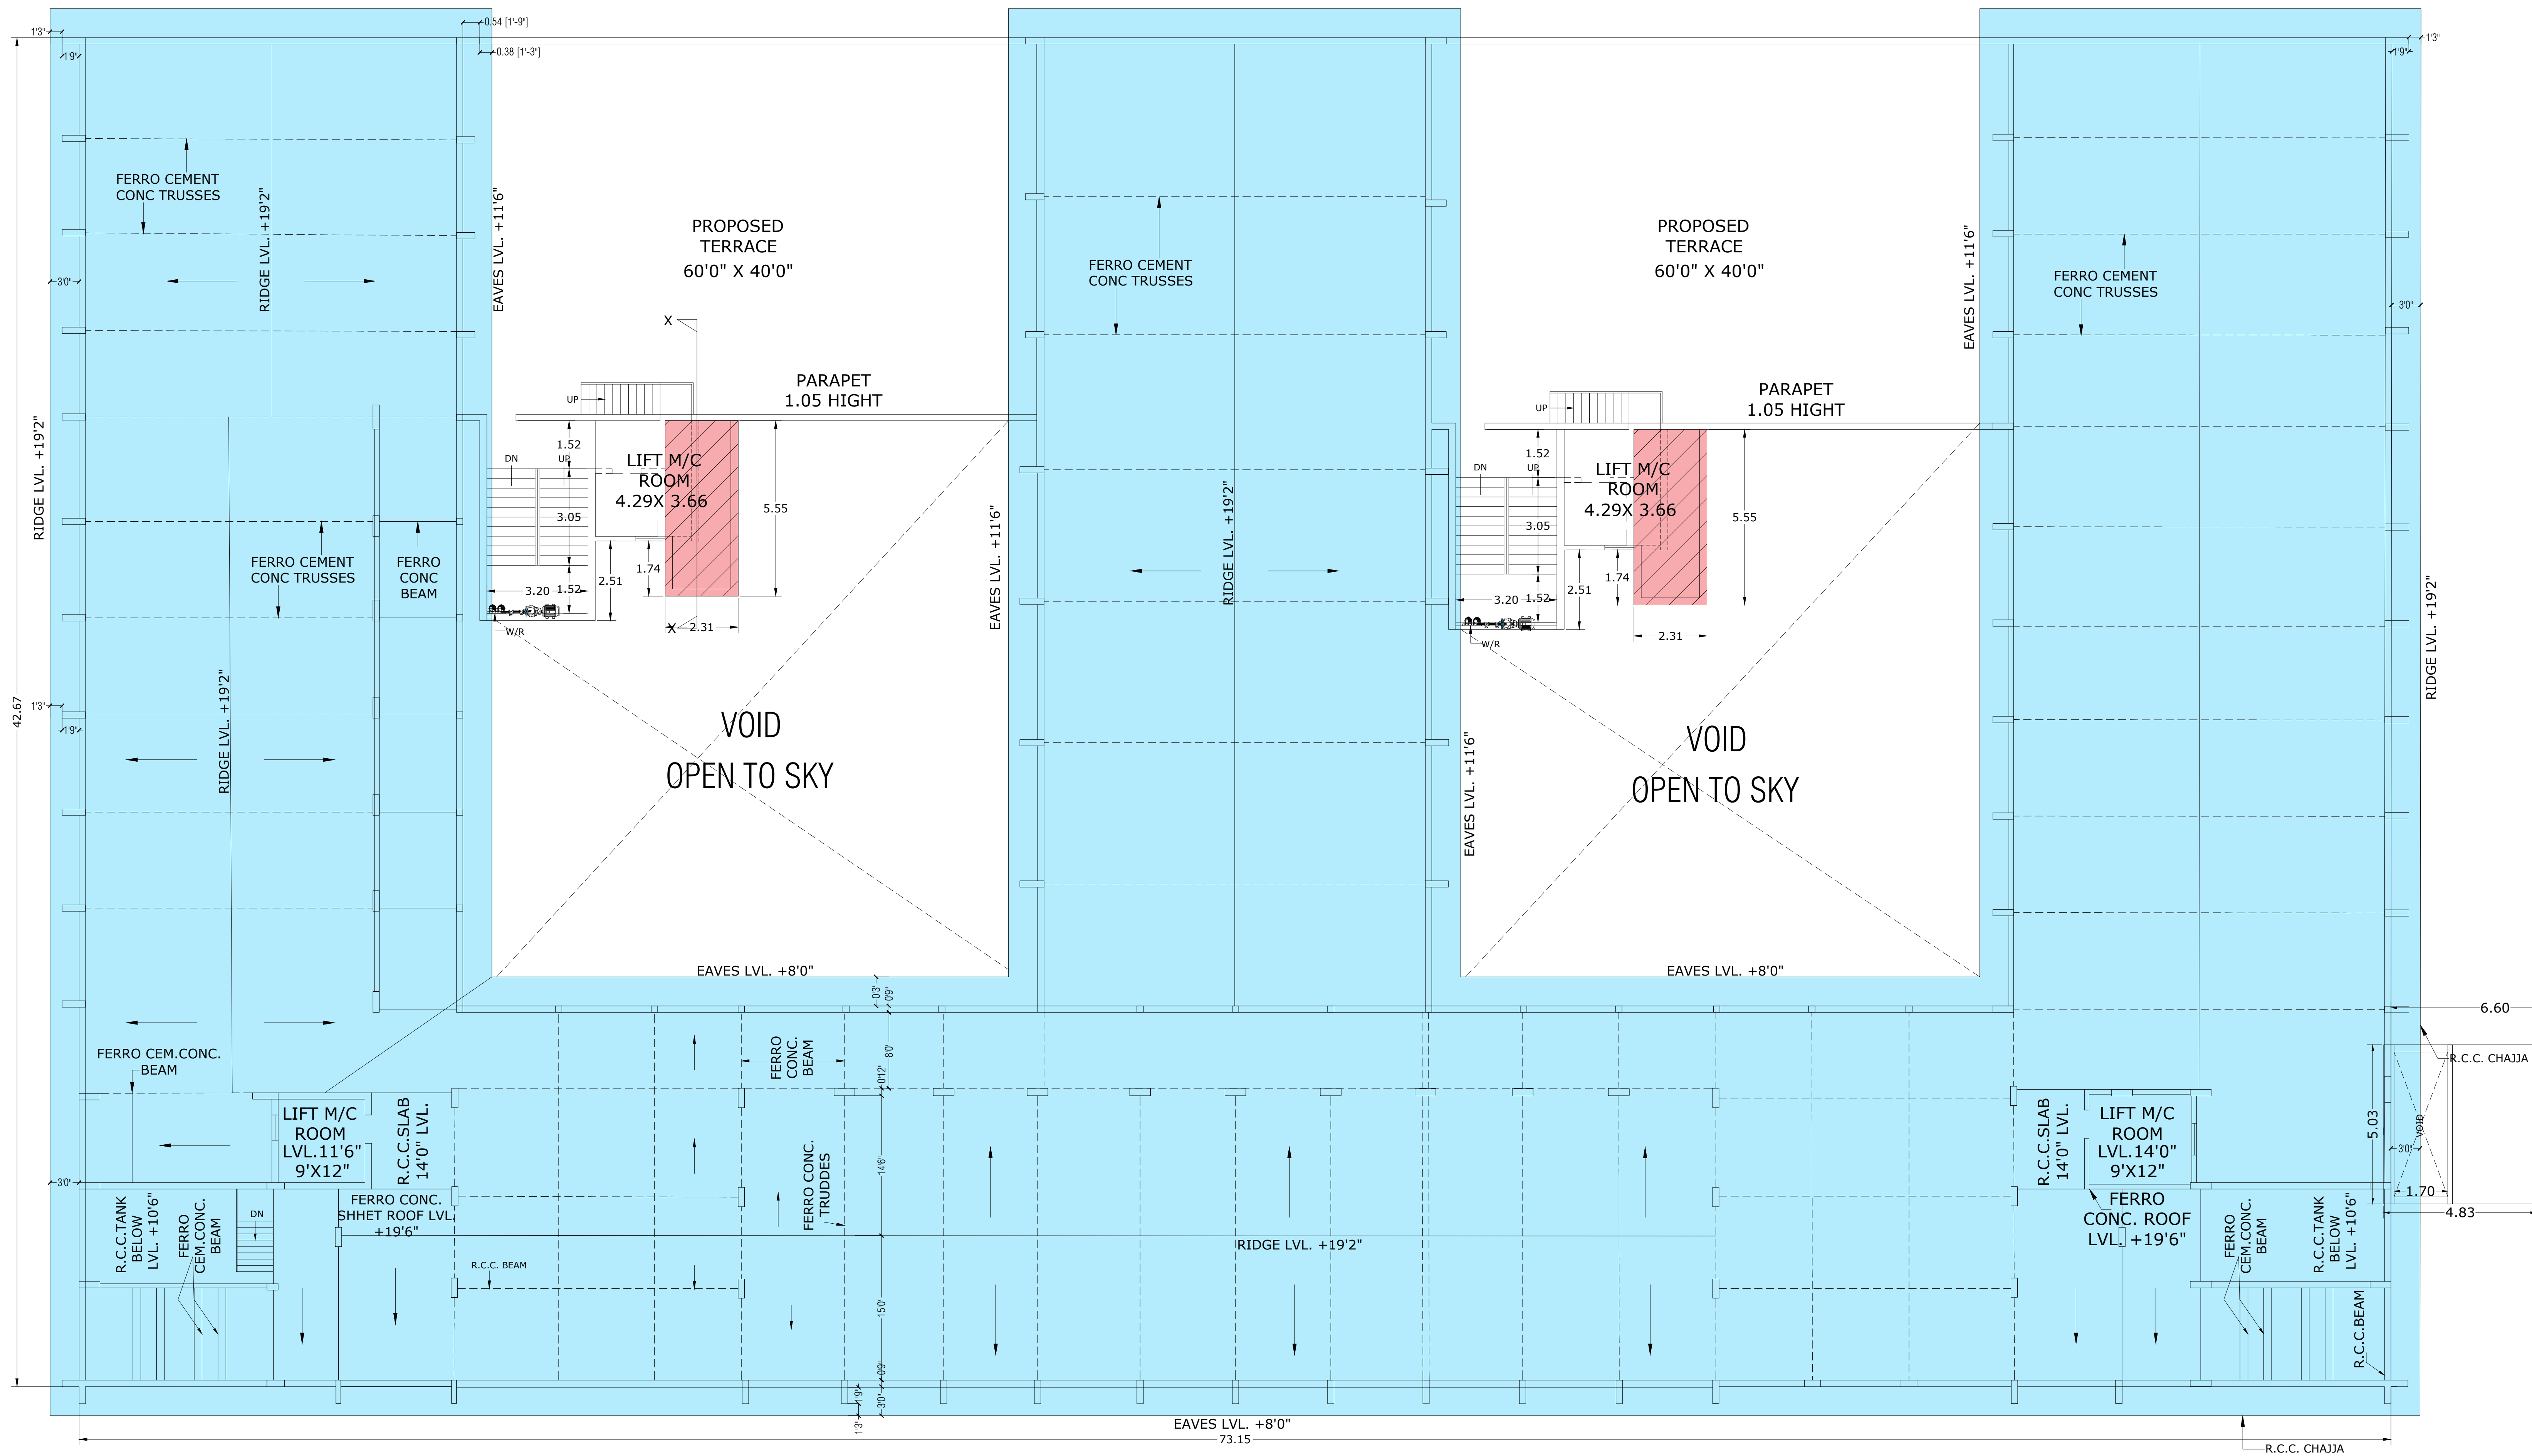

EXISTING ROOF FLOOR PLAN
SCALE : 1:100

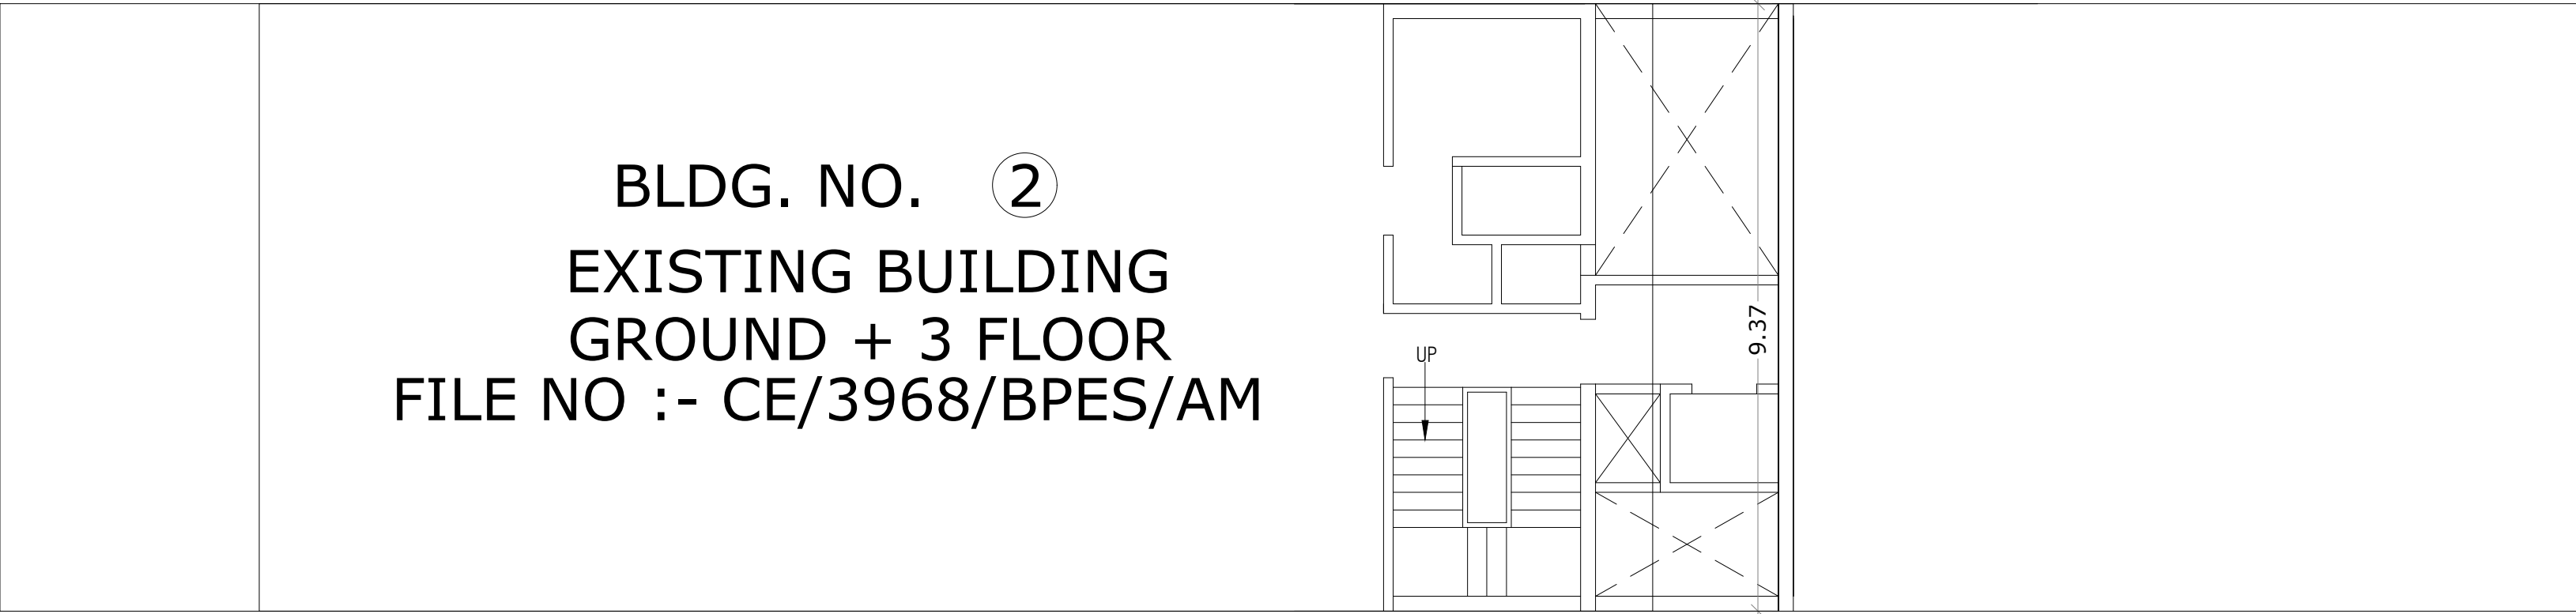

PROPOSED TERRACE FLOOR PLAN
SCALE :- 1:100

SANCTIONING AUTHORITY		8/8
STAMP OF RECEIPTS OF PLANS		
APPROVED SUBJECT TO CONDITIONS MENTIONED IN THIS OFFICE LETTER ISSUED U.No. P-24534/2024/(128 A/1 and 128 A Part)/M/E Ward/CHEMBUR-E		
E.E.(B.P.)ES-I		
S.E.(B.P.)M-II	A.E.(B.P.)M	
PROFORMA - B		
CONTENTS OF THE SHEET		
ROOF FLOOR PLAN		
DESCRIPTION OF PROPOSAL & PROPERTY		
PLAN SHOWING PROPOSED STRETCHER LIFT FOR EXISTING VES ARTS SCIENCE COMMERCE & POLYTECHNIC COLLEGE BUILDING AT PLOT C.T.S. NO. 128 A/1 & 128 - A (PT.) OF VILLAGE CHEMBUR, MUMBAI - 400 071		
NAME OF OWNER/APPLICANT	SIGNATURE	
VIVEKANAND EDUCATION SOCIETY		
NAME ADDRESS AND SIGNATURE OF ARCHITECT		
M/S B.H. WADHWA & CO.		
(ARCHITECT & ENGINEERS) A-1,SHUBASHA BUHGALOW, C.T.S. NO. 1210, OFF 10TH ROAD BEHIND JAIN TEMPLE, CHEMBUR, MUMBAI-71		
Bansi Hassana nd Wadhw a (B.H. WADHWA)		

A

STILT + 7 FLOORS
WING. A
CHE/ES/2373/M/W/337(NEW)

STILT + 7 FLOORS

STILT + 7 FLOORS
WING. B
CHE/ES/2373/M/W/337(NEW)

BLDG. NO. ②
EXISTING BUILDING
GROUND + 3 FLOOR
FILE NO :- CE/3968/BPES/AM