

AREA STATEMENT		SQ.MTS.
1	Area of Plot (as per P. R. card)	686.00
a)	Area of Reservation in plot	---
b)	i) Area of Road Set back (Already merged)	---
c)	ii) Area of Road Set back	---
2	Area of D. P. Road	---
Deductions for :		---
A) For Reservation		---
a)	Set-back area as per DCR 16	---
b)	DP road area as per DCR 16	---
c)	Enroachment area	---
Total of 2(A)		---
B) For Amenity Area		---
A	Area of amenity as per DCR 14 (A)	---
B	Area of 5% amenity	---
C	Area of amenity as per DCR 15	---
D	Area of amenity as per DCR 35	---
Total of 2(B)		---
C) Deduction for existing BUA to be retained		---
A	Land component of the same	---
Total of 2(C)		---
3	Total deduction : [2 (A) + 2 (B) + 2 (C)]	---
4	Balance area of plot (1 - 3)	686.00
5	Deduction for 15% R. G.	---
6	Net plot area for development (4)	686.00
7	Built up area equal to area of land handed over as per regulation 30 (A) (--- x 2) = ---	---
8	a Additional Premium FSI	343.00
b	Additional built-up area in the lieu of internal road area as per layout	---
c	Additional built-up area in the lieu of Set-back road area (already merged)	---
d	Built up area due to "Additional F. S. I." as per Regulation No. 33 (7) (B) on remaining / balance plot. (10.00 x --- tenement = --- sq.mt.)	---
9	Permissible TDR	---
i	General	384.16
ii	Slum	96.04
iii	Road	---
10	Permissible BUA (7 + 8 + 9)	1509.20
11	Proposed BUA	1509.20
	Residential Rehab	---
	Residential Sale	---
	Non Residential Rehab	---
	Non Residential Sale	---

CONSTRUCTION AREA STATEMENT


FLOORS	AREA IN SQ. MT.
BASE. FLR.	107.63
GR. FLR.	366.48
1ST FLR.	277.49
2ND FLR.	300.00
3RD FLR.	281.61
4TH FLR.	294.24
5TH FLR.	281.61
6TH FLR.	294.24
7TH FLR.	294.01
8TH FLR.	306.64
L.M.R. O.H.T. & ST. CABIN	60.00
TOTAL	2863.95

BUILT-UP AREA SUMMARY

FLOORS	B. U. AREA (RESIDENTIAL) SQ.MTS (1)	B. U. AREA (COMMERCIAL) SQ.MTS (2)	TOTAL B. U. AREA SQ.MTS (1+2)	STAIRCASE LIFT & LIFT LOBBY AREA
GR. FLR.	---	129.71	129.71	18.79
1ST FLR.	---	161.81	161.81	16.57
2ND FLR.	244.25	---	244.25	43.12
3RD FLR.	246.15	---	246.15	35.64
4TH FLR.	246.15	---	246.15	35.64
5TH FLR.	246.15	---	246.15	35.64
6TH FLR.	246.15	---	246.15	35.64
7TH FLR.	258.50	---	258.50	35.58
8TH FLR.	258.50	---	258.50	35.58
TOTAL	1745.85	291.52	2037.37	292.20


CAR PARKING STATEMENT FOR SALE T/S

CARPET AREA 90 MT.	REQD. PARKING AS PER D.C. RULE	NO. OF FLATS	REQD. PARKING
BELOW 45.00	1 PARK / 4 TENE.	---	---
45.00 TO 60.00	1 PARK / 2 TENE.	01 NOS.	20.50 NOS.
60.00 TO 90.00	1 PARK / 1 TENE.	20 NOS.	20.00 NOS.
ABOVE 90.00	1 PARK / 1/2 TENE.	---	---
TOTAL		21 NOS.	20.50 NOS.
SHOP = 129.71 / 40.00			03.24 NOS.
OFFICE = 144.32 / 37.50			03.85 NOS.
10 % ADDITIONAL VISITORS PARKING FOR RESIDENTIAL			02.05 NOS.
10 % ADDITIONAL VISITORS PARKING FOR COMMERCIAL			02.00 NOS.
TOTAL			31.64 NOS.
PARKING REQUIRED =			32.00 NOS.
TOTAL PARKING PROPOSED			34.00 NOS.

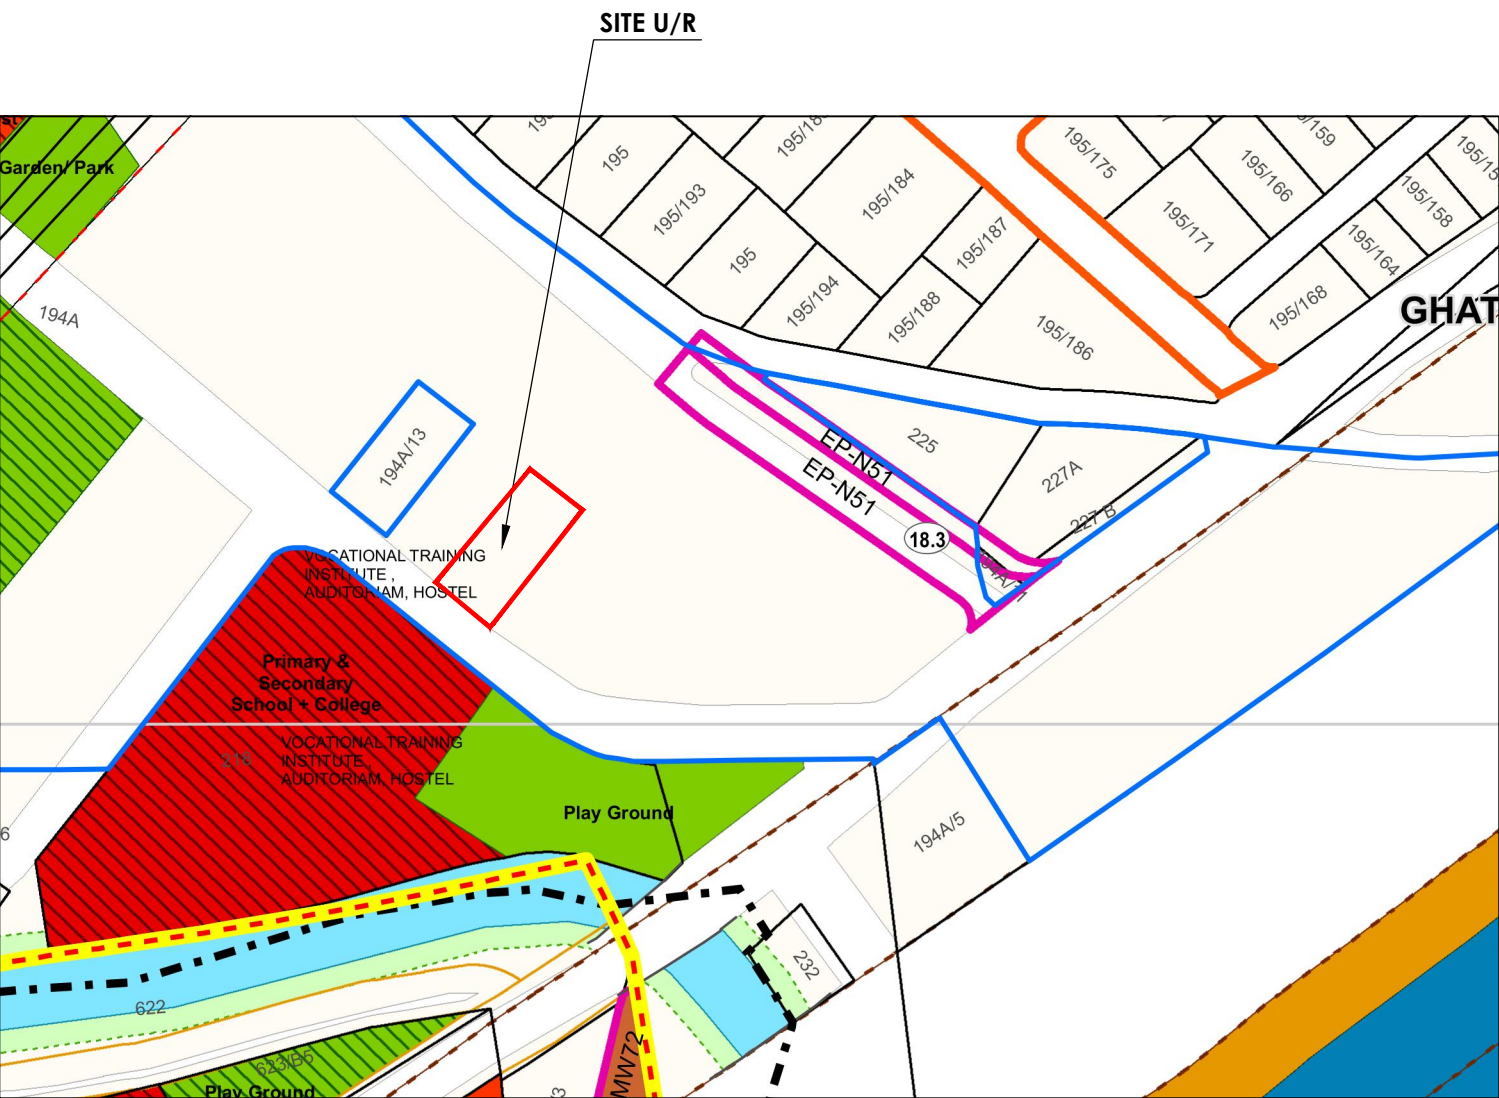

LOCATION PLAN

SCALE :- 1:6000

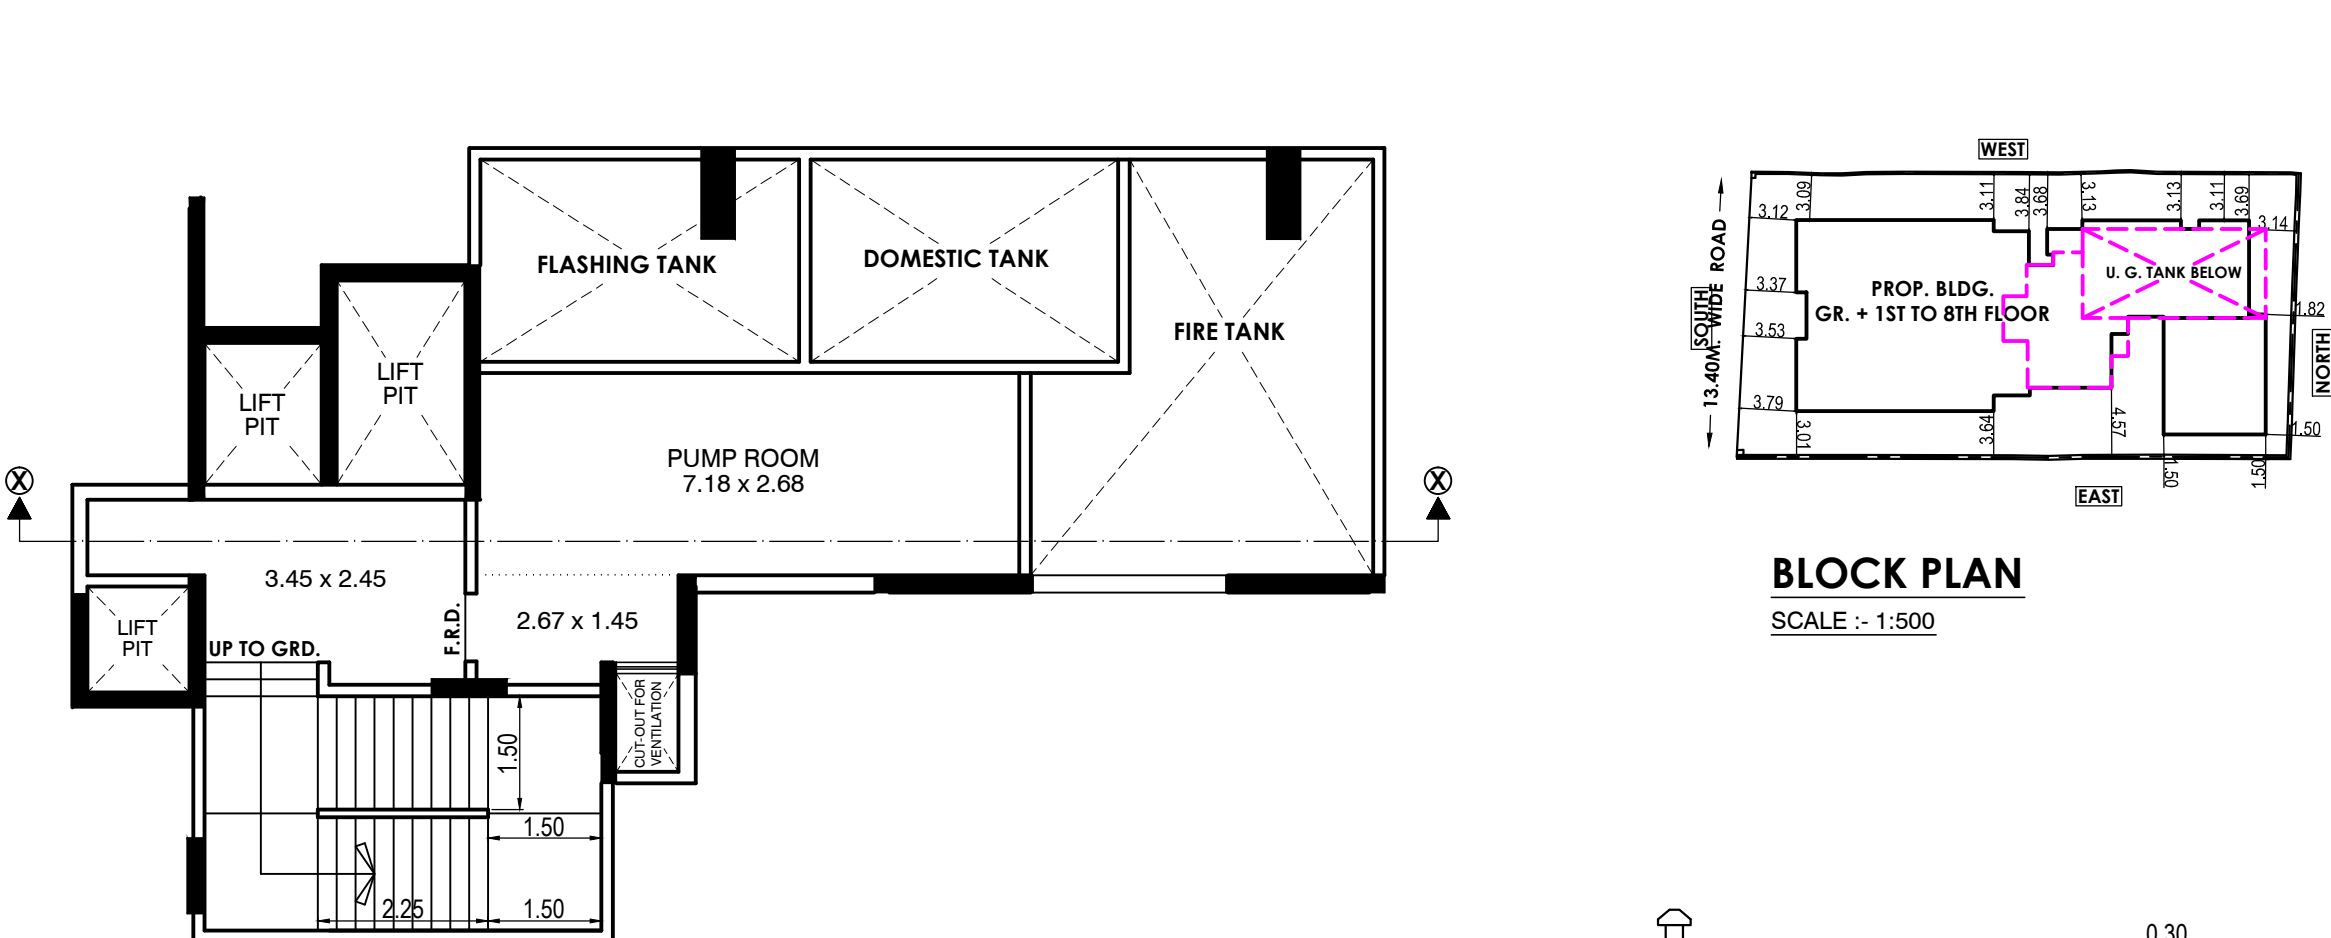


BLOCK PLAN

SCALE :- 1:500


BASEMENT FLOOR PLAN (U.G.T. & PUMP RM.)

SCALE :- 1:100

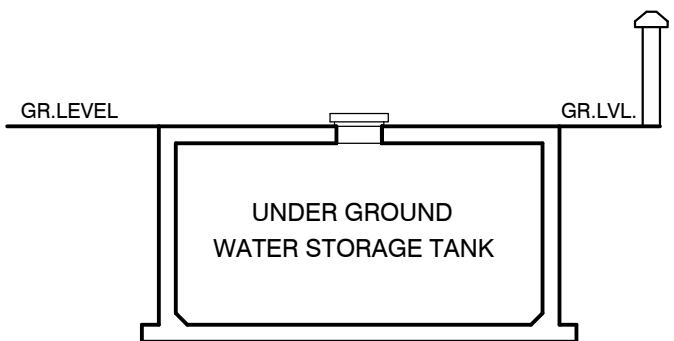


SECTION THROUGH U. G. TANK

SCALE :- 1 : 100

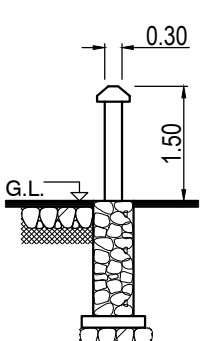


SECTION THRO' COMPOUND WALL

SCALE :- 1:100

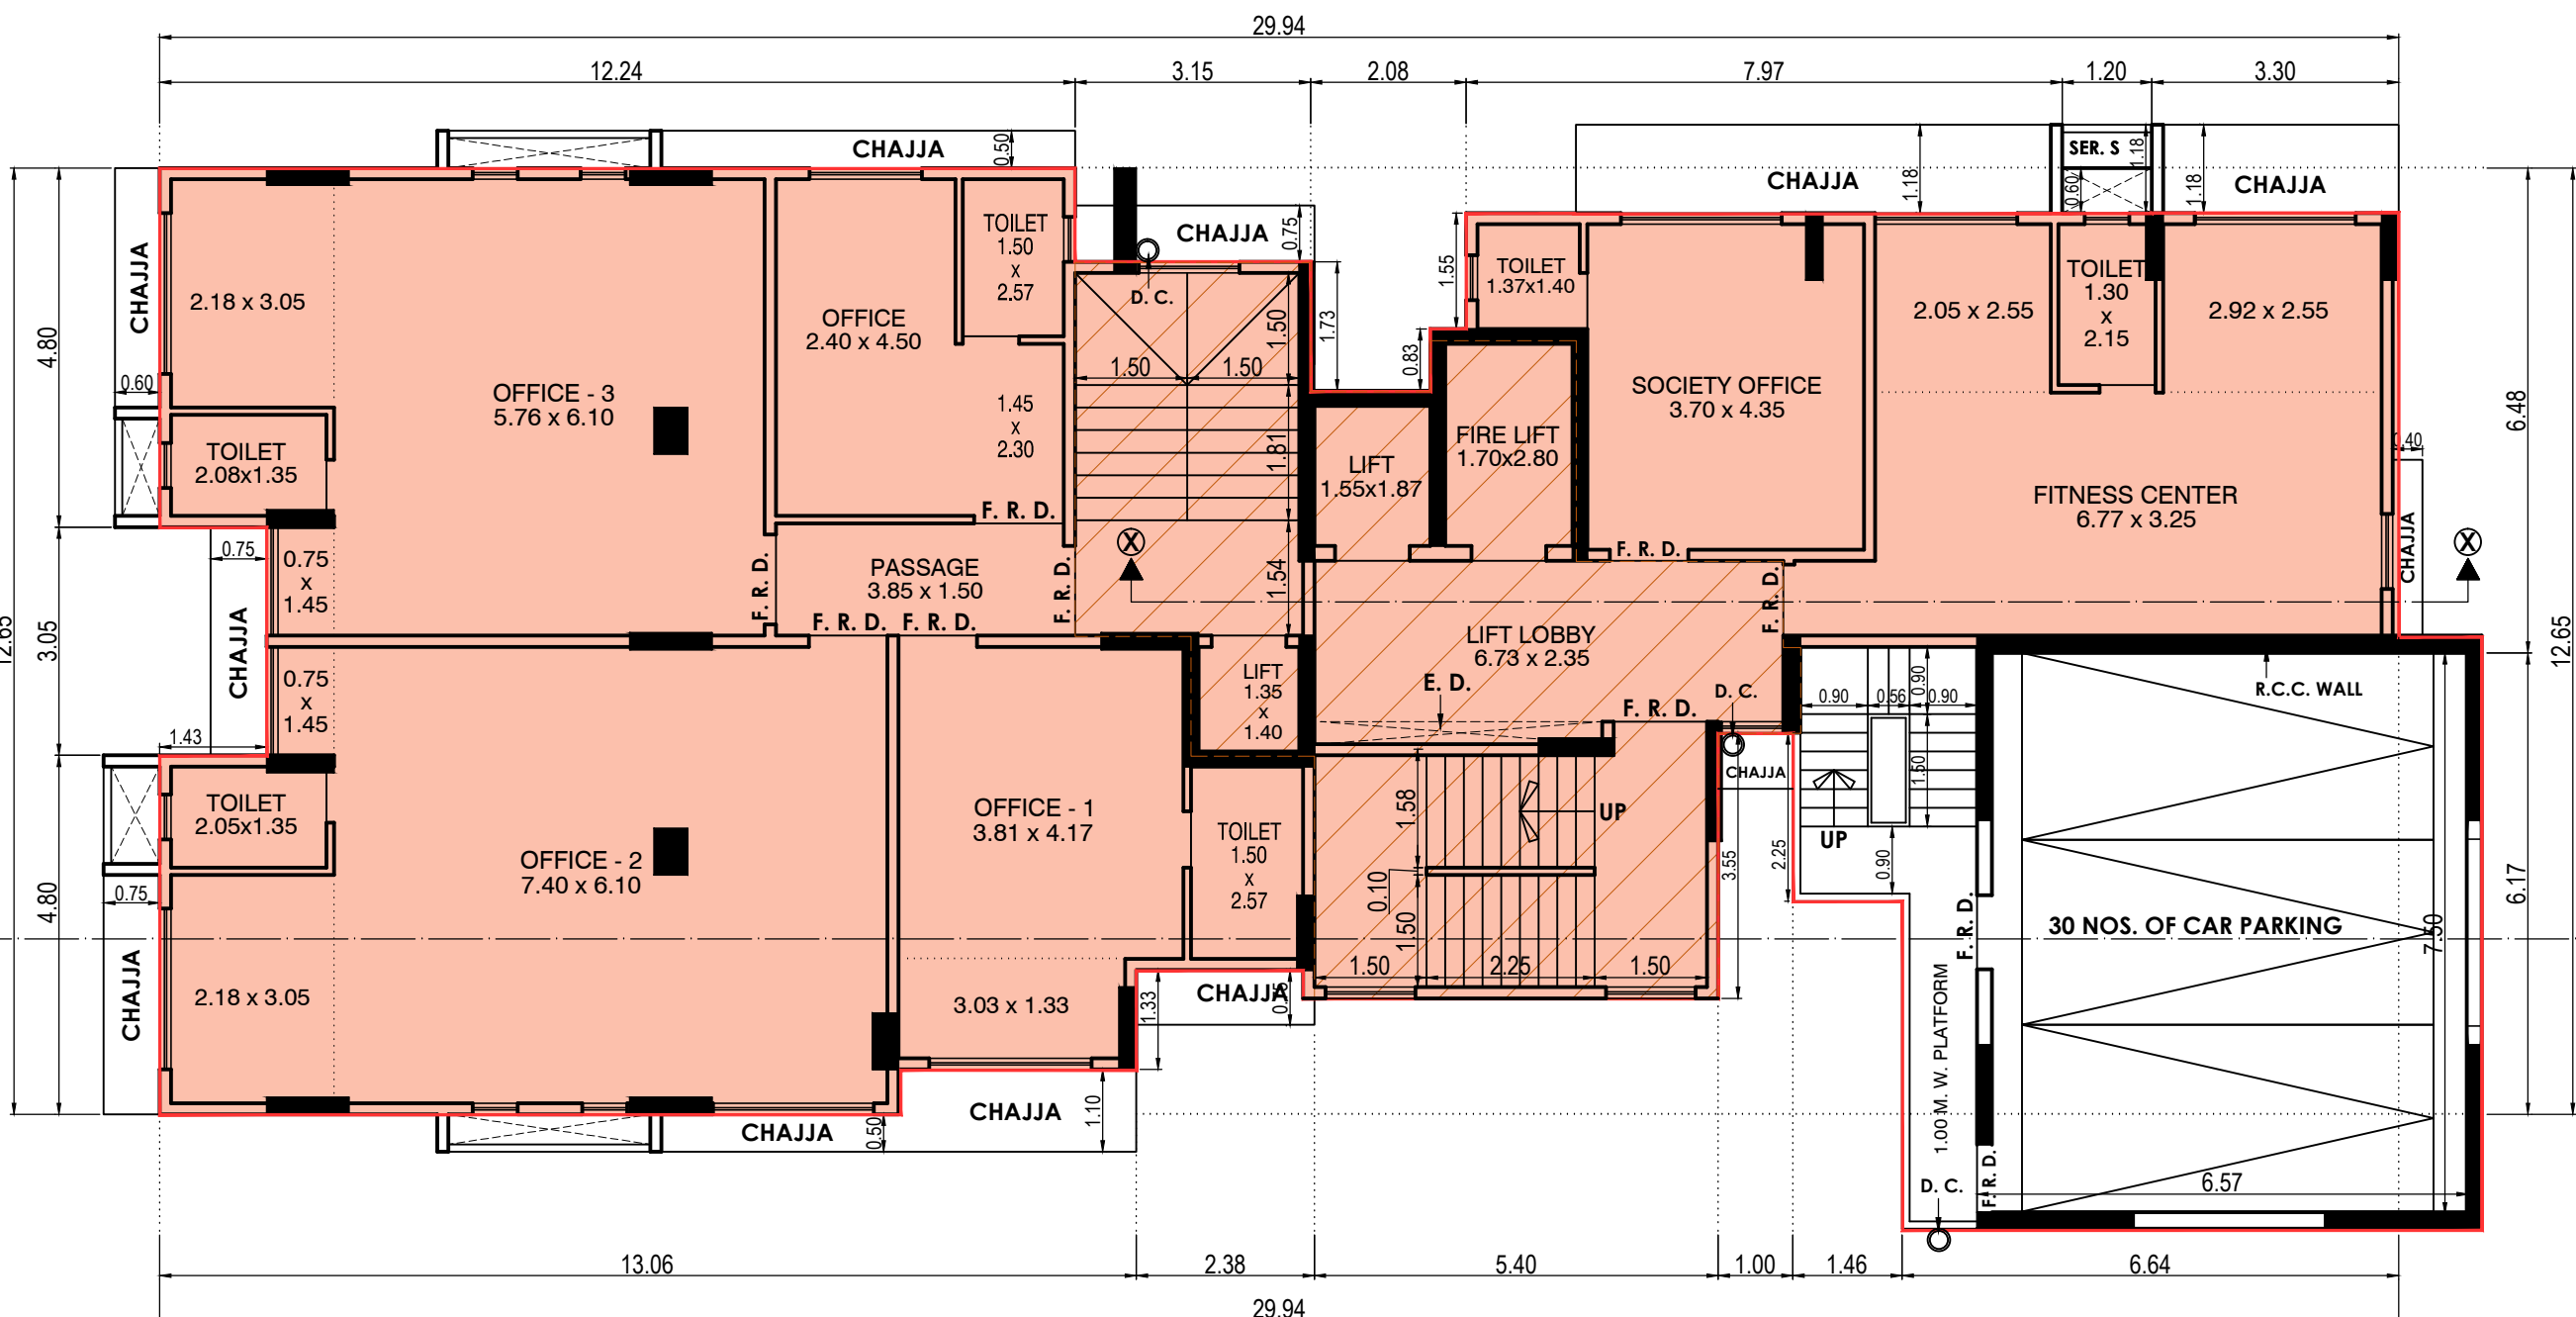


1ST FLOOR PLAN

SCALE :- 1:100

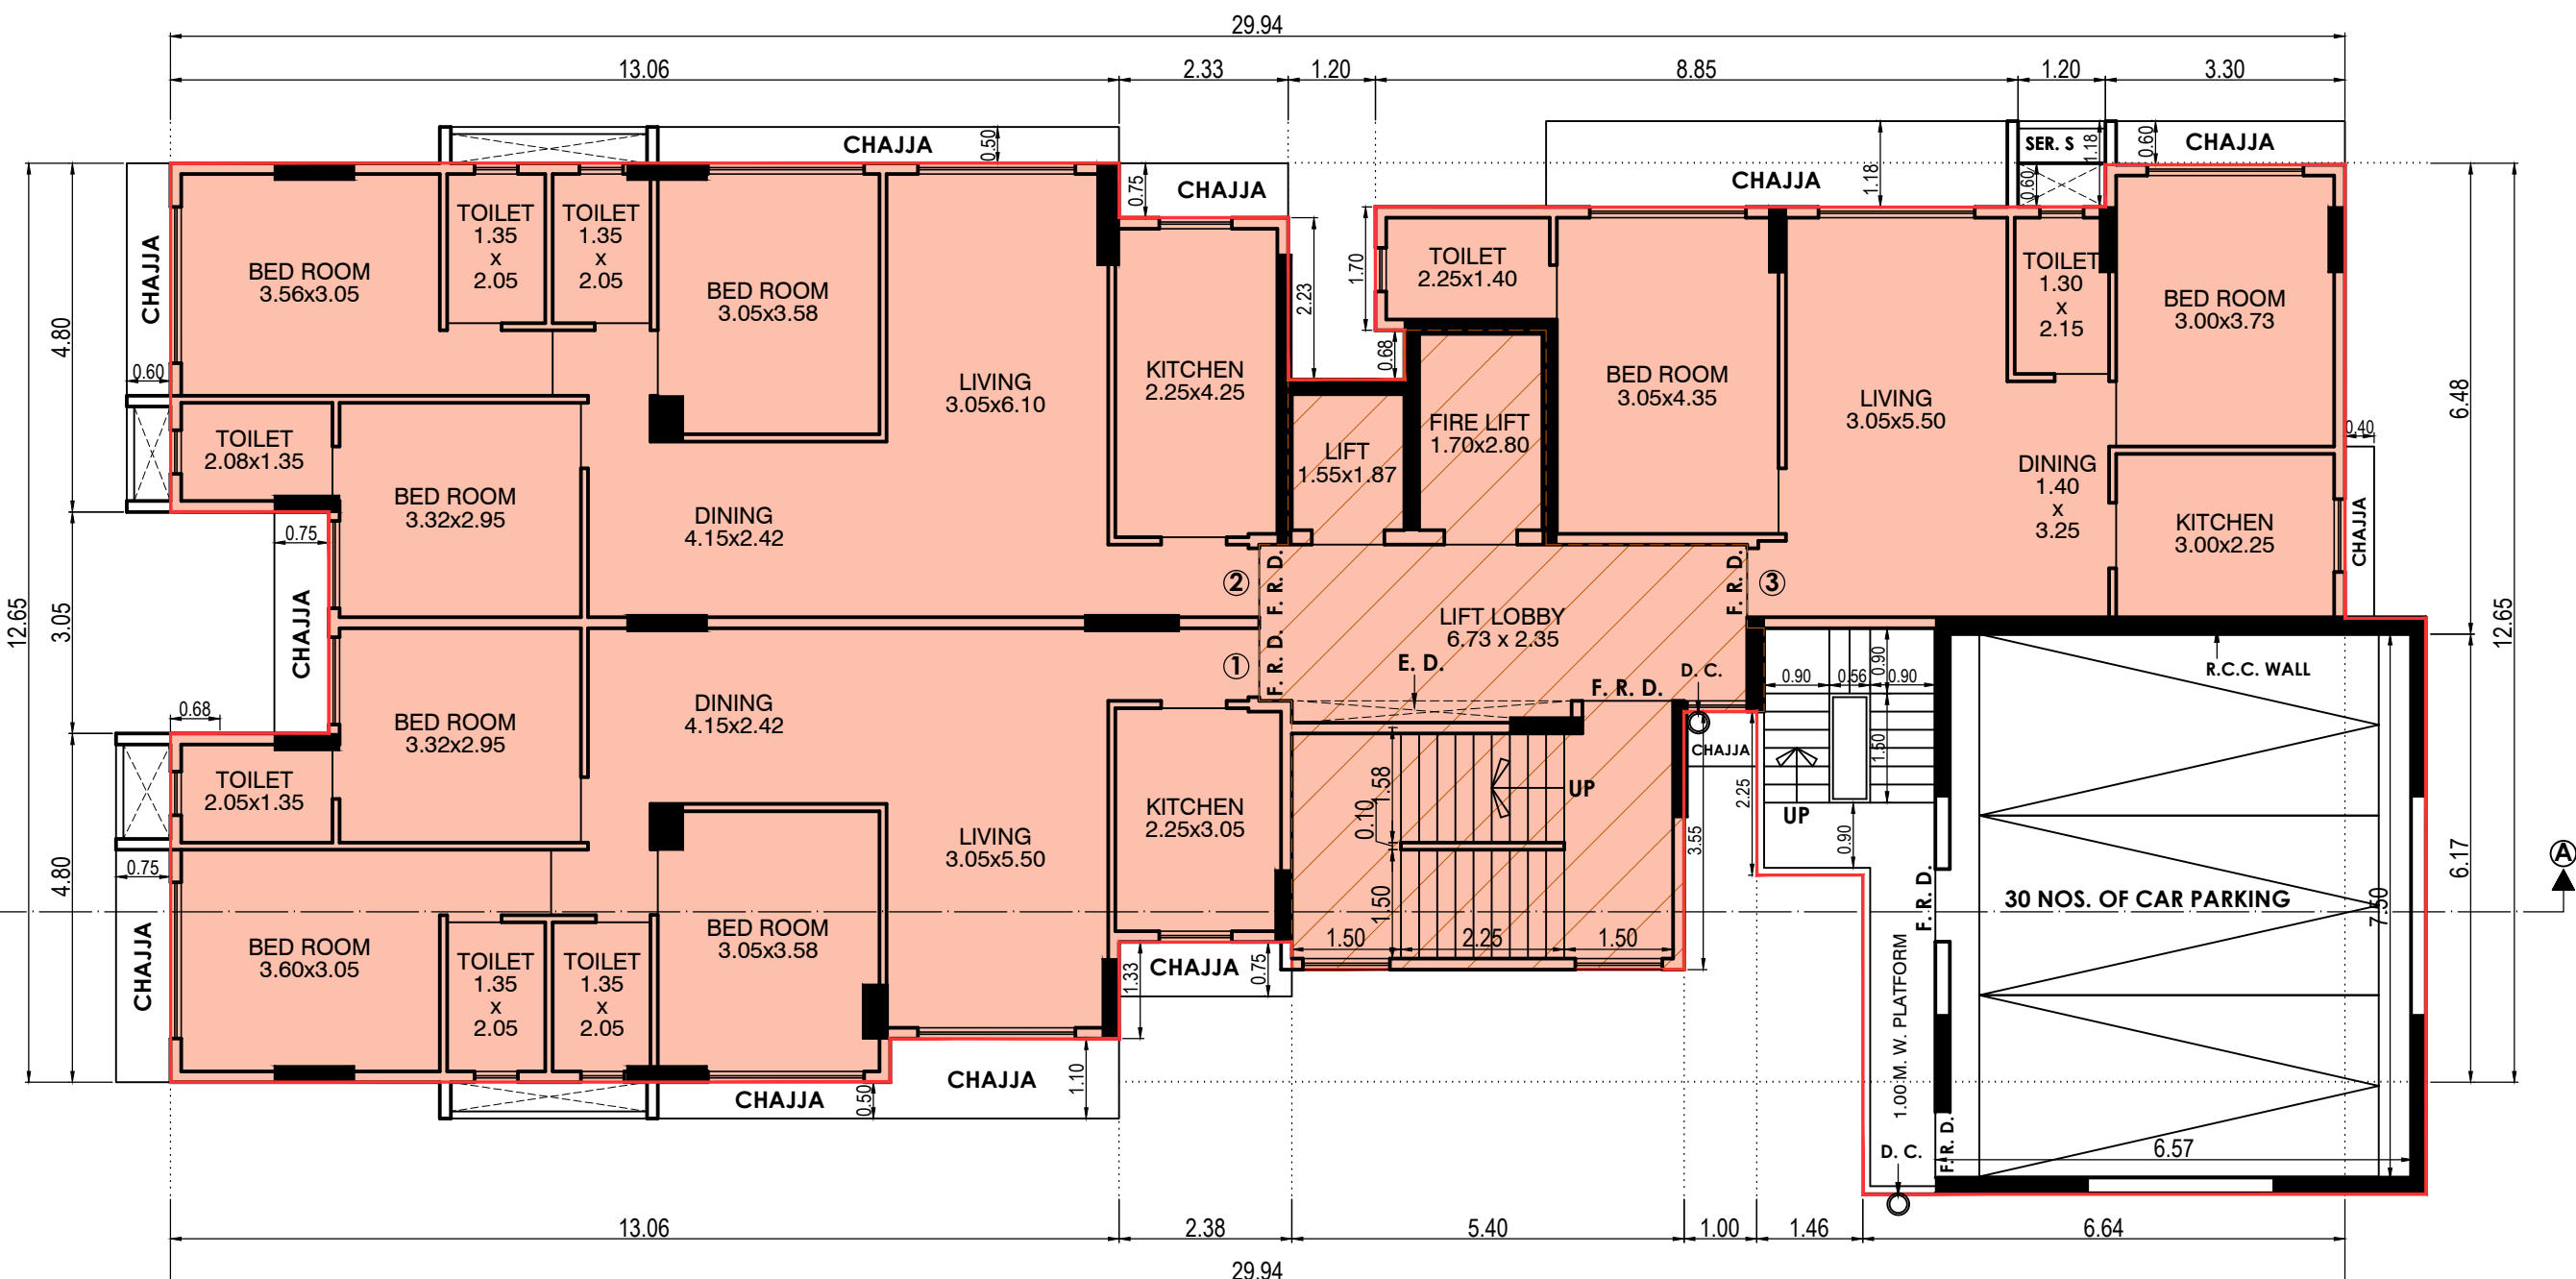


3RD TO 6TH FLOOR PLAN

SCALE :- 1:100

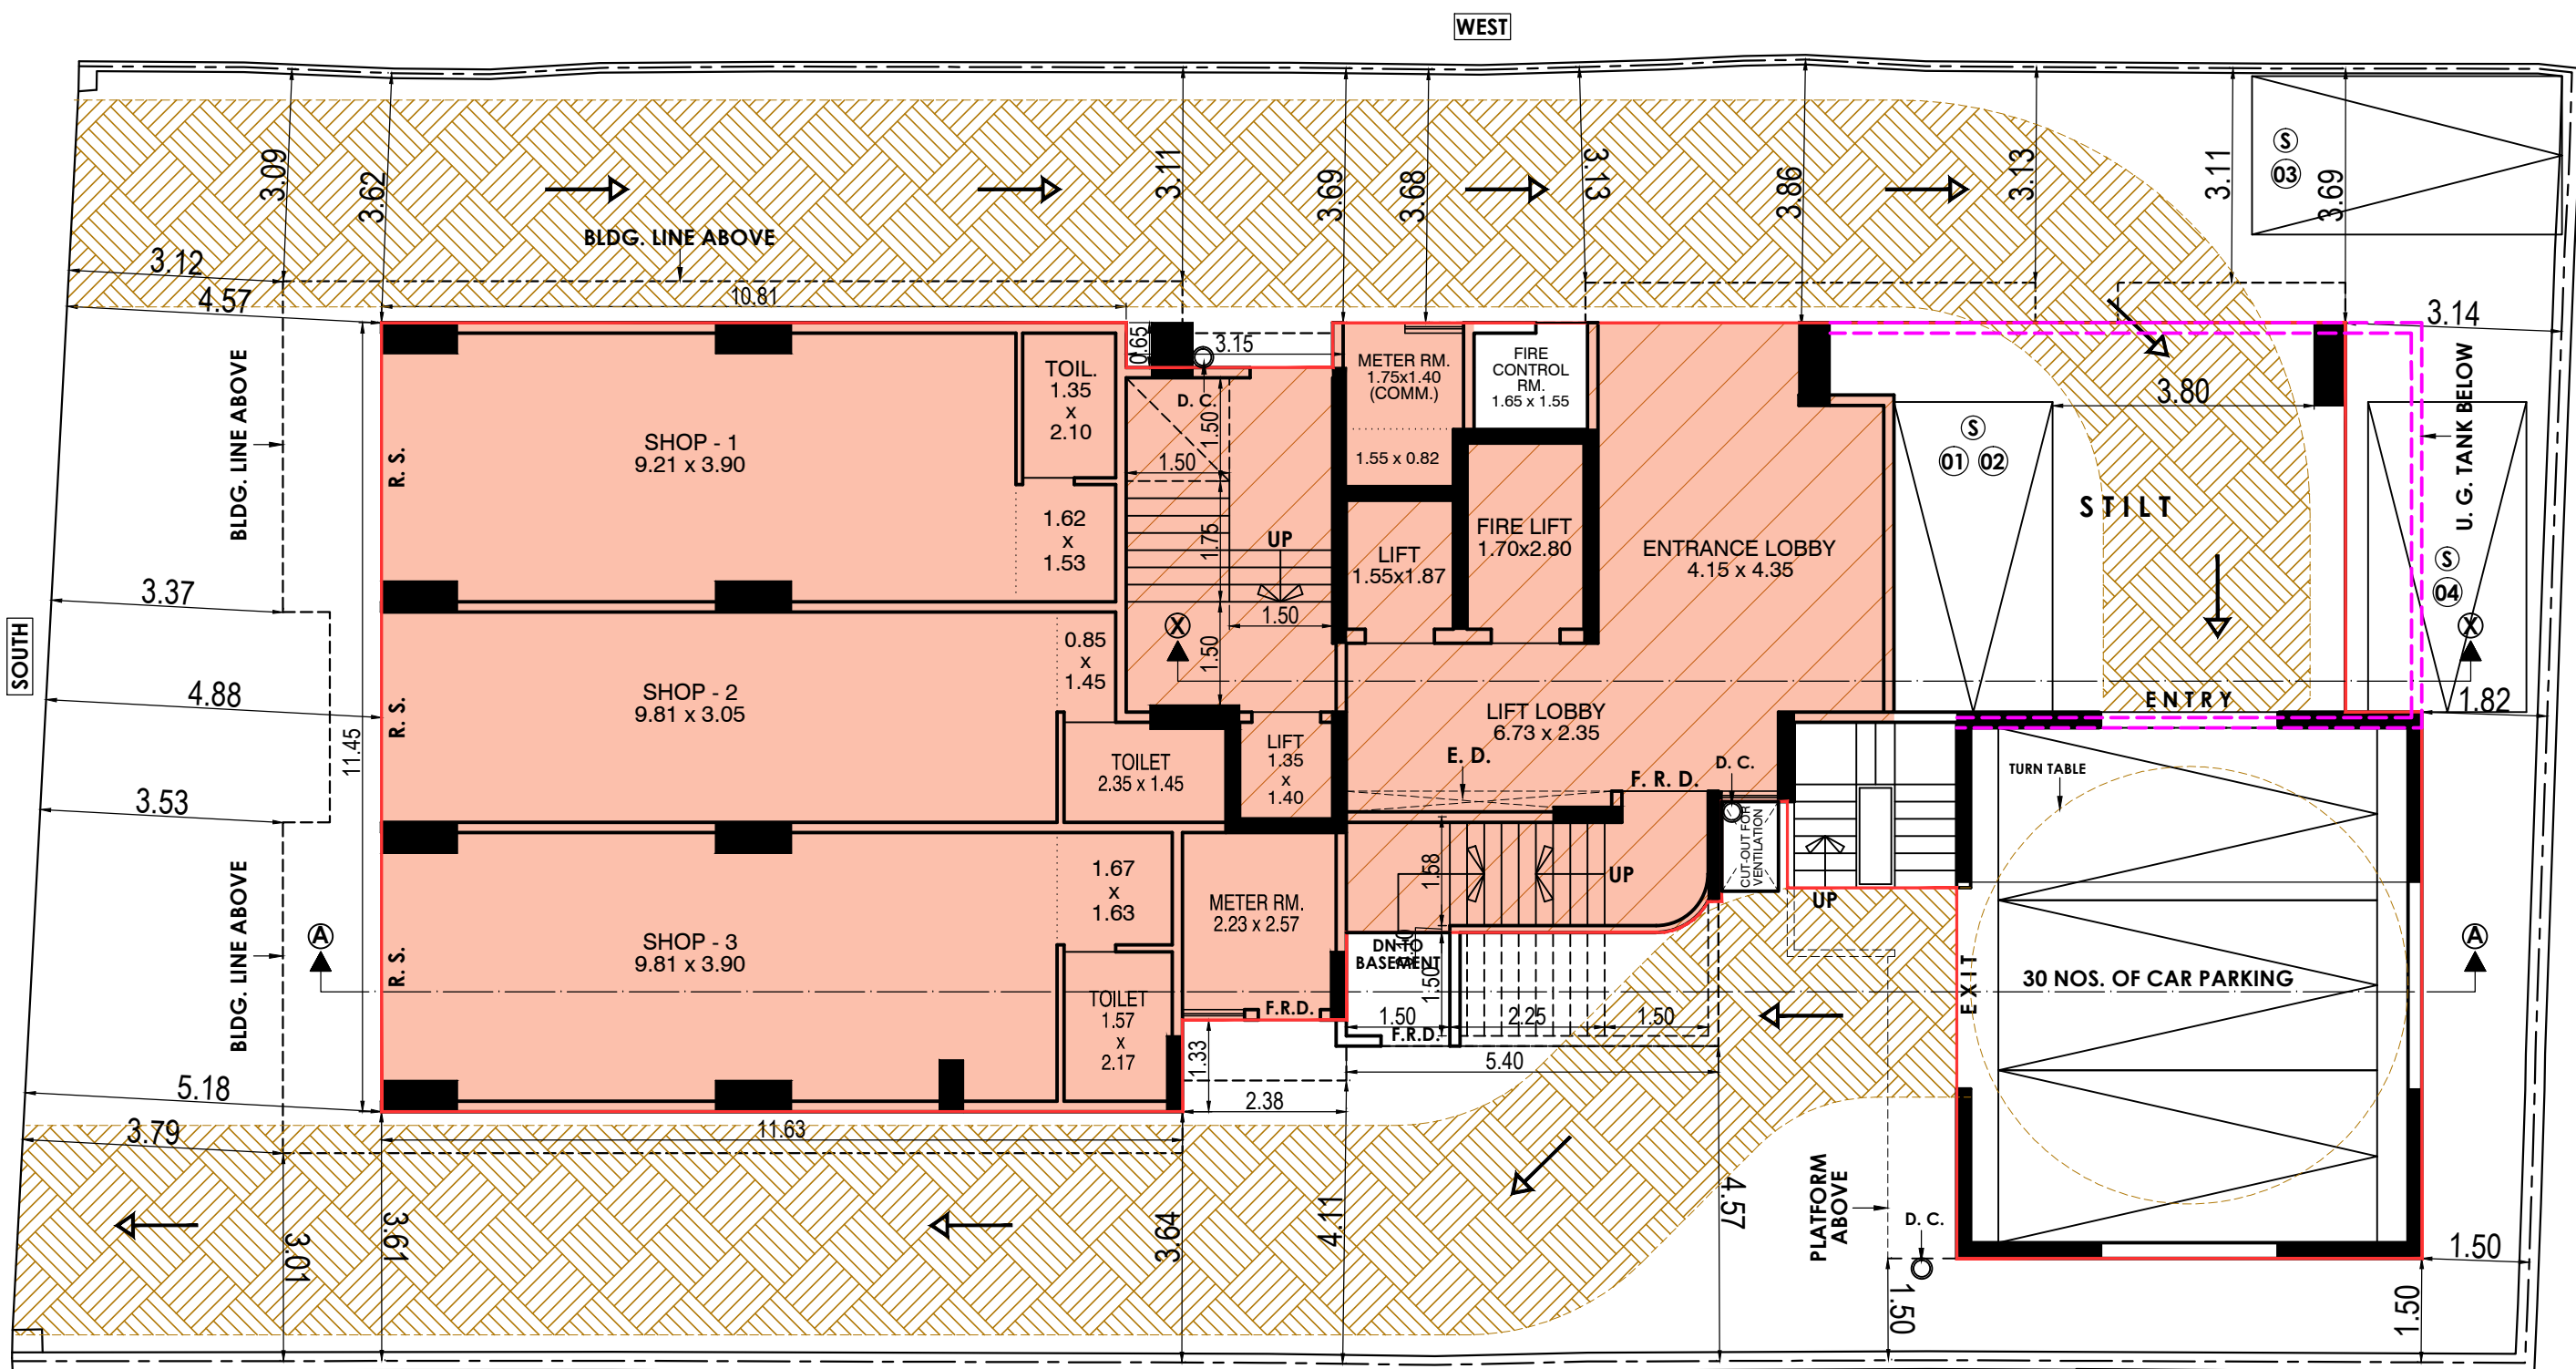

GROUND FLOOR PLAN

SCALE :- 1:100

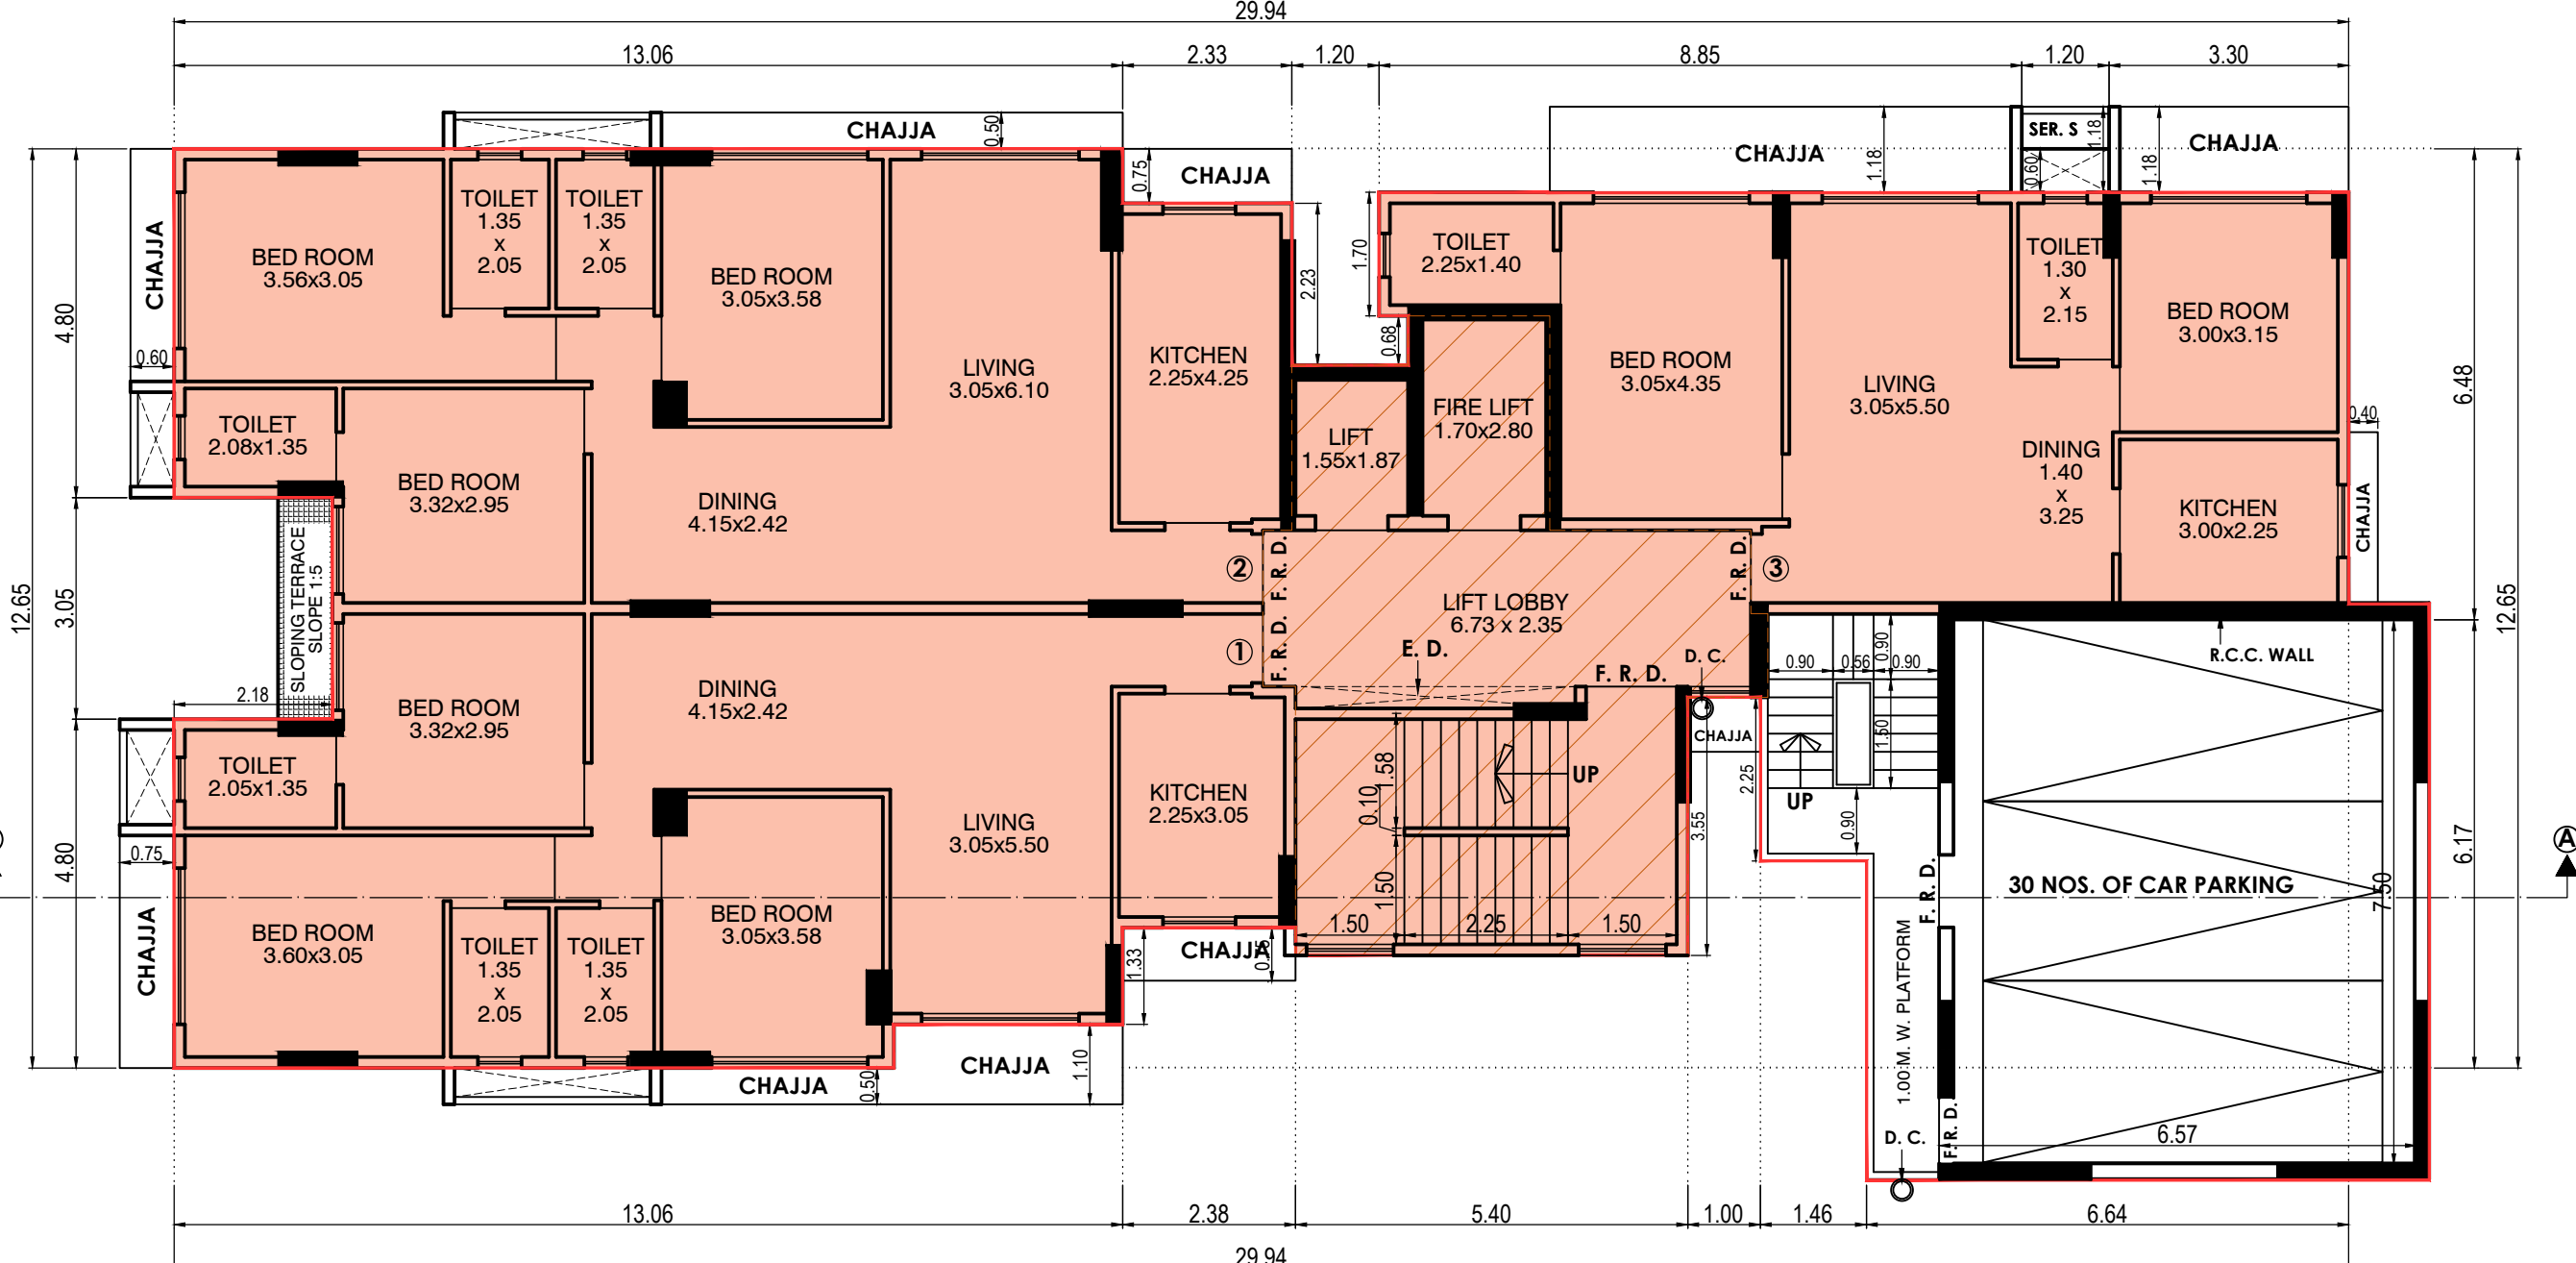

2ND FLOOR PLAN

SCALE :- 1:100

PROFORMA-B

CONTENT OF SHEET

GROUND FLOOR PLAN, 1ST TO 6TH FLOOR PLAN, BUILT-UP AREA SUMMARY, PARKING STATEMENT, STAIRCASE AREA STATEMENT, BLOCK & LOCATION PLAN

STAMP OF APPROVAL OF PLAN

FILE No. P-29345/2026(194/16/1/Apt.)/N Ward / GHATKOPAR - CFO / 1 / 1 New

D. F. O.

Dy. C. F. O.

CERTIFICATE OF AREA

CERTIFIED THAT THE I HAVE SURVEYED THE PLOT UNDER REFERENCE ON AND THAT THE DIMENSION OF THE SIDE ETC OF PLOT STATED ON THE PLOT ARE AS MEASURED ON SITE AND THE AREA SO WORKED OUT IS 686.00 SQ MT AND TALLIES WITH IS MORE THAN THE AREA STATED IN THE DOCUMENT OF OWNERSHIP, TOWN PLANNING SCHEME RECORD.

SIGNATURE OF L. S.

DESCRIPTION OF PROPOSAL

PROPOSED REDEVELOPMENT OF EXISTING BUILDING ON LAND BEARING OLD C. T. S. No. 194/A NEW CTS NO.194/A/16/1A (PT.) OF VILLAGE GHATKOPAR PLOT NO. 28, OF B. NATH PAI NAGAR, PROPOSED REDEVEAT VIDYA BHAWAN MARG, GHATKOPAR (EAST), MUMBAI-400077.

NAME OF OWNER


SIGNATURE

M/s. AYAANSH BUILDCON LLP
C. A. TO OWNER


NAME SIGN. & ADD. OF L. S.

SIGNATURE


ASHISH BHATT
802, 8TH FLOOR,
VIKAS CENTRE, JUNCTION OF N. S. B.
ROAD & S. L. ROAD, MULUND (WEST)
MUMBAI - 400080.

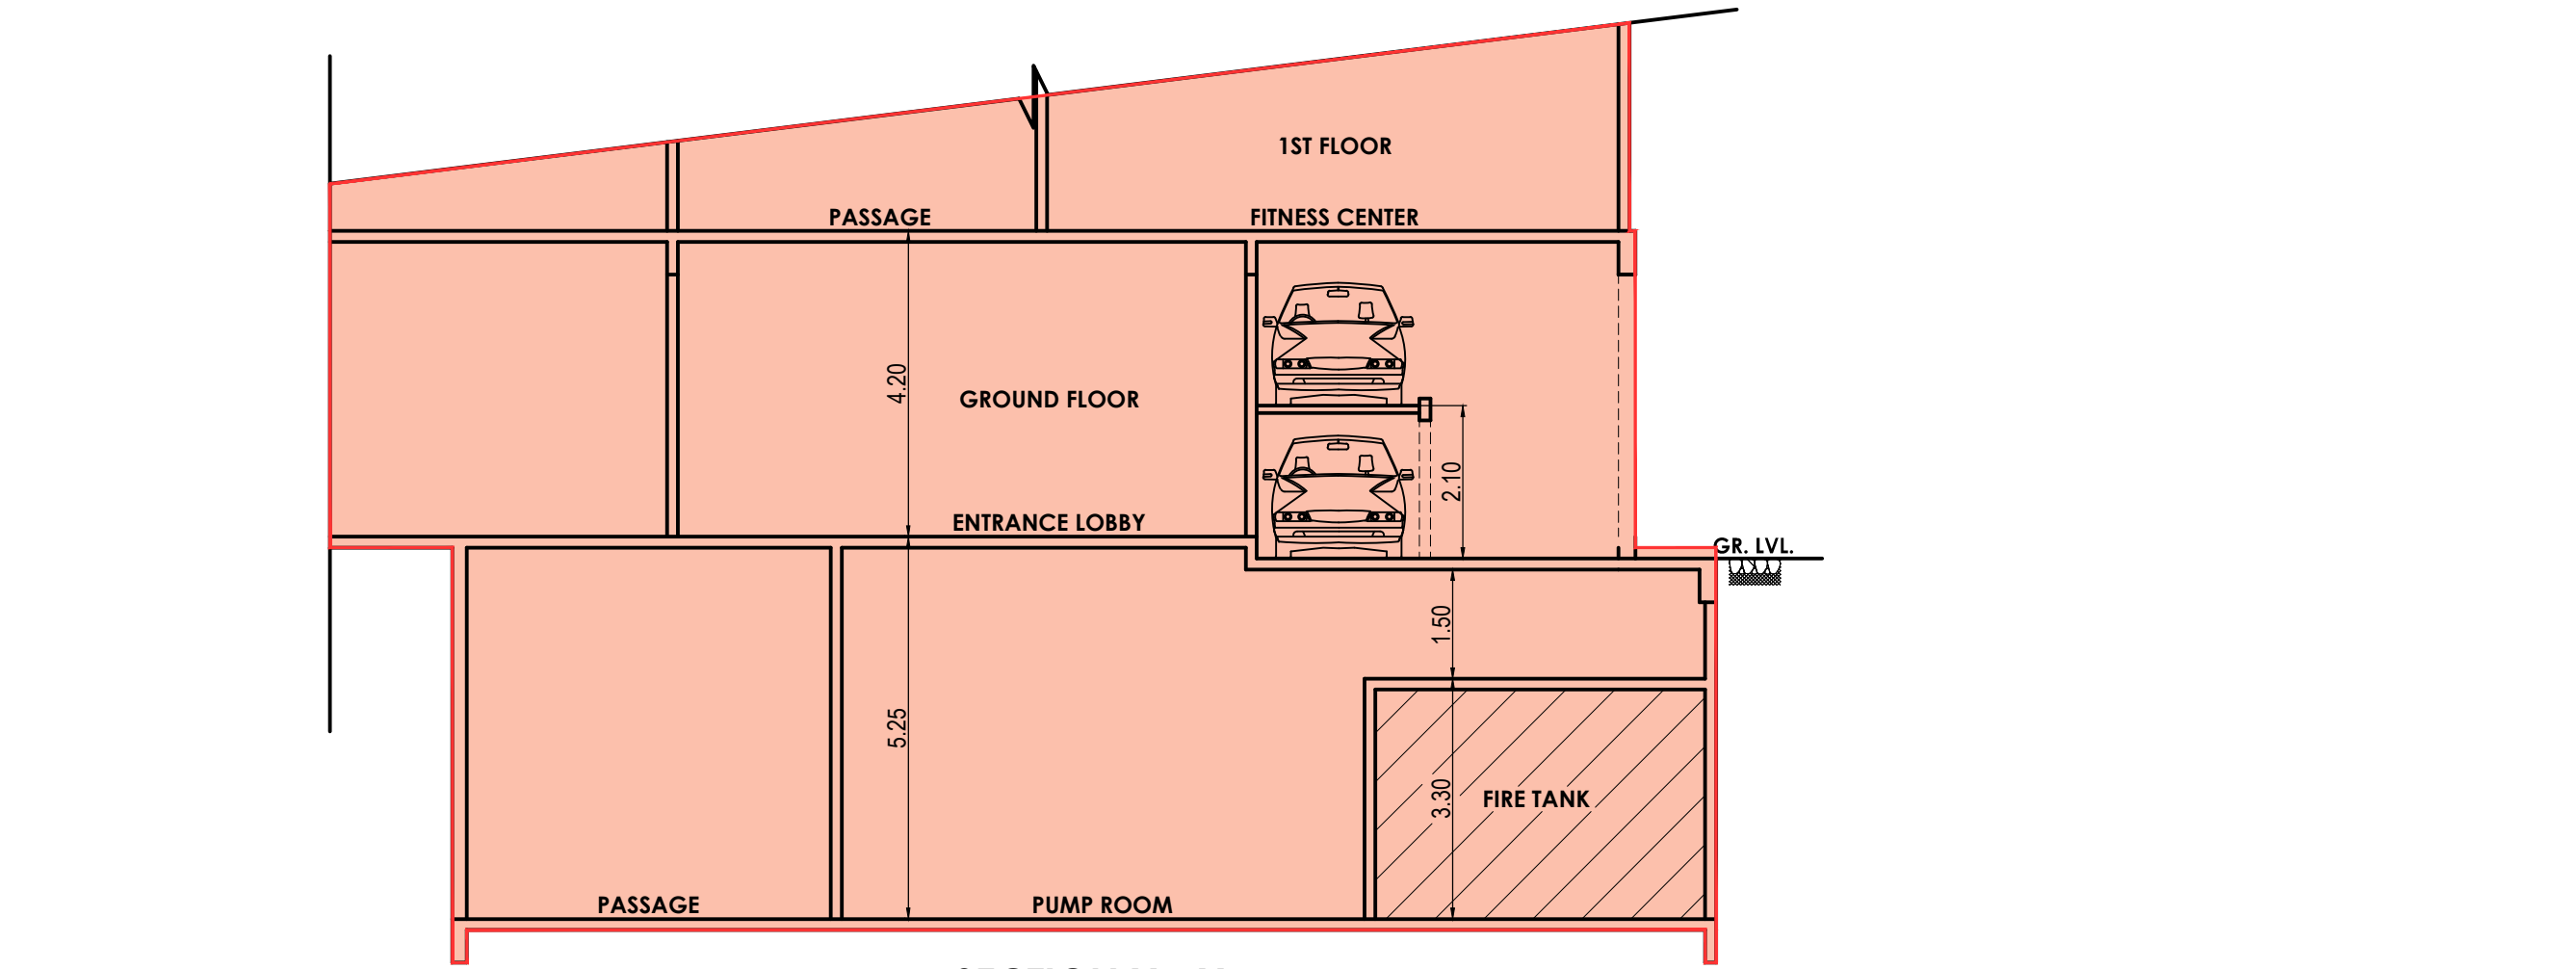


SECTION X - X
SCALE :- 1:100

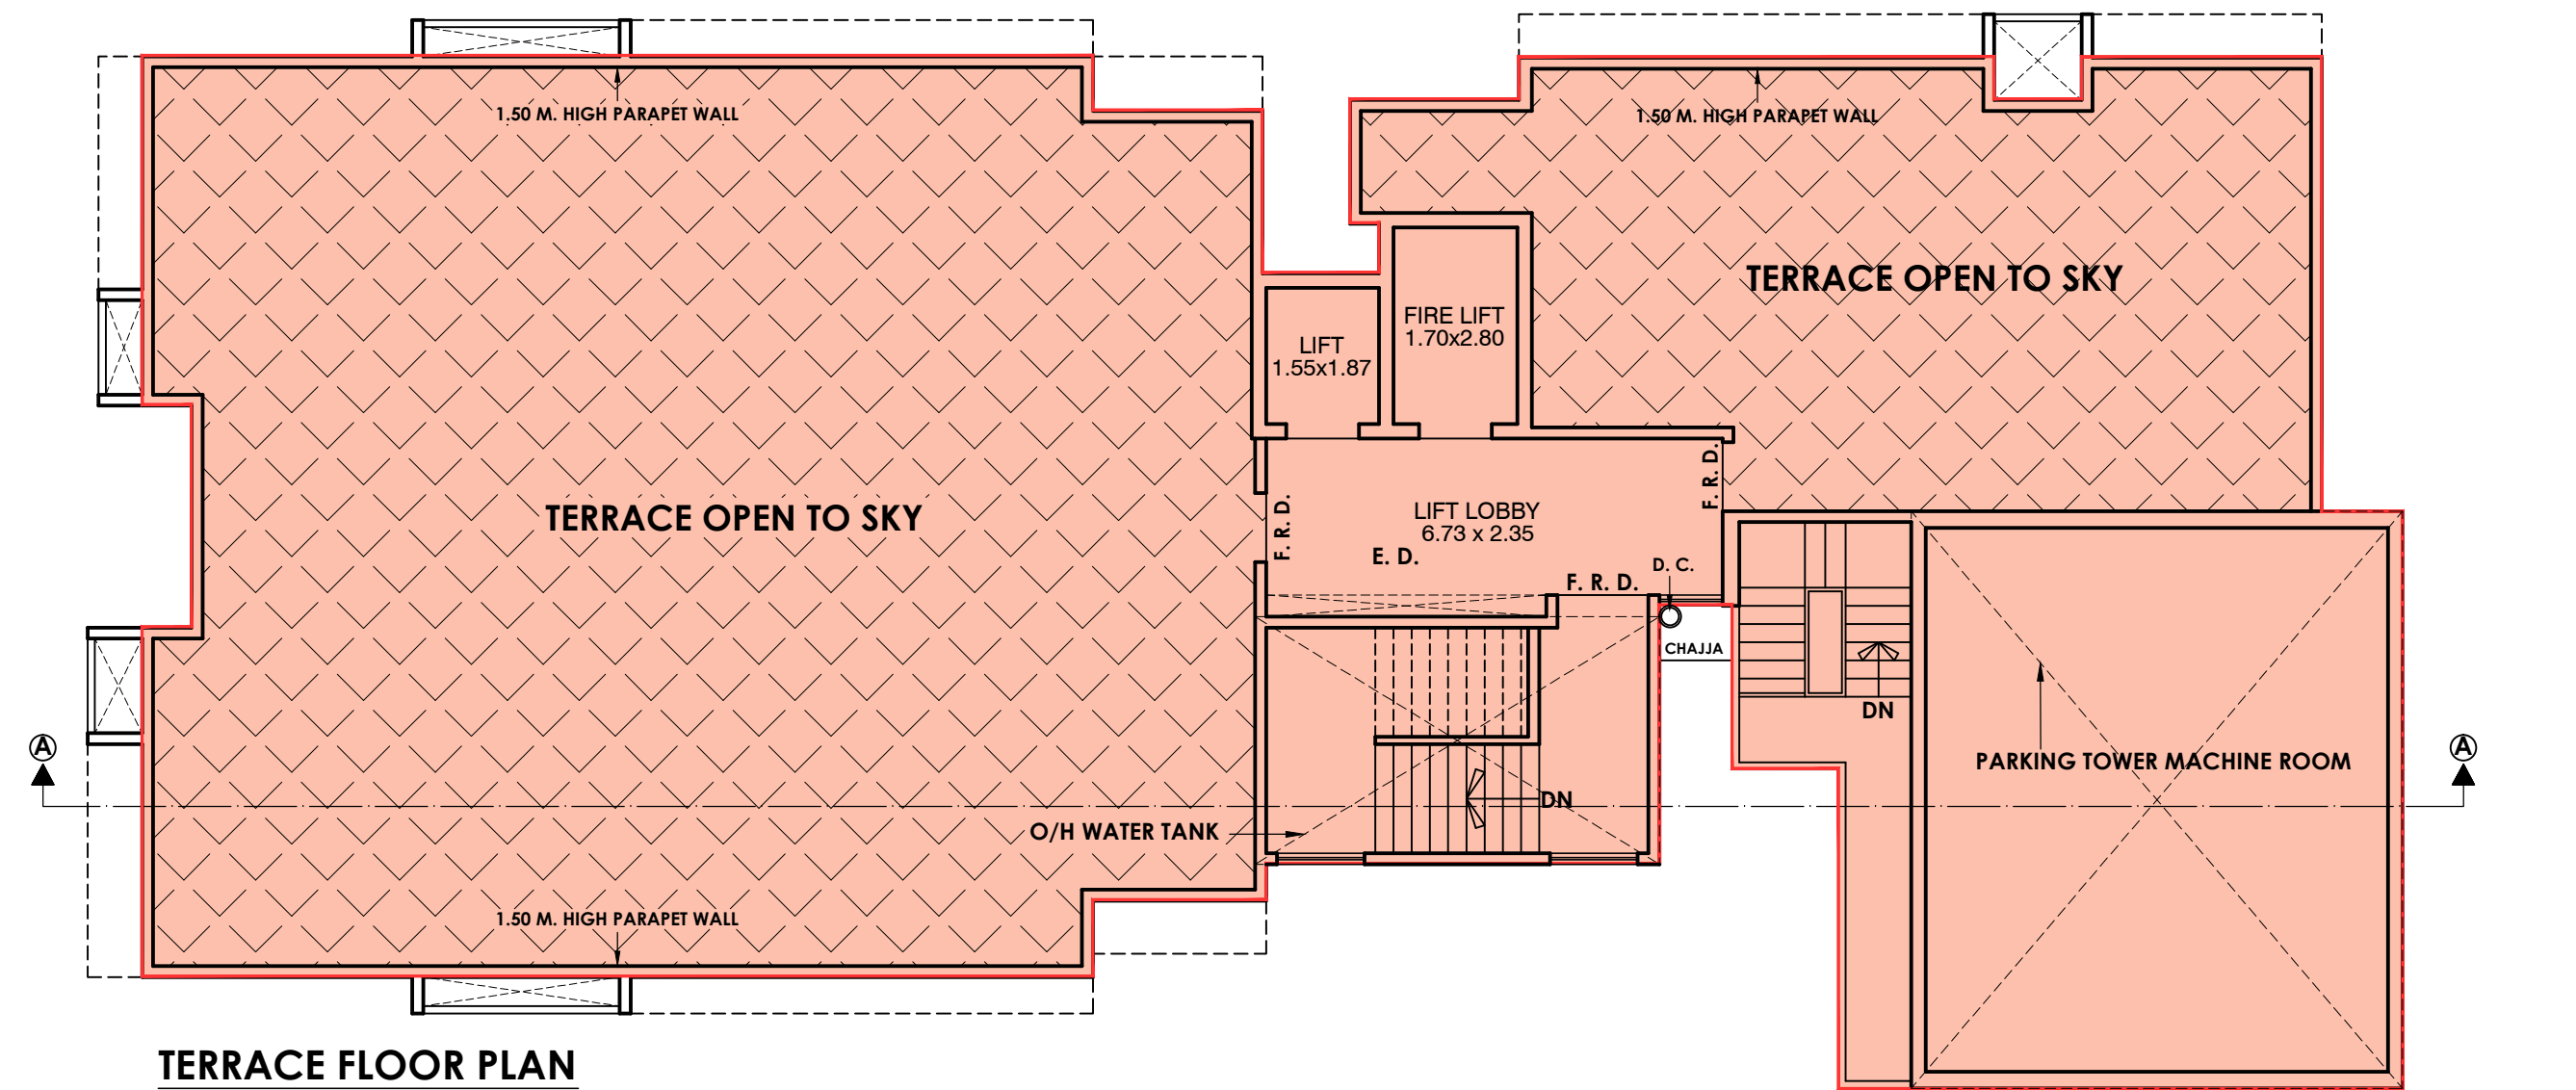

TERRACE FLOOR PLAN
SCALE :- 1:100

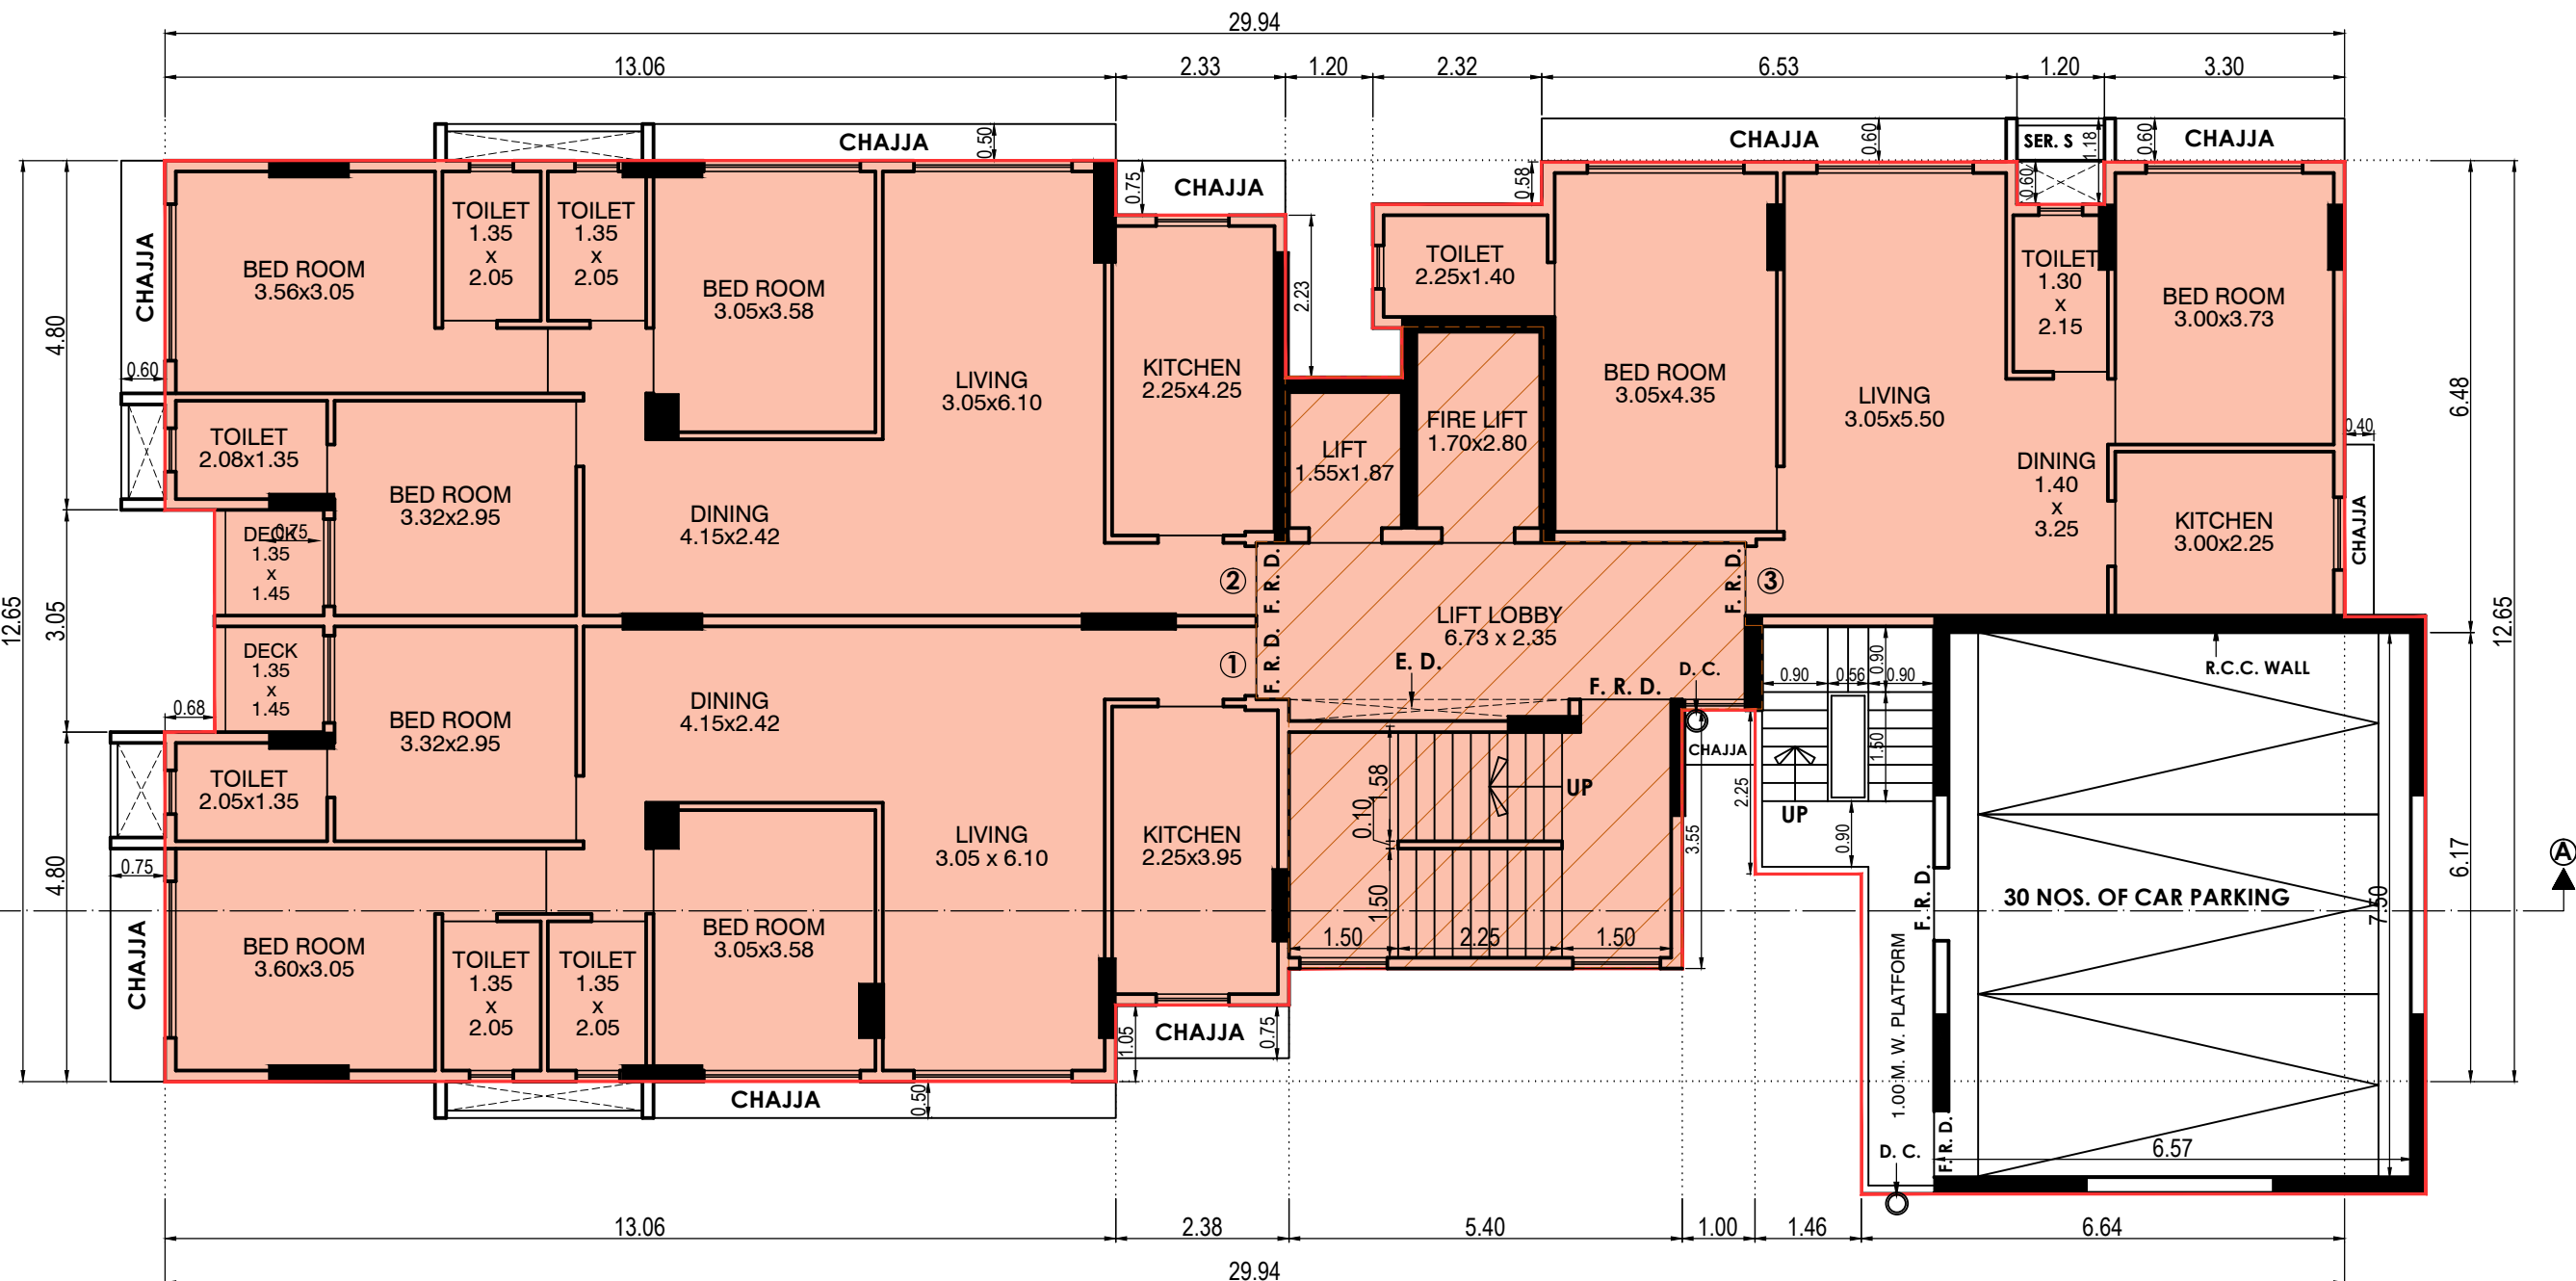

7TH & 8TH FLOOR PLAN
SCALE :- 1:100

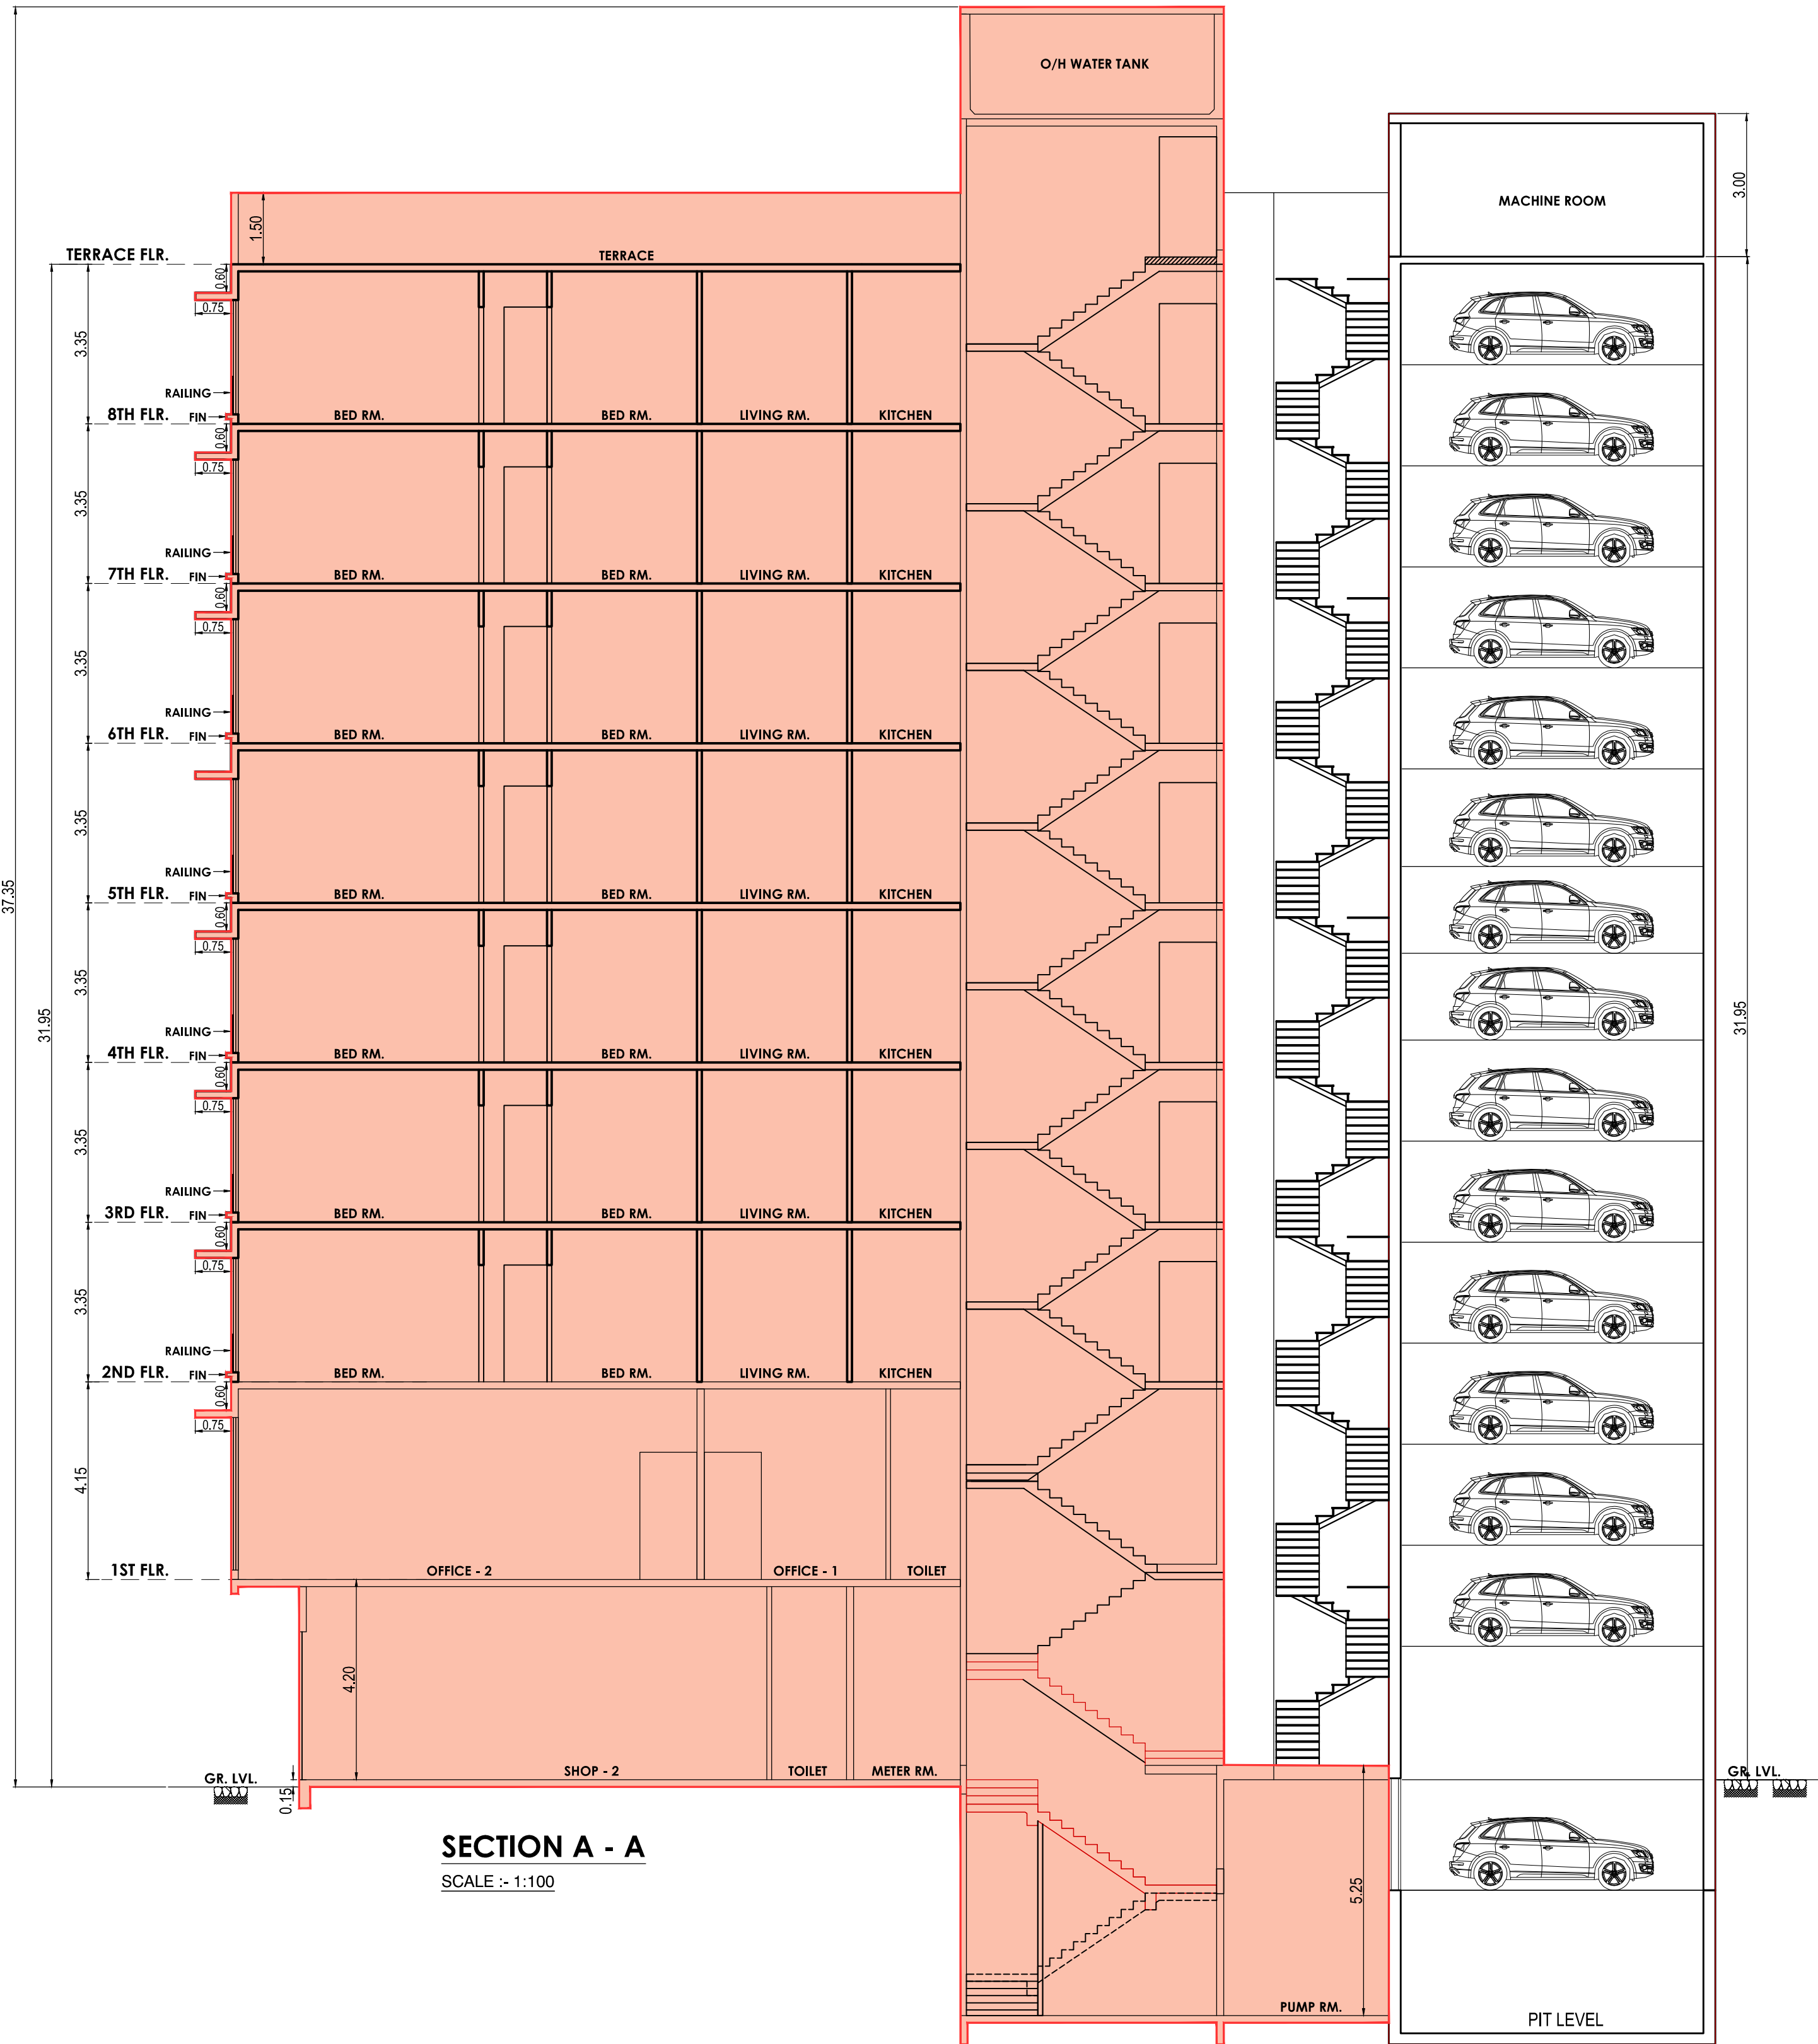

SECTION A - A
SCALE :- 1:100

PROFORMA-B	
CONTENT OF SHEET	
7TH & 8TH FLOOR PLAN, TERRACE FLOOR PLAN, SECTION A - A & X - X	
STAMP OF APPROVAL OF PLAN	
FILE No. P-29345/2026/(194A/16/1A(pt.)) /N Ward / GHATKOPAR - CFO / 1 / New	
D. F. O. Dy. C. F. O.	
DESCRIPTION OF PROPOSAL	
PROPOSED REDEVELOPMENT OF EXISTING BUILDING ON LAND BEARING OLD C. T.S. No. 194/A NEW CTS NO.194/A/16/1A (PT.) OF VILLAGE GHATKOPAR PLOT NO. 28, OF B. NATH PAI NAGAR, PROPOSED REDEVEAT VIDYA BHAWAN MARG, GHATKOPAR (EAST), MUMBAI-400077.	
NAME OF OWNER	SIGNATURE
M/s. AYAANSH BUILDCON LLP C. A. TO OWNER	
NAME SIGN. & ADD. OF L. S.	SIGNATURE
ASHISH BHATT 802, 8TH FLOOR, VIKAS CENTRE, JUNCTION OF N. S. B. ROAD & S. L. ROAD, MULUND (WEST) MUMBAI - 400080.	