


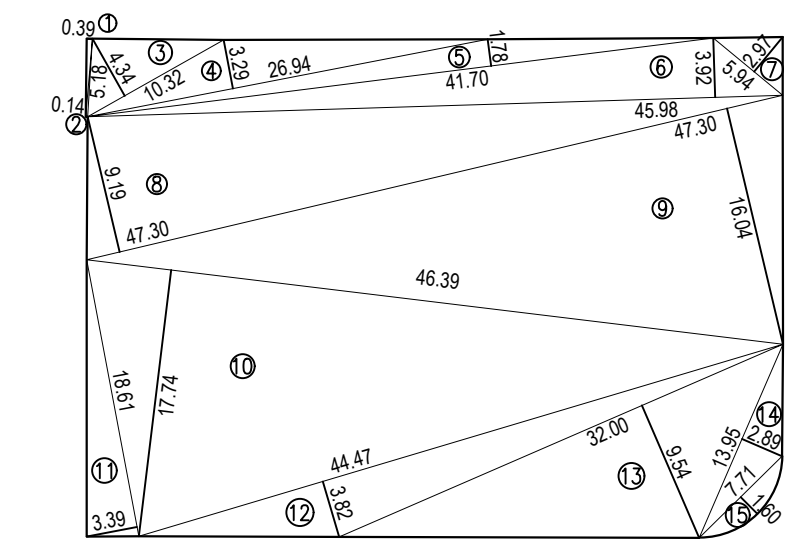


PLOT AREA LINE DIAGRAM

(PLOT - A)

SCALE :- 1:500

PLOT AREA CALCULATION

PLOT - A									
1	1/2	X	5.18	X	0.39	X	1NO	=	1.01 SQ.MT.
2	1/2	X	5.18	X	0.14	X	1NO	=	0.36 SQ.MT.
3	1/2	X	10.32	X	4.34	X	1NO	=	22.39 SQ.MT.
4	1/2	X	26.94	X	3.29	X	1NO	=	44.32 SQ.MT.
5	1/2	X	41.70	X	1.78	X	1NO	=	37.11 SQ.MT.
6	1/2	X	45.98	X	3.92	X	1NO	=	90.12 SQ.MT.
7	1/2	X	5.94	X	2.97	X	1NO	=	8.82 SQ.MT.
8	1/2	X	47.30	X	9.19	X	1NO	=	217.34 SQ.MT.
9	1/2	X	47.30	X	16.04	X	1NO	=	379.35 SQ.MT.
10	1/2	X	46.39	X	17.74	X	1NO	=	411.48 SQ.MT.
11	1/2	X	18.61	X	3.39	X	1NO	=	31.54 SQ.MT.
12	1/2	X	44.47	X	3.82	X	1NO	=	84.94 SQ.MT.
13	1/2	X	32.00	X	9.54	X	1NO	=	152.64 SQ.MT.
14	1/2	X	13.95	X	2.89	X	1NO	=	20.16 SQ.MT.
15	2/3	X	7.71	X	1.60	X	1NO	=	8.22 SQ.MT.
TOTAL ADDITION									= 1509.80 SQ.MT. X

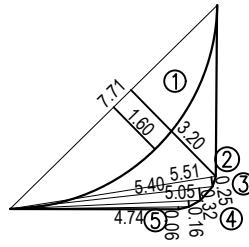

SET-BACK AREA LINE DIAGRAM

(PLOT - B)

SCALE :- 1:200

SET-BACK AREA CALCULATION


PLOT - B									
1	1/2	X	7.68	X	3.20	X	1NO	=	12.29 SQ.MT.
2	1/2	X	5.51	X	0.25	X	1NO	=	0.69 SQ.MT.
3	1/2	X	5.40	X	0.32	X	1NO	=	0.86 SQ.MT.
4	1/2	X	5.05	X	0.16	X	1NO	=	0.40 SQ.MT.
5	1/2	X	4.74	X	0.06	X	1NO	=	0.14 SQ.MT.
TOTAL ADDITION									= 14.38 SQ.MT. X

DEDUCTION

6	2/3	X	7.71	X	1.60	X	1NO	=	8.22 SQ.MT. Y
TOTAL SET-BACK AREA									= 6.16 SQ.MT.


BUILT- UP AREA SUMMARY				
FLOORS	B. U. AREA SQ.MTS	STAIRCASE LIFT & LIFT LOBBY AREA	STILT / FITNESS CENTER SOC. OFFICE / REFUGE FREE OF FSI SQ.MTS	GROSS B. U. AREA IN SQ. MT.
GR. FLR.	692.55	47.93	392.10	1132.58
1ST FLR.	---	---	1132.58	1132.58
2ND FLR.	---	---	1132.58	1132.58
3RD FLR.	---	---	388.31	388.31
4TH FLR.	323.60	47.95	---	371.55
5TH FLR.	326.83	47.95	---	374.78
6TH FLR.	326.83	47.95	---	374.78
7TH FLR.	233.37	47.95	94.89	376.21
8TH FLR.	328.26	47.95	---	376.21
9TH FLR.	328.26	47.95	---	376.21
10TH FLR.	340.58	47.73	---	388.31
11TH FLR.	340.58	47.73	---	388.31
12TH FLR.	340.58	47.73	---	388.31
13TH FLR.	340.58	47.73	---	388.31
14TH FLR.	283.41	49.22	55.68	388.31
15TH FLR.	340.58	47.73	---	388.31
16TH FLR.	246.82	47.73	93.78	388.31
TERRACE FLR.	---	---	51.18	51.18
L. M. R. G. H. T. & ST. CABIN	---	---	70.00	70.00
TOTAL	4792.83	671.23	3411.08	8875.14

CAR PARKING STATEMENT			
CARPET AREA SQ.MT.	REDD. PARKING AS PER D.C. RULE	NO. OF FLATS	REQ. PARKING
---	SHOP = 640.92 / 40	---	16.02 NOS
BELOW 45.00	1 PARK / 4 TENE.	---	---
45.00 TO 60.00	1 PARK / 2 TENE.	---	---
60.00 TO 90.00	1 PARK / 1 TENE.	42 NOS	42.00 NOS
ABOVE 90.00	1 PARK / 1/2 TENE.	07 NOS	14.00 NOS
TOTAL	---	49 NOS	72.02 NOS.
10% ADDITIONAL VISITORS PARKING FOR COMMERCIAL		---	01.60 NOS.
10% ADDITIONAL VISITORS PARKING FOR RESIDENTIAL		---	05.60 NOS.
TOTAL		---	79.22 NOS.
PARKING REQUIRED =		---	79.00 NOS.
TOTAL PARKING PROVIDED =		---	79.00 NOS.

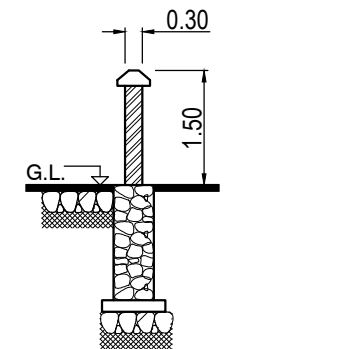


SECTION THRO' COMPOUND WALL

SCALE :- 1:100

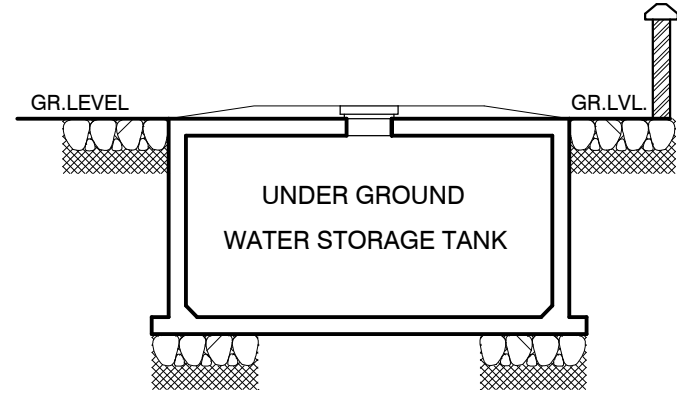


SECTION THROUGH U. G. TANK

SCALE :- 1 : 100

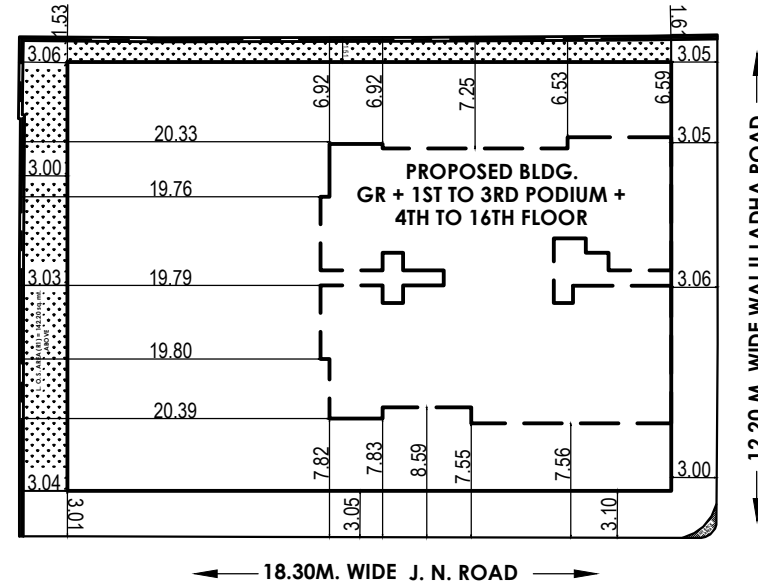

BLOCK PLAN

SCALE :- 1:500

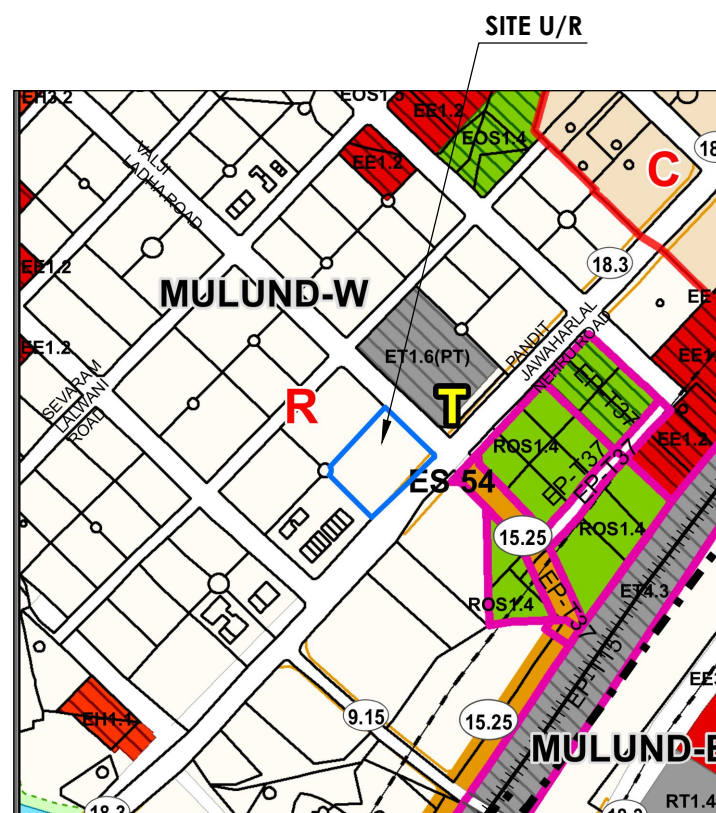

LOCATION PLAN

SCALE :- 1:4000

PROFORMA - A		TOTAL
A) AREA STATEMENT		SQ.MTS.
1	Area of Plot	1481.70
a)	Area of Reservation in plot	---
b)	Area of Road Set back	6.16
c)	Area of D. P. Road	---
2	Deductions for :	
A) For Reservation		
a)	Set-back area as per DCR 16	6.16
b)	DP road area as per DCR 16	---
c)	Reservation area as per DCR 17	---
Total of 2(A)		6.16
B) For Amenity Area		
A	Area of amenity as per DCR 14 (A)	---
B	Area of 5% amenity	---
C	Area of amenity as per DCR 15	---
D	Area of amenity as per DCR 35	---
Total of 2(B)		---
C) Deduction for existing BUA to be retained		
A	Land component of the same	---
Total of 2(C)		---
3	Total deduction : [2 (A) + 2 (B) + 2 (C)]	6.16
4	Balance area of plot (1 - 3)	1475.54
5	Deduction for 15% R. G.	---
6	Net plot area for development (4)	1475.54
7	Built up area due to area of land handed over as per regulation 30 (A) (6.16 x 2) = 12.32	12.32
8	a) Additional Premium FSI	737.77
b	Additional built-up area in the lieu of internal road area as per layout	---
c	Additional built-up area in the lieu of D. P. road area as per layout	---
d	Built up area due to "Additional F. S. I." as per Regulation No. 33 (7) (B) on remaining / balance plot. (x x tene = sq.mt.)	---
9	Permissible TDR	
i	General	1062.39
ii	Slum	265.60
iii	Road	---
iv	Permissible BUA (7 + 8 + 9)	3553.62
10	Proposed BUA	3553.62
11	Residential Rehab	---
	Residential Sale	---
	Non Residential Rehab	---
	Non Residential Sale	---
12	Fungible BUA	
a	Permissible fungible BUA without premium (Resi.)	---
ii	Availed fungible BUA without premium (Resi.)	---
b	Permissible fungible BUA without premium (NR)	---
iv	Availed fungible BUA without premium (NR)	---
c	v Permissible fungible BUA by charging premium (Resi.)	1064.36
vi	Availed fungible BUA by charging premium (Resi.)	1059.56
d	vii Permissible fungible BUA by charging premium (NR)	179.41
viii	Availed fungible BUA by charging premium (NR)	179.41
Total		1243.77
13	Total Gross BUA PERMISSIBLE (11 + 12)	4797.39
Total Gross BUA PROPOSED		4792.83
D) Tenement Statement		
i	Proposed Built up area (13 above)	4792.83
ii	Less deduction of Non-residential area (Shop etc.)	692.55
iii	Area available for tenements [(i) - (ii)]	4100.28
iv	Tenements permissible (Density of tenements / hectare)	185 Nos.
v	Total number of Tenements proposed on the plot	49 Nos.
E) Parking Statement		
i	Parking required by Regulation for	79 Nos.
	Car	---
	Scooter / Motor cycle	---
	Outsiders (visitors)	---
ii	Covered garage permissible	---
iii	Covered garage proposed	---
	Car	---
	Scooter / Motor cycle	---
	Outsiders (visitors)	---
iv	Total parking provided	79 Nos.
F) Transport Vehicles Parking		
i	Space for transport vehicles parking required by Regulation	---
ii	Total No. of transport vehicles parking spaces provided	---

PROFORMA-B

CONTENT OF SHEET

GROUND FLOOR PLAN, BUILT-UP AREA CALCULATION OF GR. FLOOR, BUILT-UP AREA SUMMARY, PARKING STATEMENT, BLOCK PLAN & LOCATION PLAN

STAMP OF APPROVAL OF PLAN

D. F. O.

DY. C. F. O.

CERTIFICATE OF AREA

CERTIFIED THAT THE I HAVE SURVEYED THE PLOT UNDER REFERENCE ON AND THAT THE DIMENSION OF THE SIDE ETC OF PLOT STATED ON THE PLOT ARE AS MEASURED ON SITE AND THE AREA SO WORKED OUT IS 1481.70 SQ. MT. AND TALLIES WITH IS MORE THAN THE AREA STATED IN THE DOCUMENT OF OWNERSHIP, TOWN PLANNING SCHEME RECORD.

Ashish Narendra Bhatt

SIGNATURE OF L. S.

DESCRIPTION OF PROPOSAL

PROPOSED DEVELOPMENT ON PLOT BEARING C. T. S. NO. 1386 OF MULUND (W), AT JUNCTION OF J. N. ROAD & WALJI LADHA ROAD, MUMBAI.

NAME OF OWNER

SIGNATURE

MULUND HANSA VILLA CO.OP. HSG LTD.

MANISH HIMATLAL HALARI

JOB No.

DRG. No.

DATE

DRN. BY

CHK. BY

REVISION

1/4

SHASHI

ASHISH


NAME SIGN. & ADD. OF L. S.

SIGNATURE

ASHISH BHATT

802, 8TH FLOOR, VIKAS CENTRE, JUNCTION OF N. S. B. ROAD & S. L. ROAD, MULUND (WEST) MUMBAI - 400080.


Ashish Narendra Bhatt

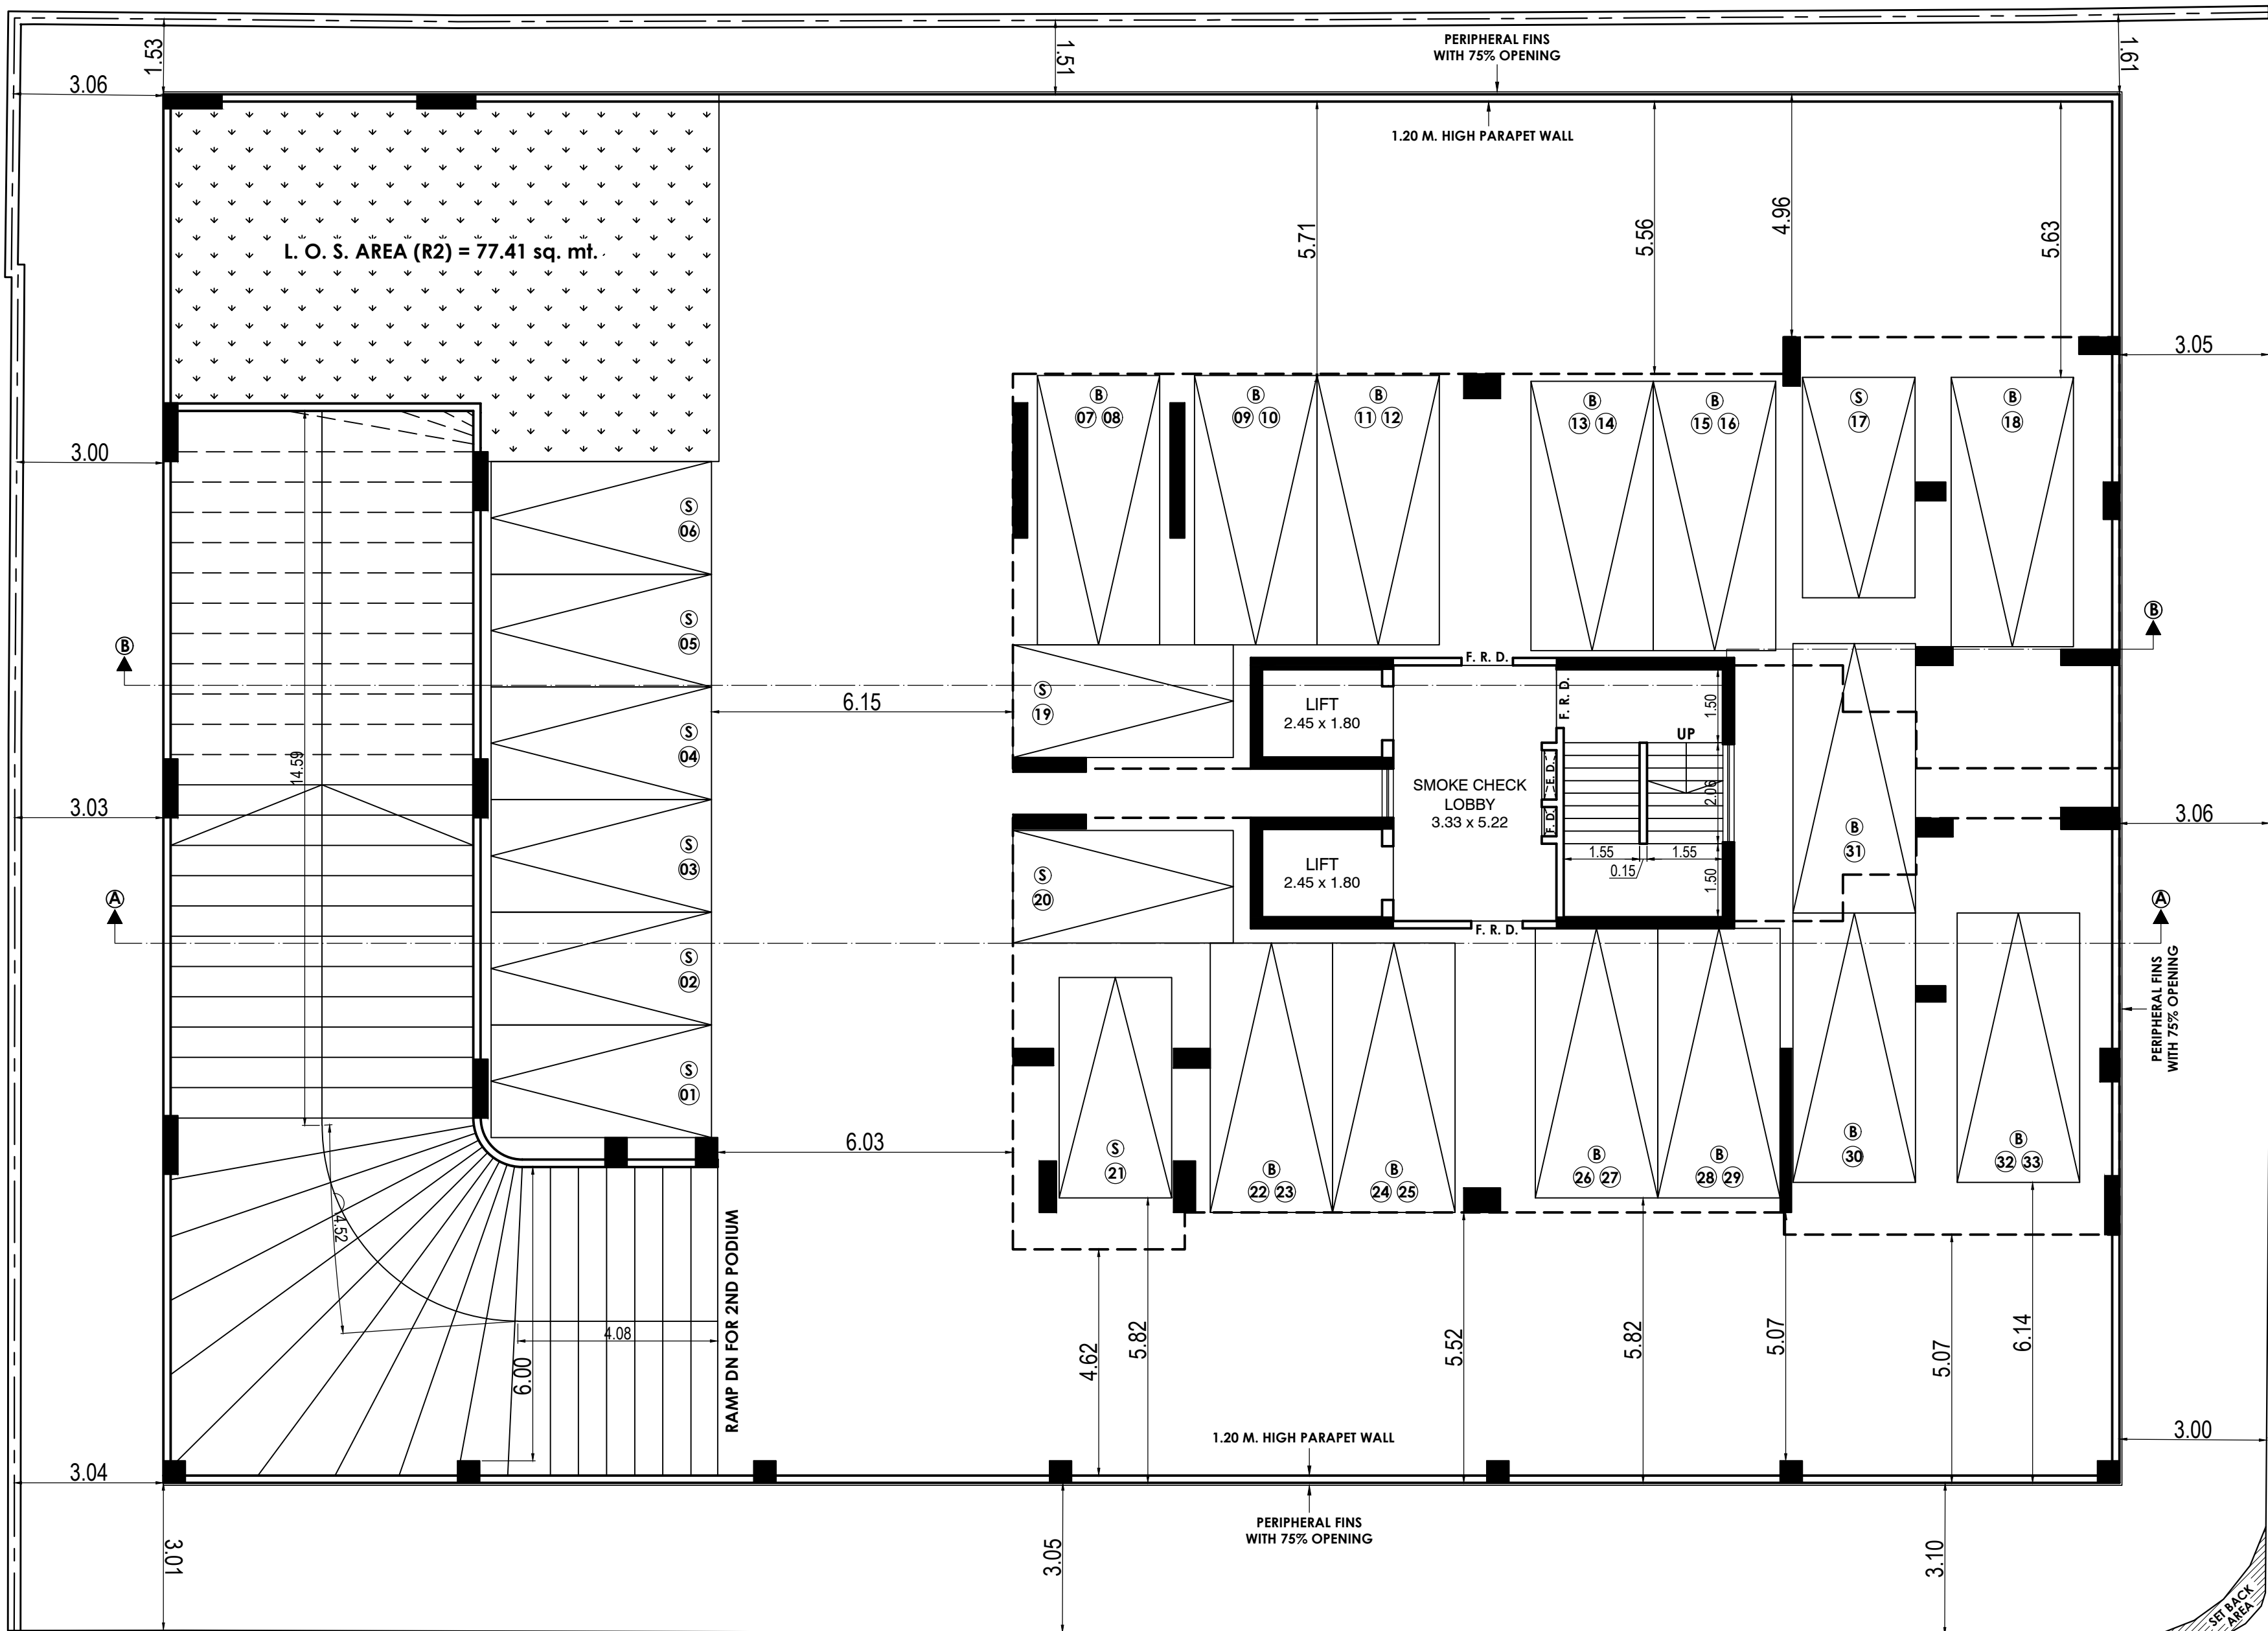

3RD PODIUM FLOOR PLAN
SCALE :- 1:100

CARPET AREA STATEMNT FOR PARKING PURPOSE ONLY


FLOORS	SHOP Nos.															
	1 & 2	3	4	5	6	7	8	9	10	11	12	13	14	15	16	17
GR. FLR.	186.09	31.19	31.17	30.46	30.45	30.43	32.04	31.87	31.84	30.15	30.03	29.72	30.90	24.29	30.49	30.45

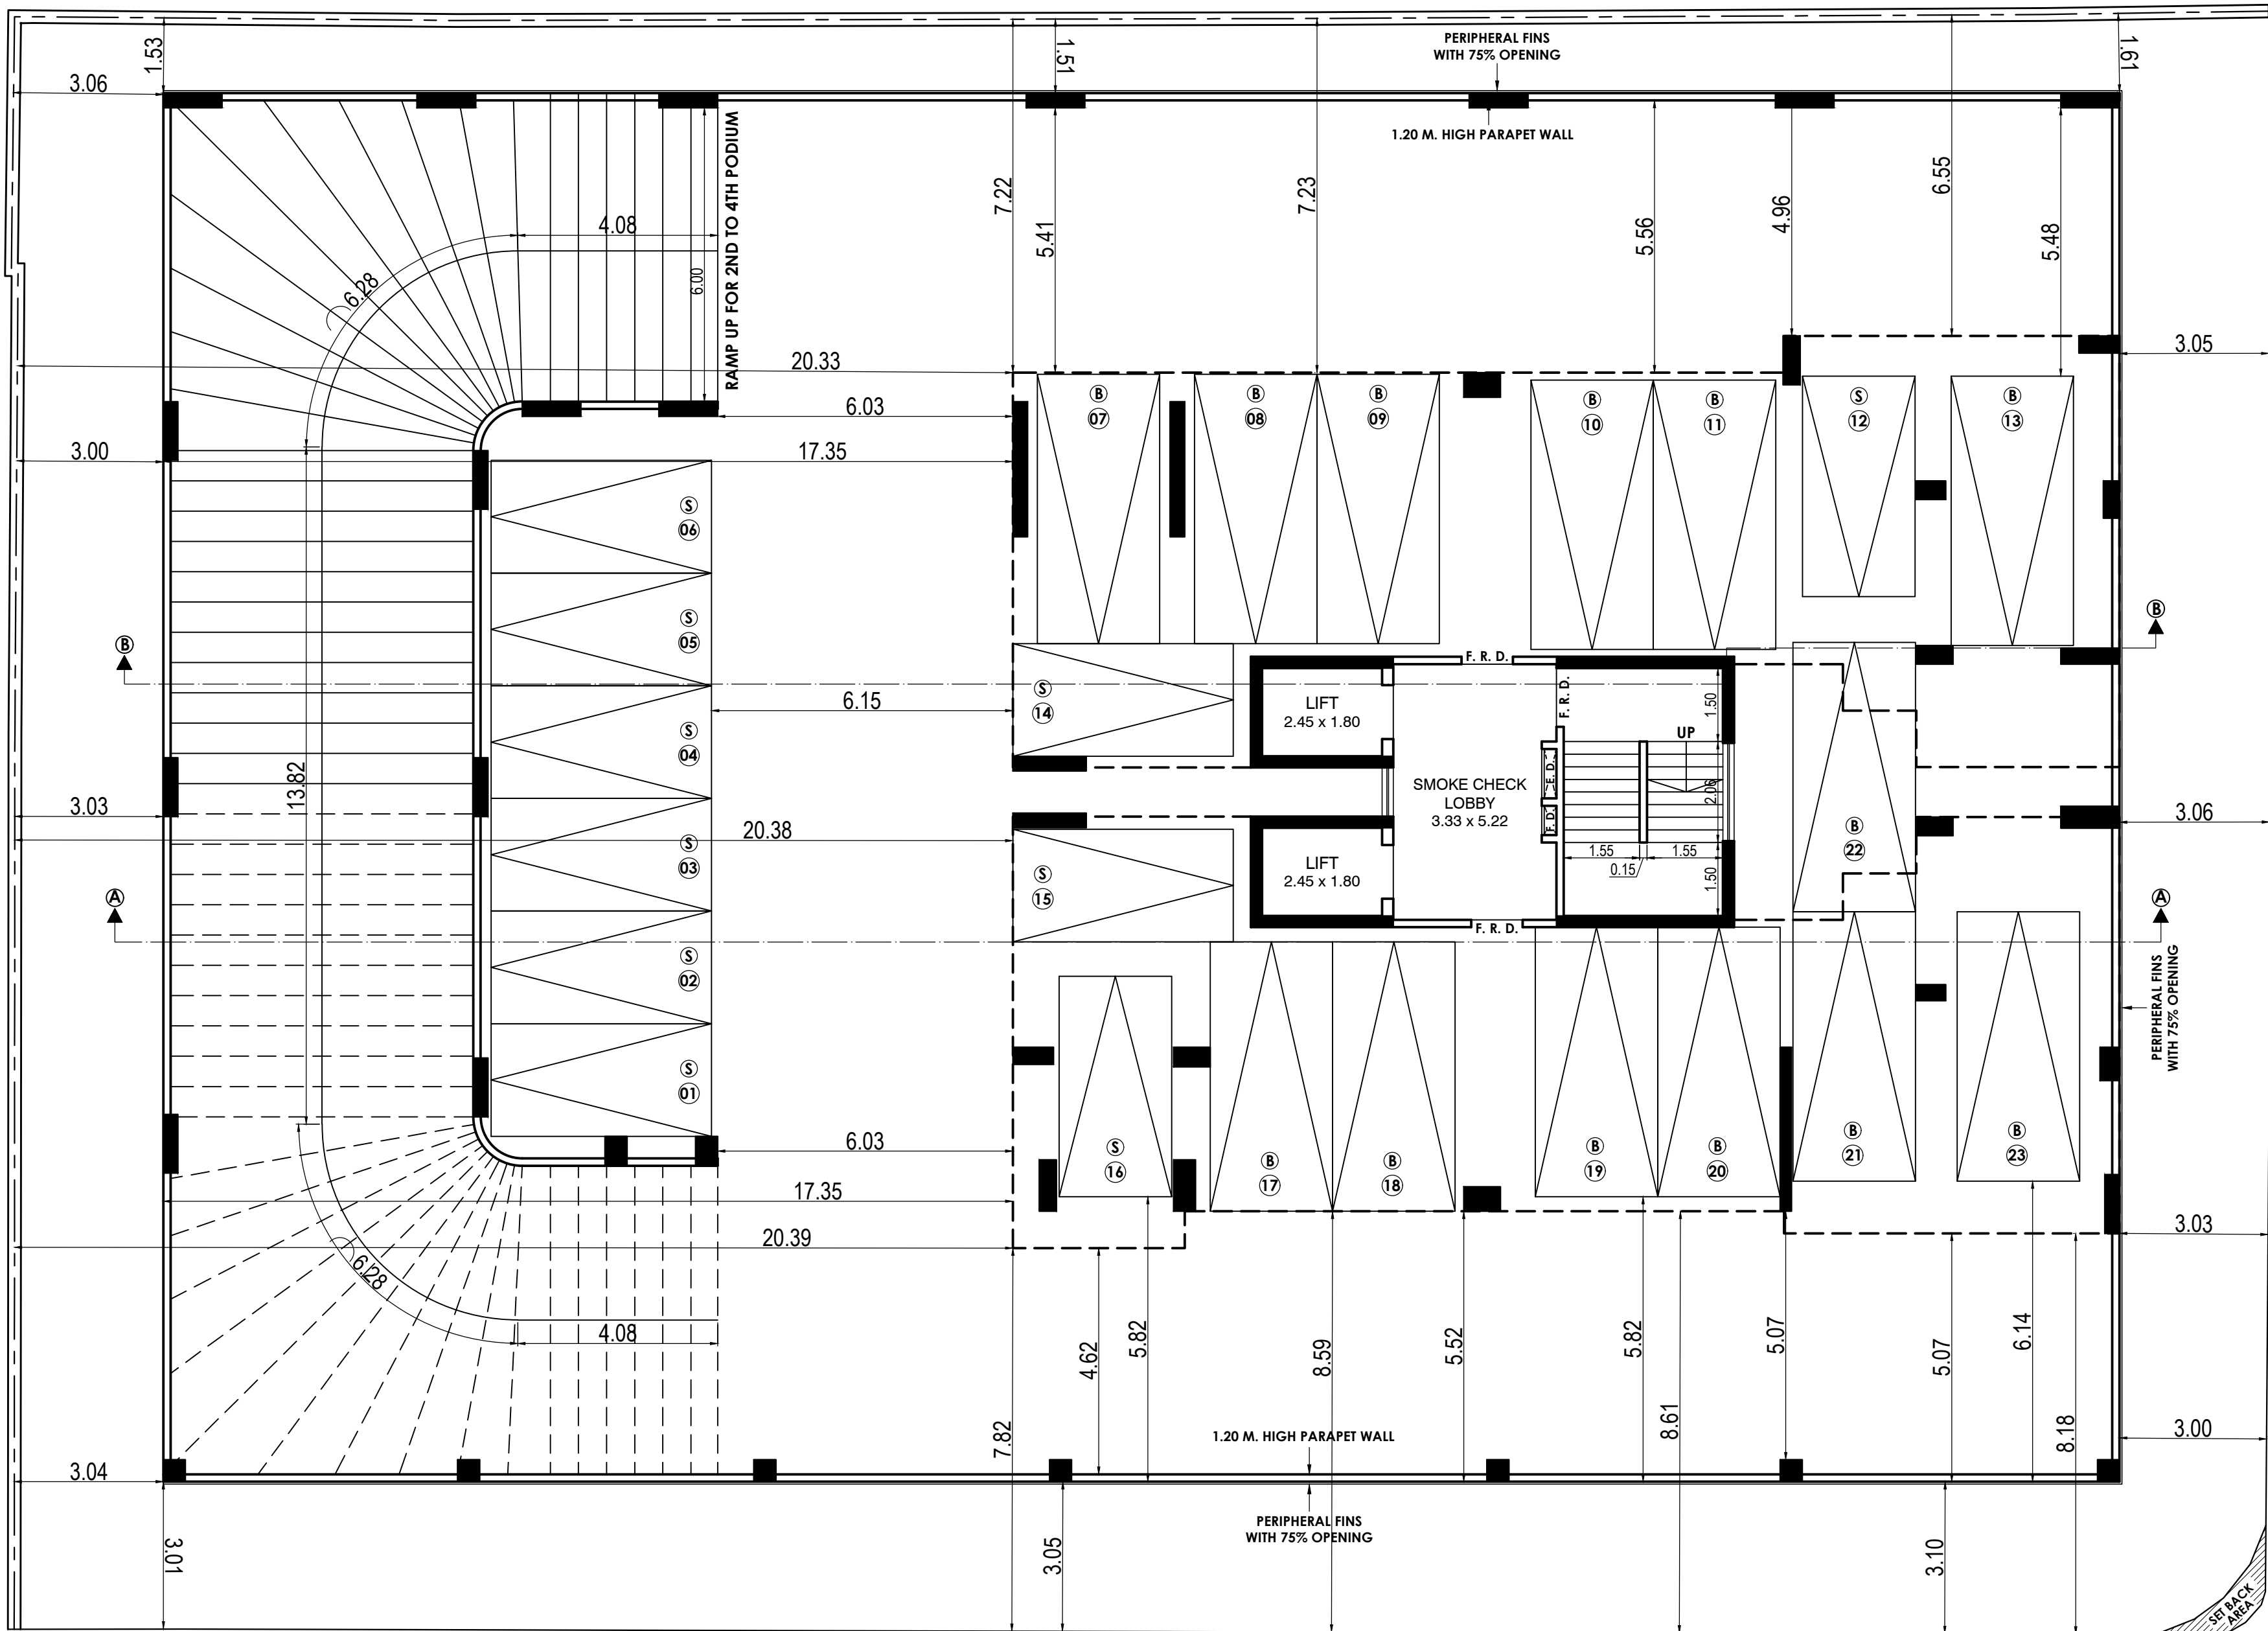


1ST & 2ND PODIUM FLOOR PLAN
SCALE :- 1:100

FLOORS	FLAT Nos.			
	1	2	3	4
4TH FLR.	84.79	64.68	63.04	87.61
5TH FLR.	88.16	64.68	63.04	87.61
6TH FLR.	88.16	64.68	63.04	87.61
7TH FLR.	REFUGE	64.68	64.54	87.61
8TH FLR.	88.16	64.68	64.54	87.61
9TH FLR.	88.16	64.68	64.54	87.61
10TH FLR.	100.18	64.68	64.54	87.61
11TH FLR.	100.18	64.68	64.54	87.61
12TH FLR.	100.18	64.68	64.54	87.61
13TH FLR.	100.18	64.68	64.54	87.61
14TH FLR.	110.85	REFUGE	64.54	87.61
15TH FLR.	100.18	64.68	64.54	87.61
16TH FLR.	100.18	64.68	64.54	FITNESS


PROFORMA-B					
CONTENT OF SHEET					
1ST TO 3RD PODIUM FLOOR PLAN					
STAMP OF APPROVAL OF PLAN					
D. F. O. DY. C. F. O.					
DESCRIPTION OF PROPOSAL					
PROPOSED DEVELOPMENT ON PLOT BEARING C. T. S. NO. 1386 OF MULUND (W), AT JUNCTION OF J. N. ROAD & WALJI LADHA ROAD, MUMBAI.					
NAME OF OWNER			SIGNATURE		
MULUND HANSA VILLA CO.OP. HSG LTD.			MANISH HIMATLAL HALARI		
JOB No.	DRG. No.	DATE	DRN. BY	CHK. BY	REVISION
	2/4		SHASHI	ASHISH	
NAME SIGN. & ADD. OF L. S.			SIGNATURE		
ASHISH BHATT 802, 8TH FLOOR, VIKAS CENTRE, JUNCTION OF N. S. B. ROAD & S. L. ROAD, MULUND (WEST) MUMBAI - 400080.			Ashish Narendra Bhatt		

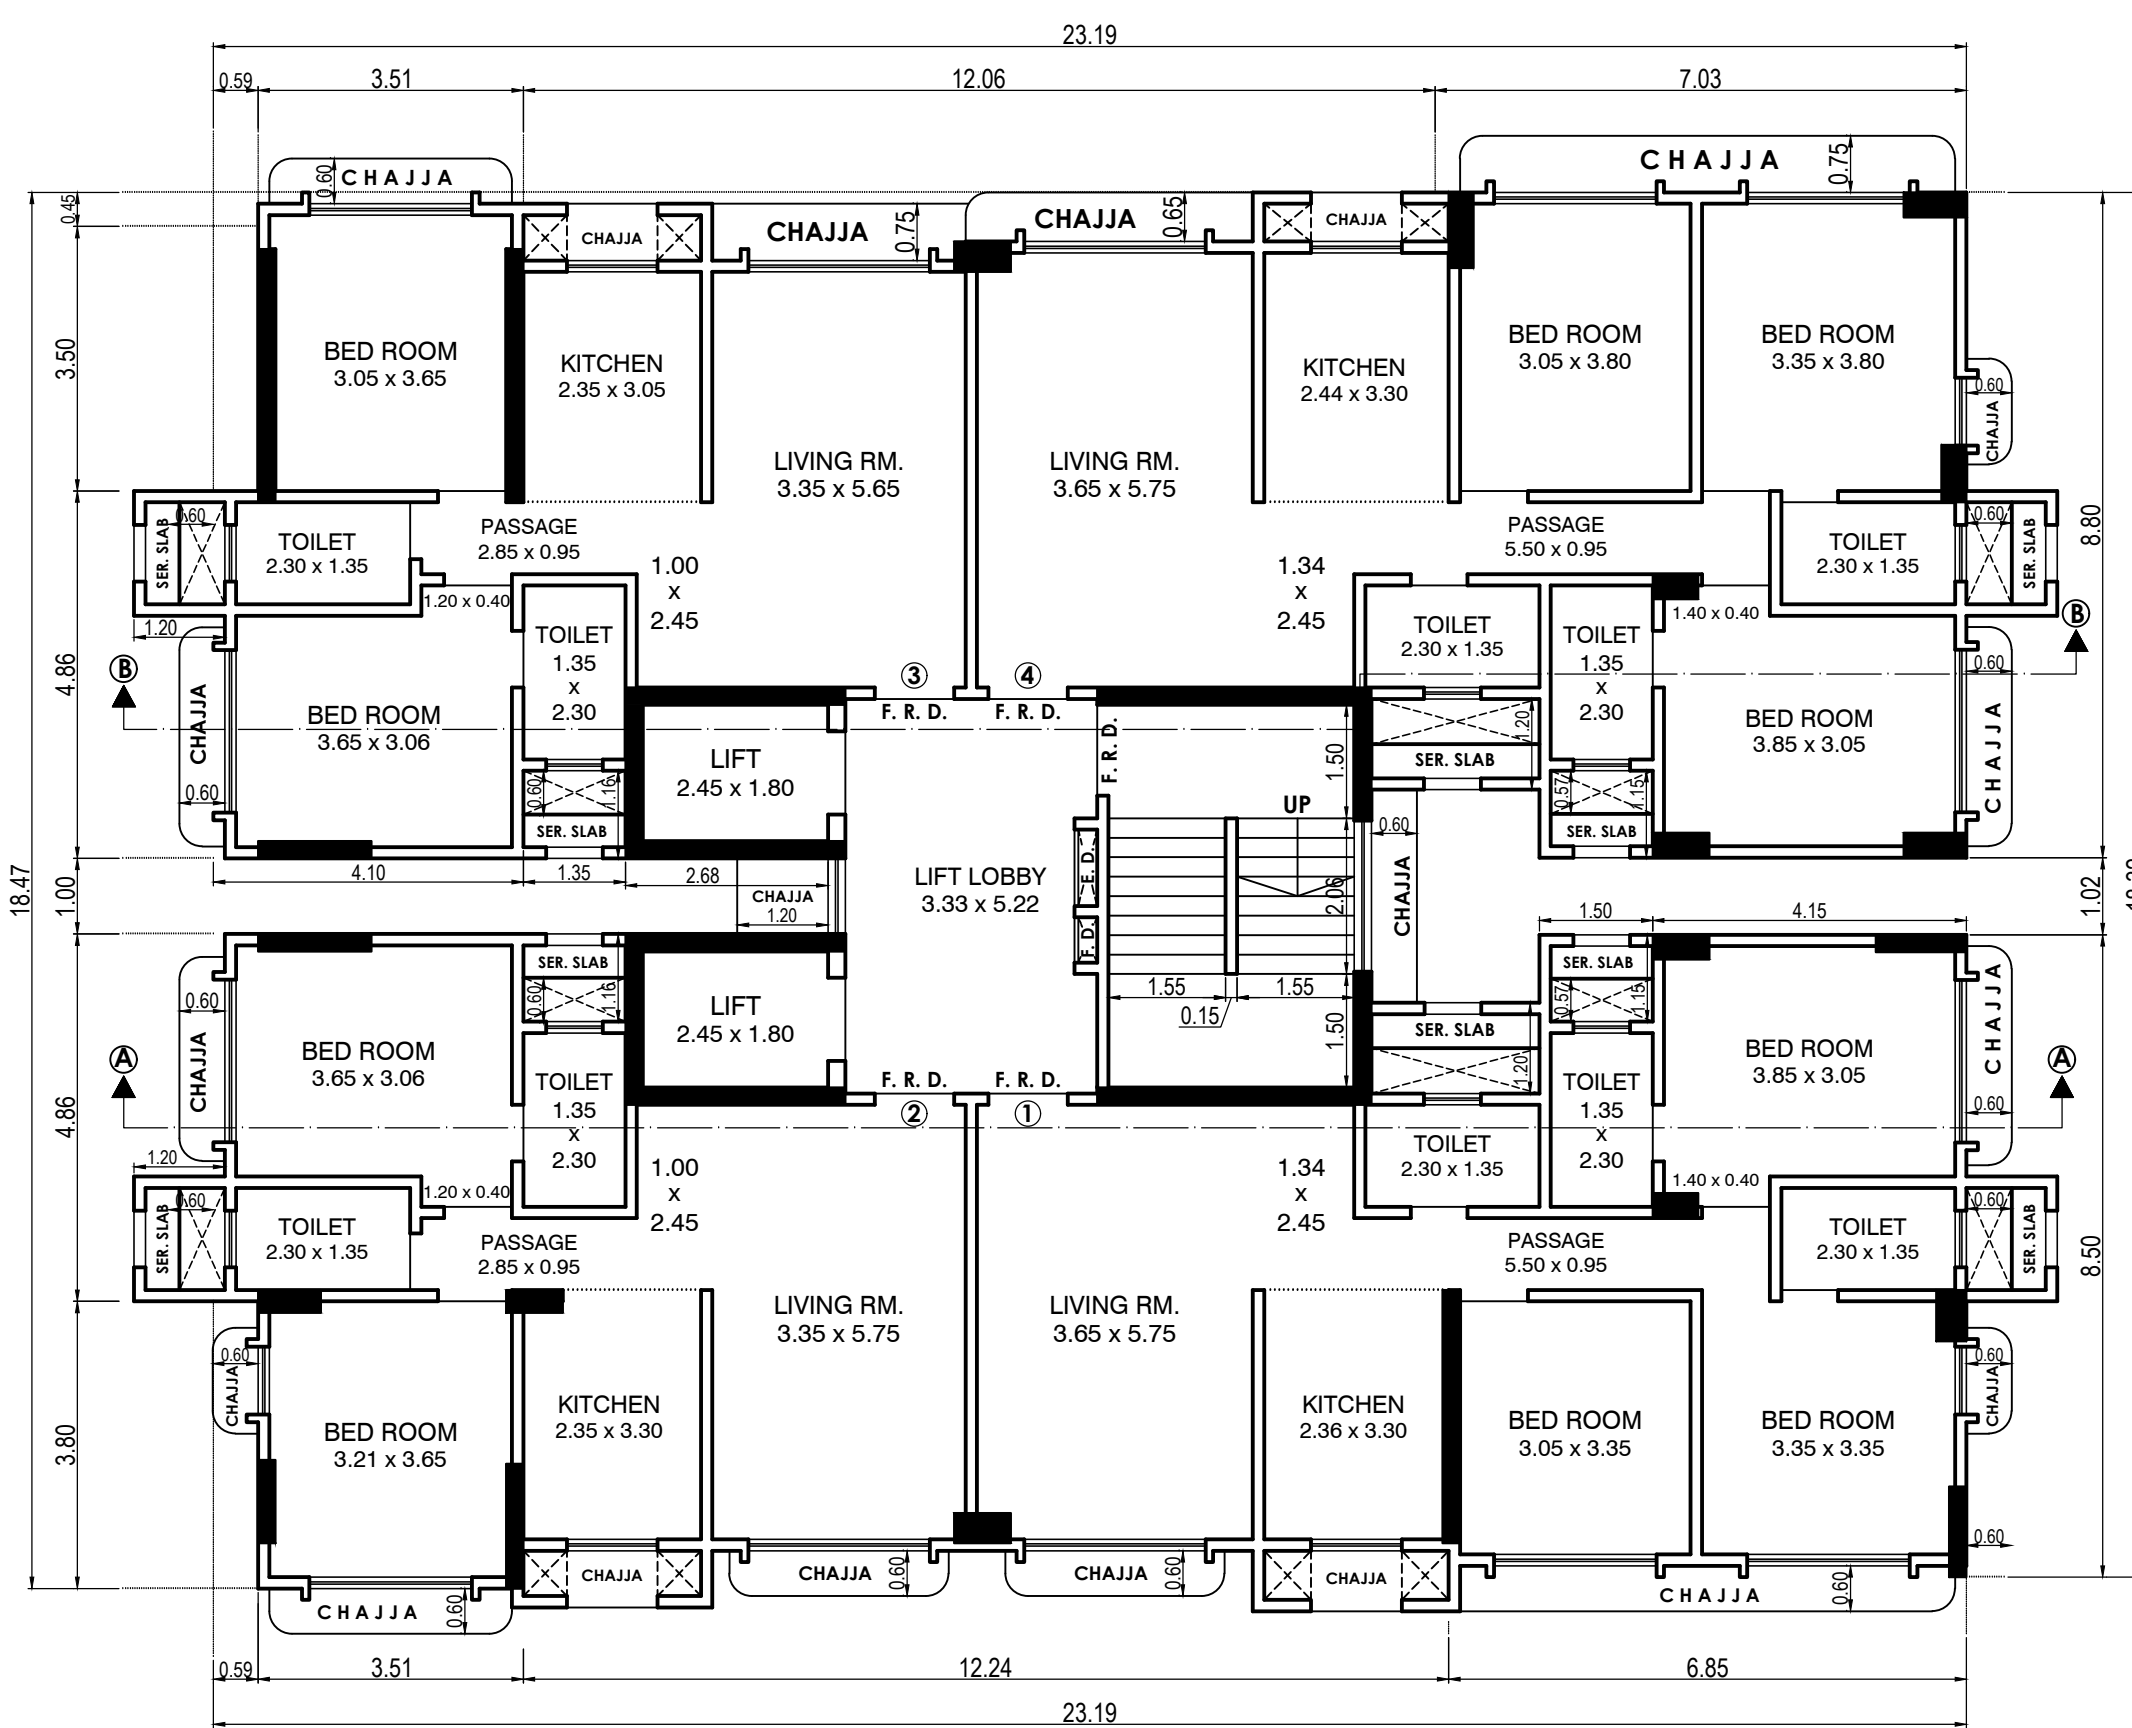


4TH FLOOR PLAN
SCALE :- 1:100

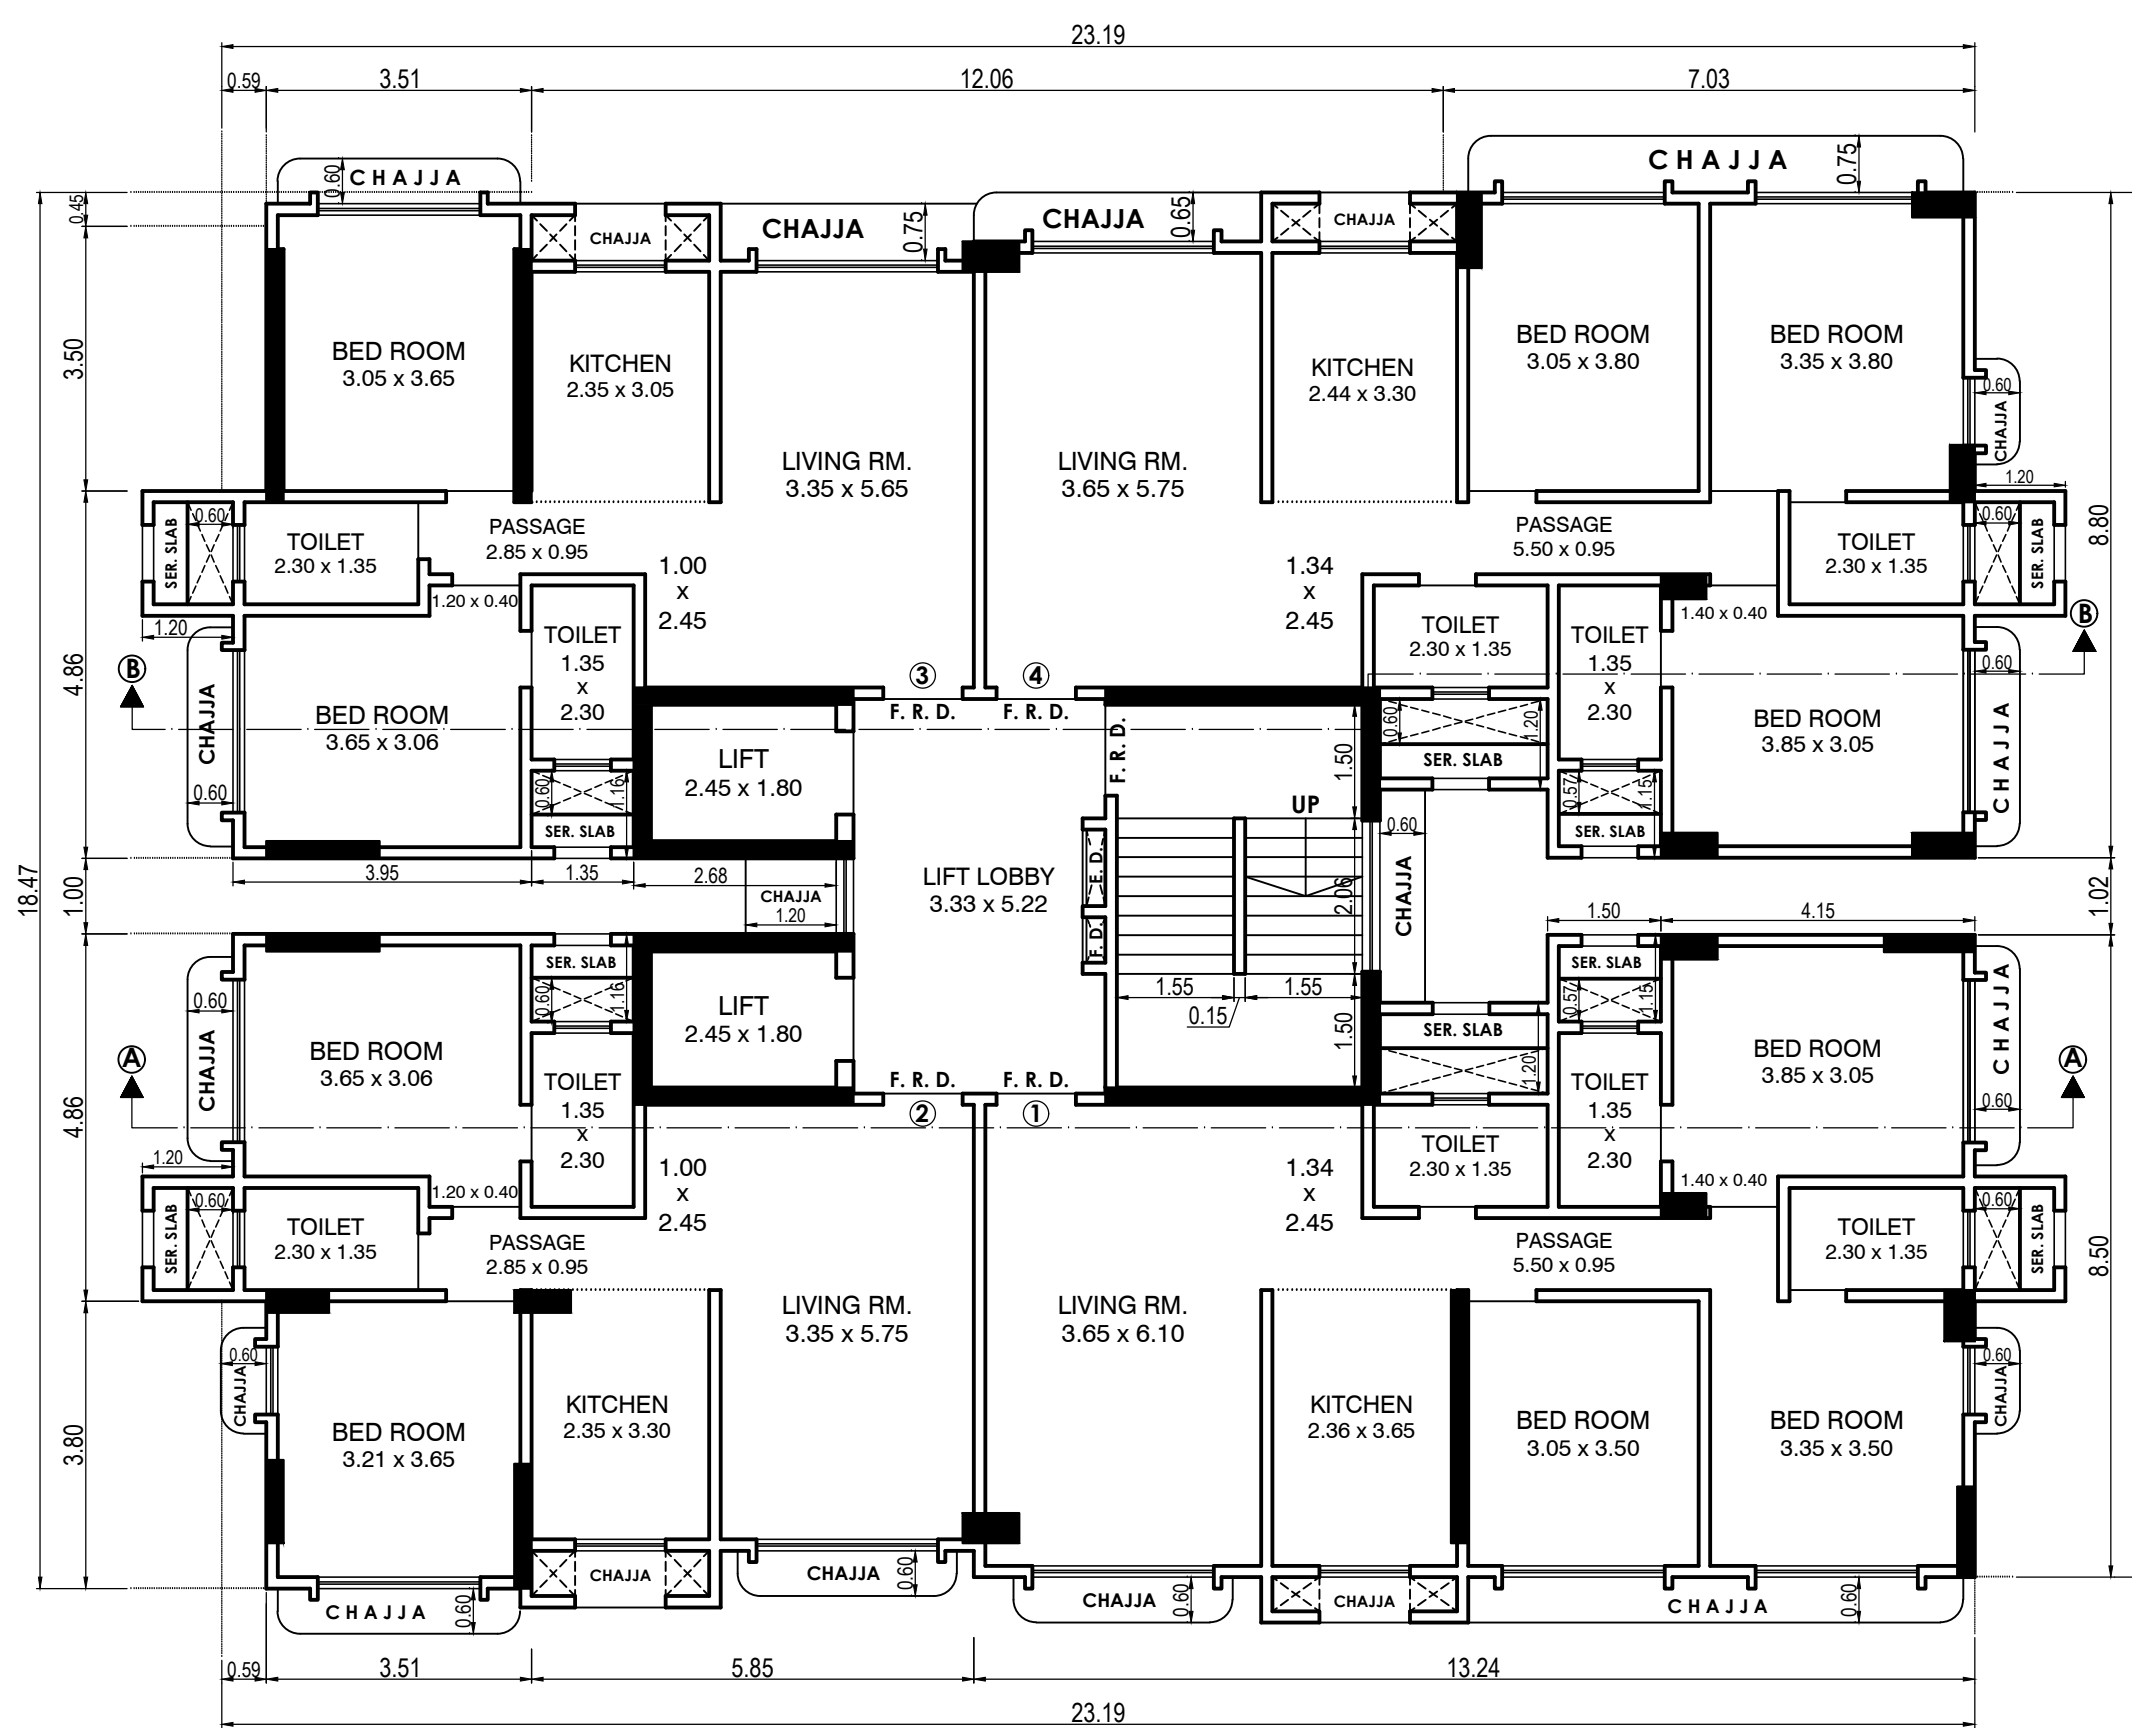


5TH & 6TH FLOOR PLAN
SCALE :- 1:100

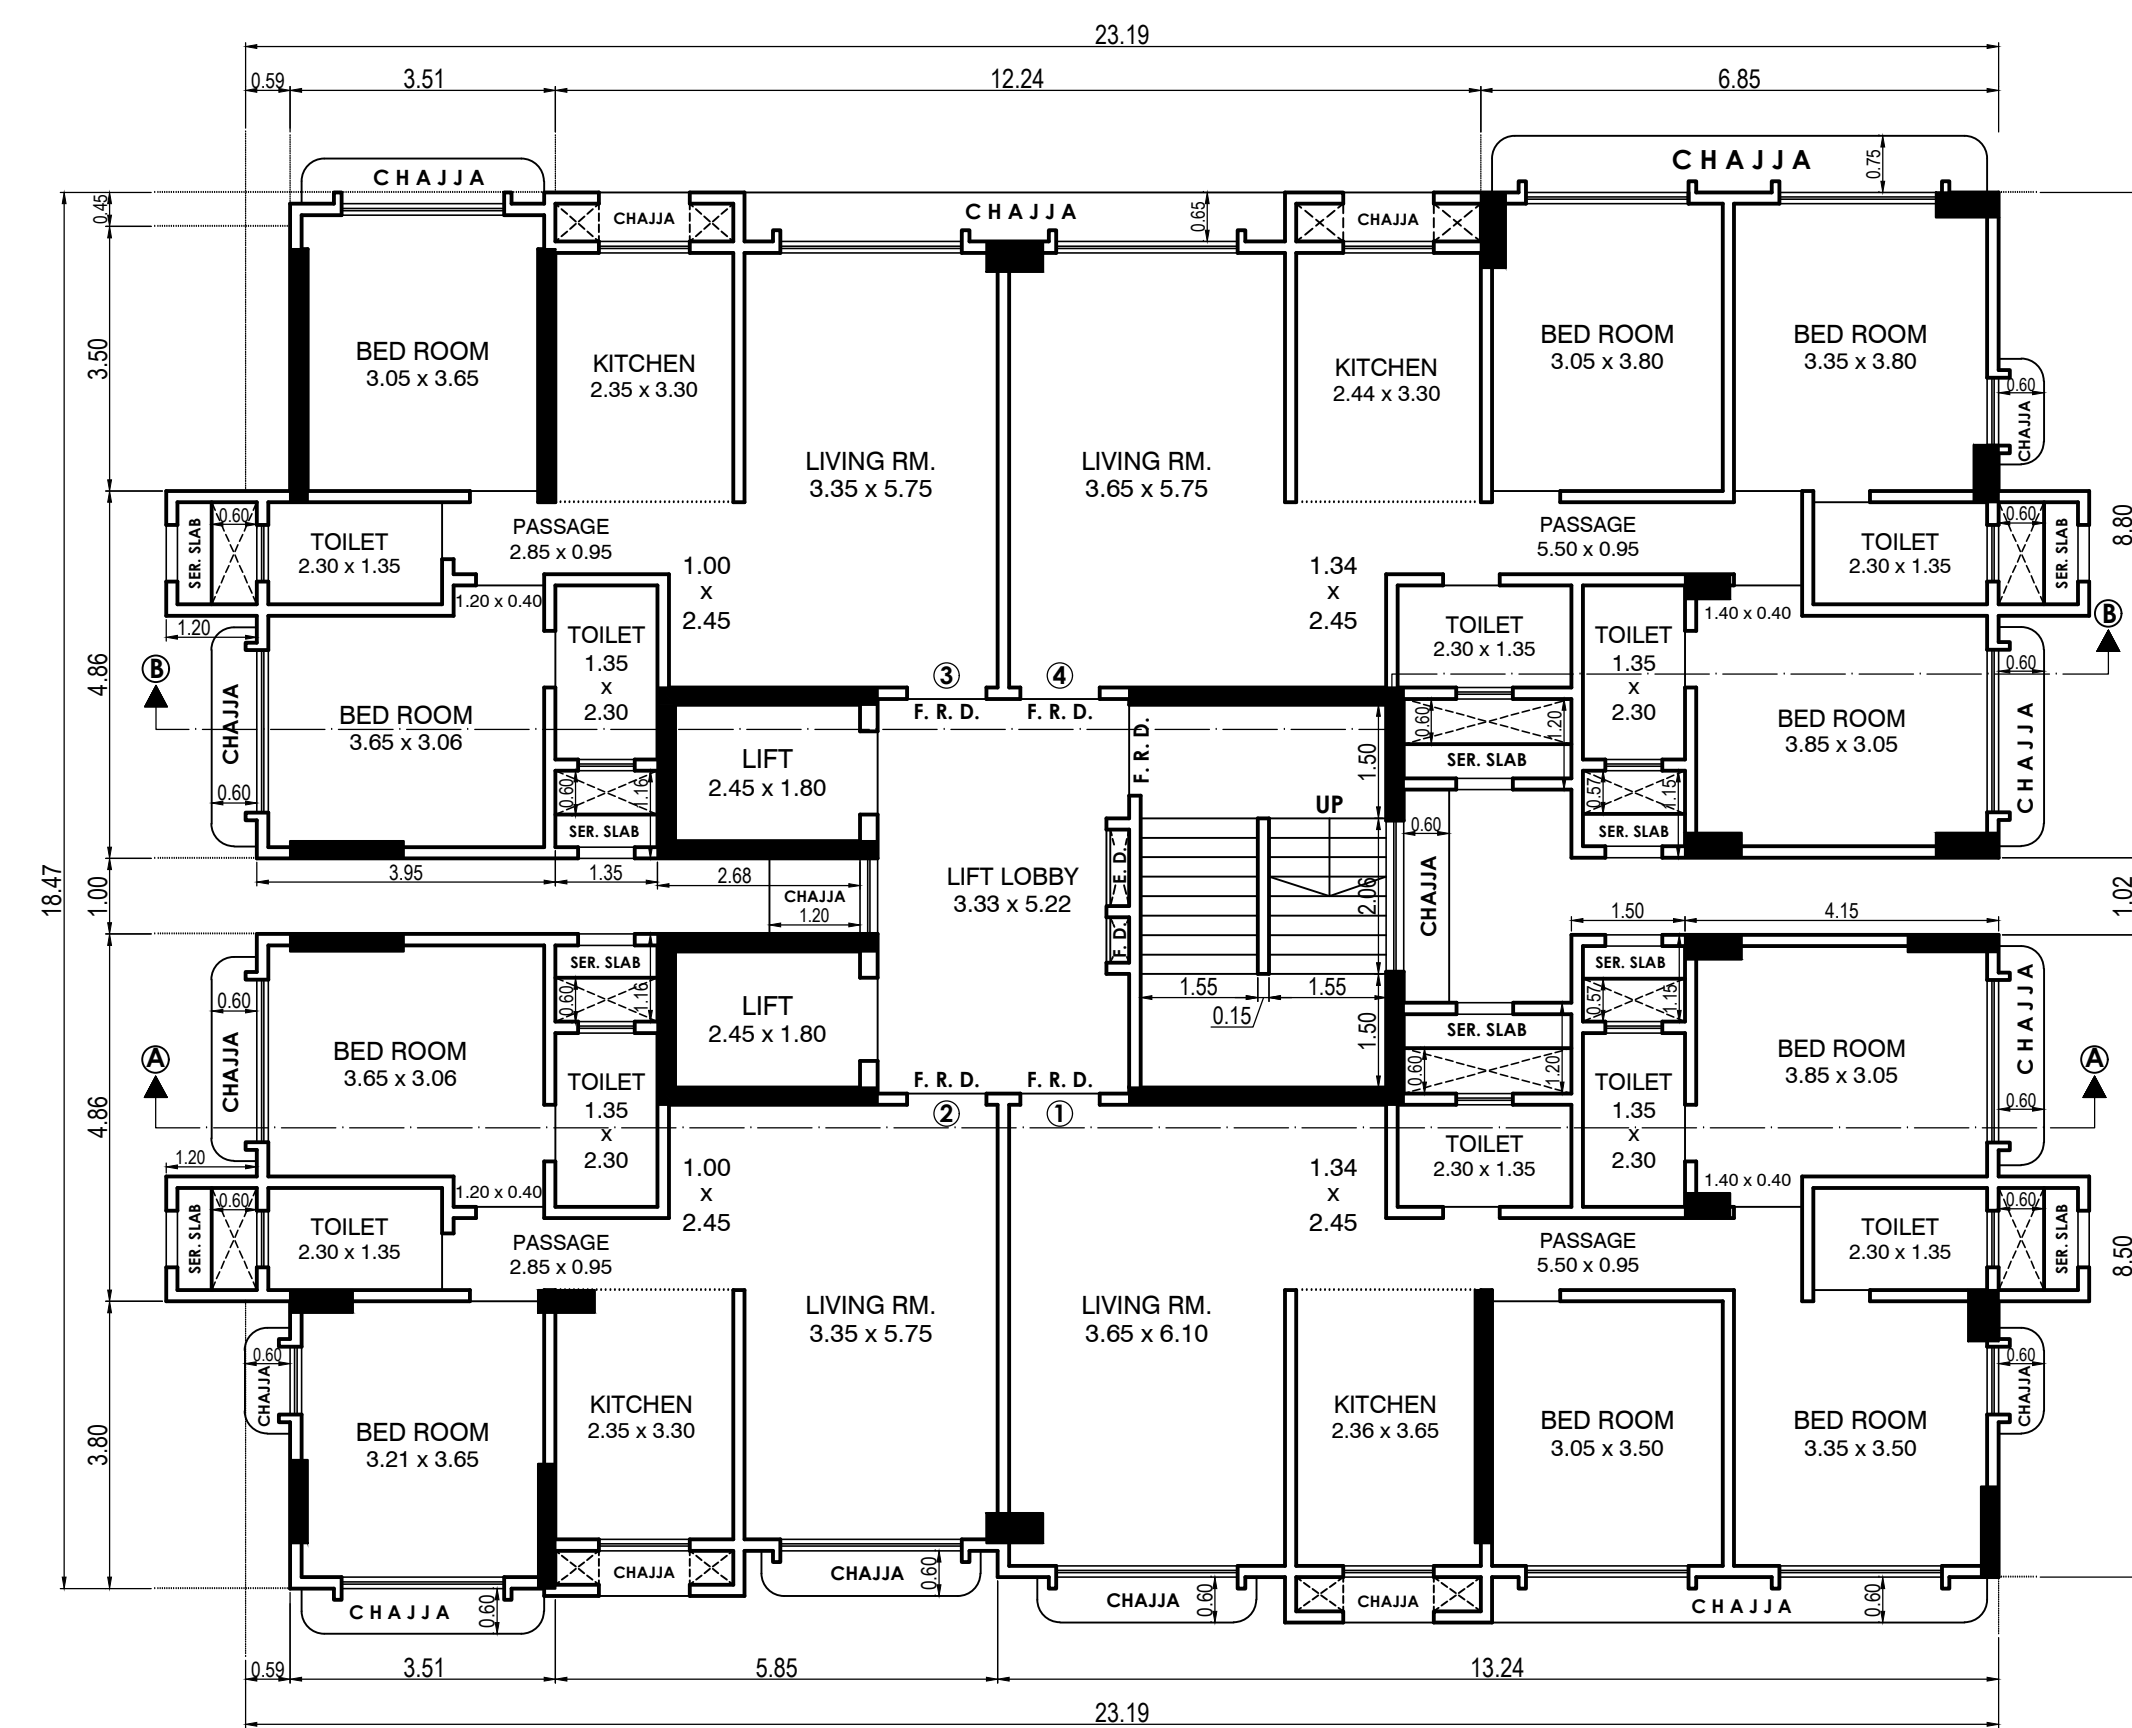


8TH & 9TH FLOOR PLAN
SCALE :- 1:100

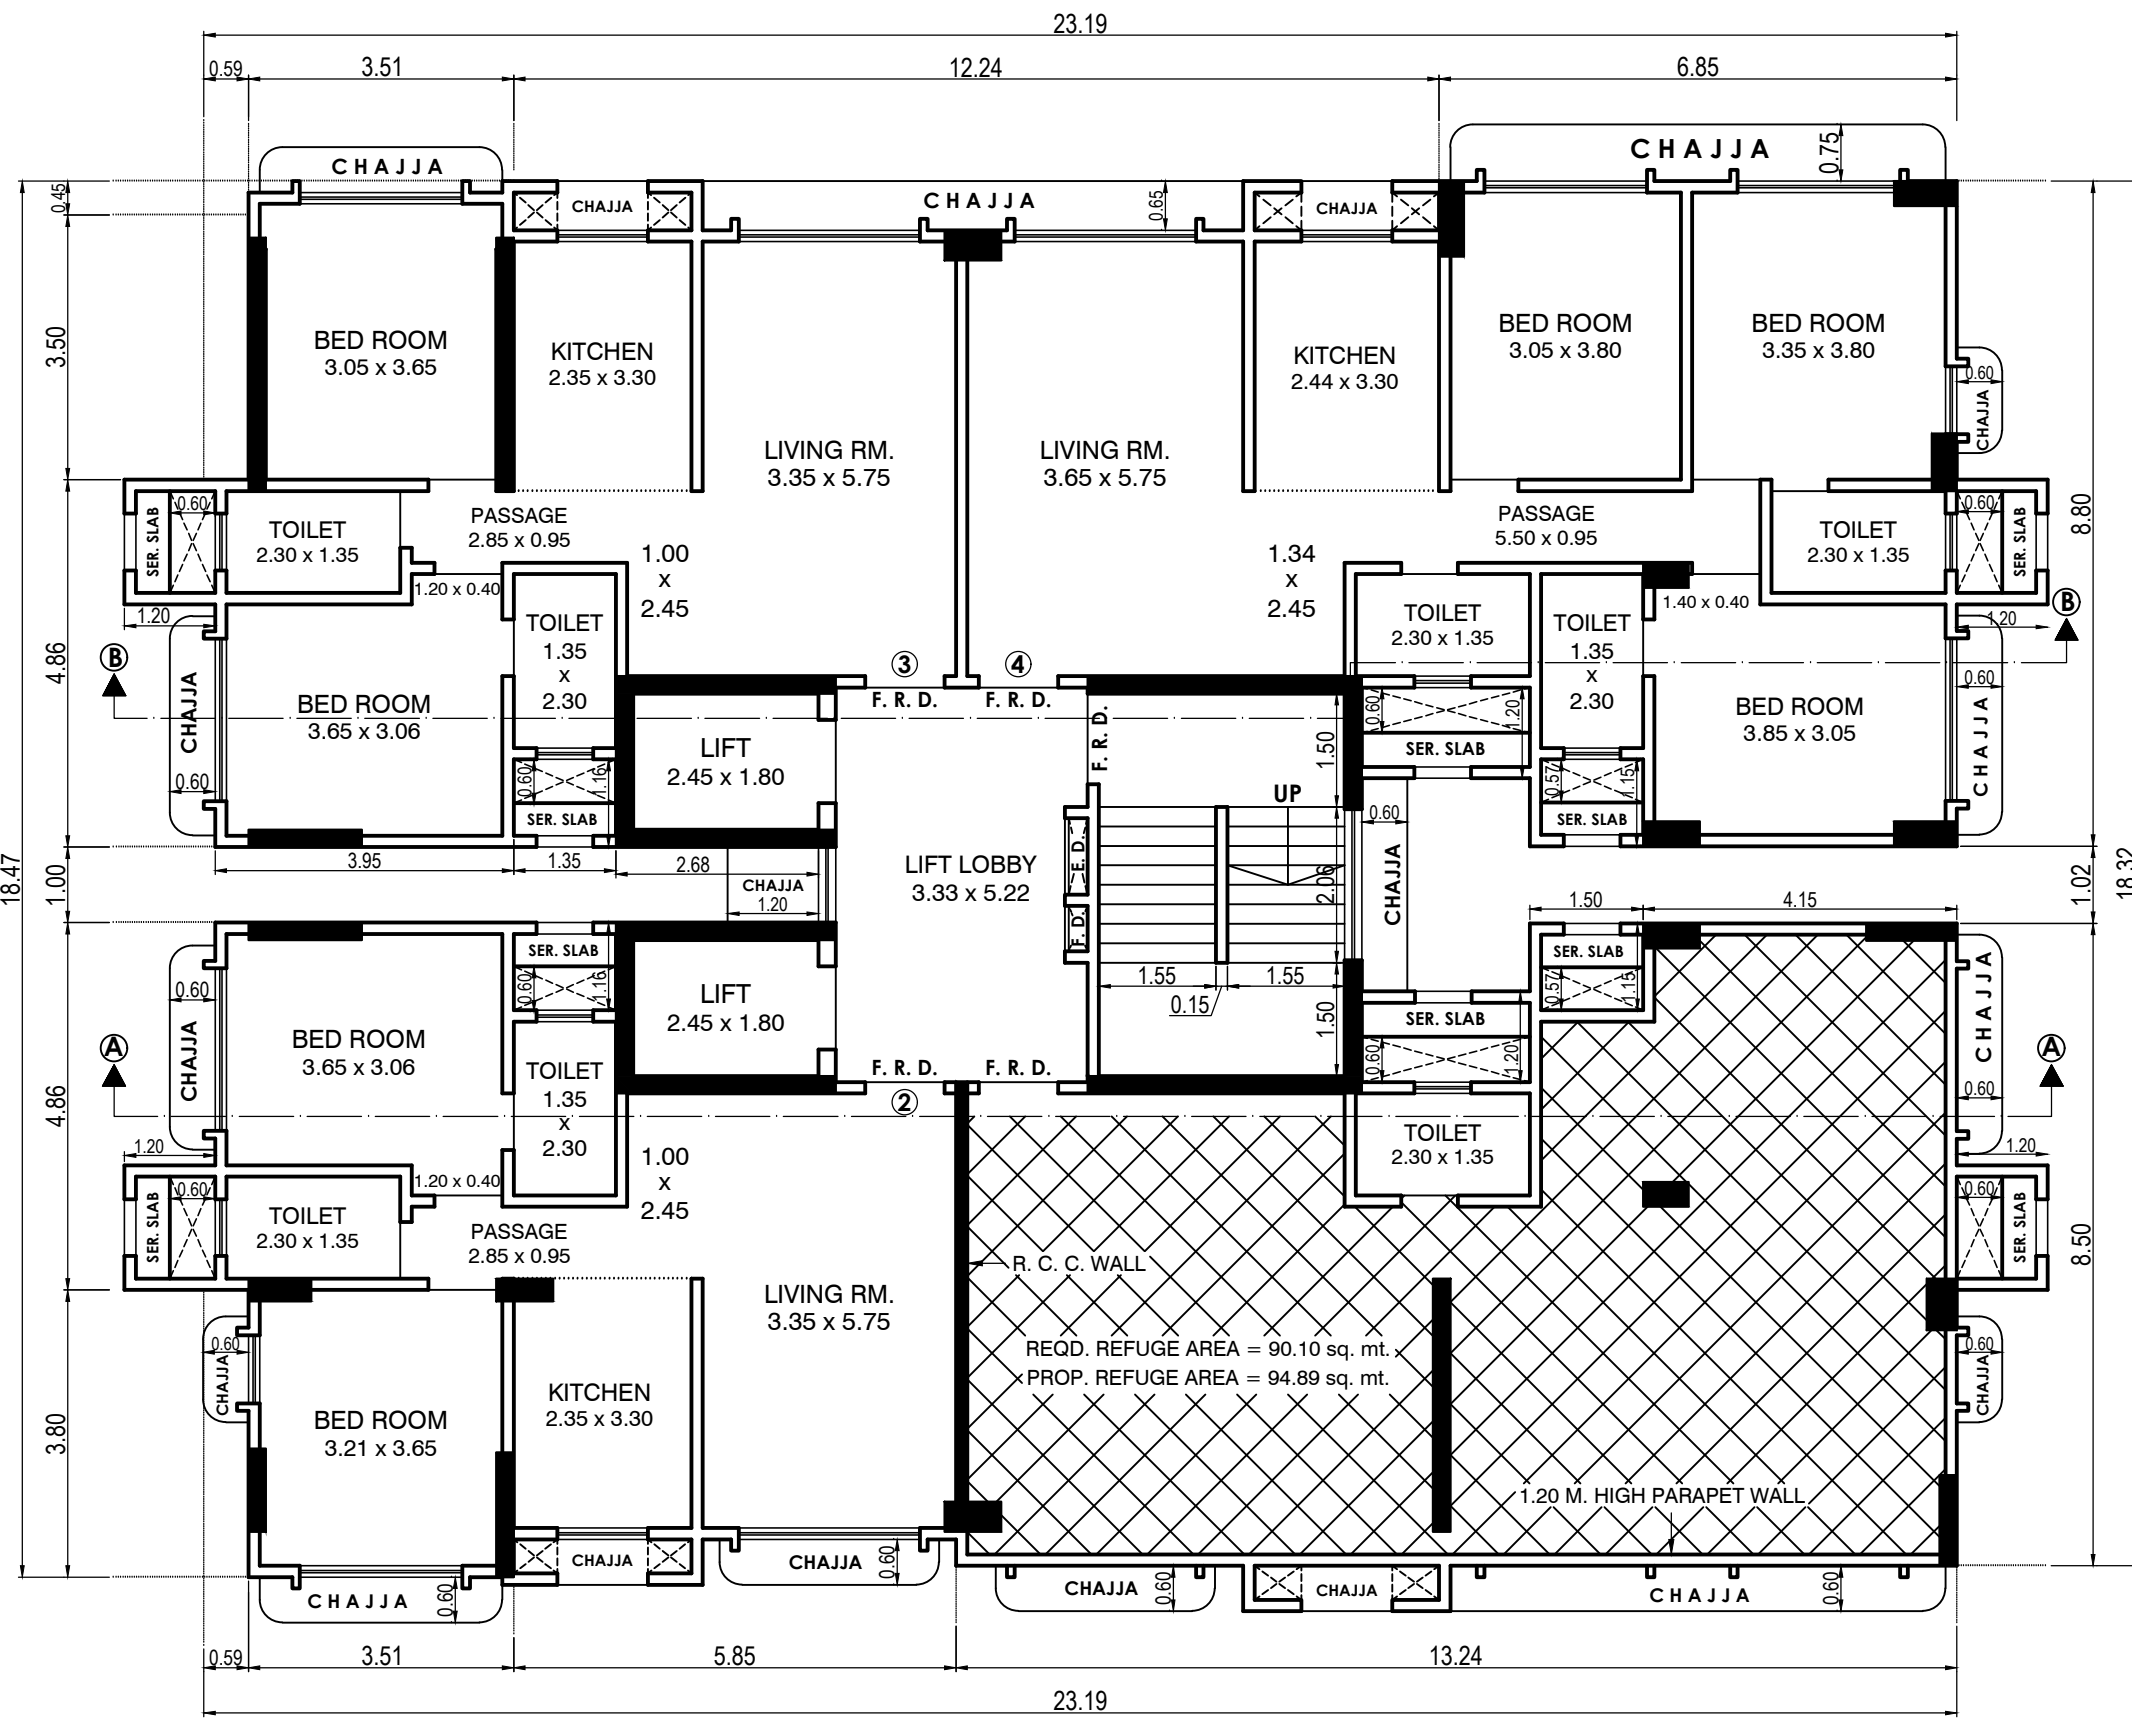


7TH FLOOR PLAN
SCALE :- 1:100

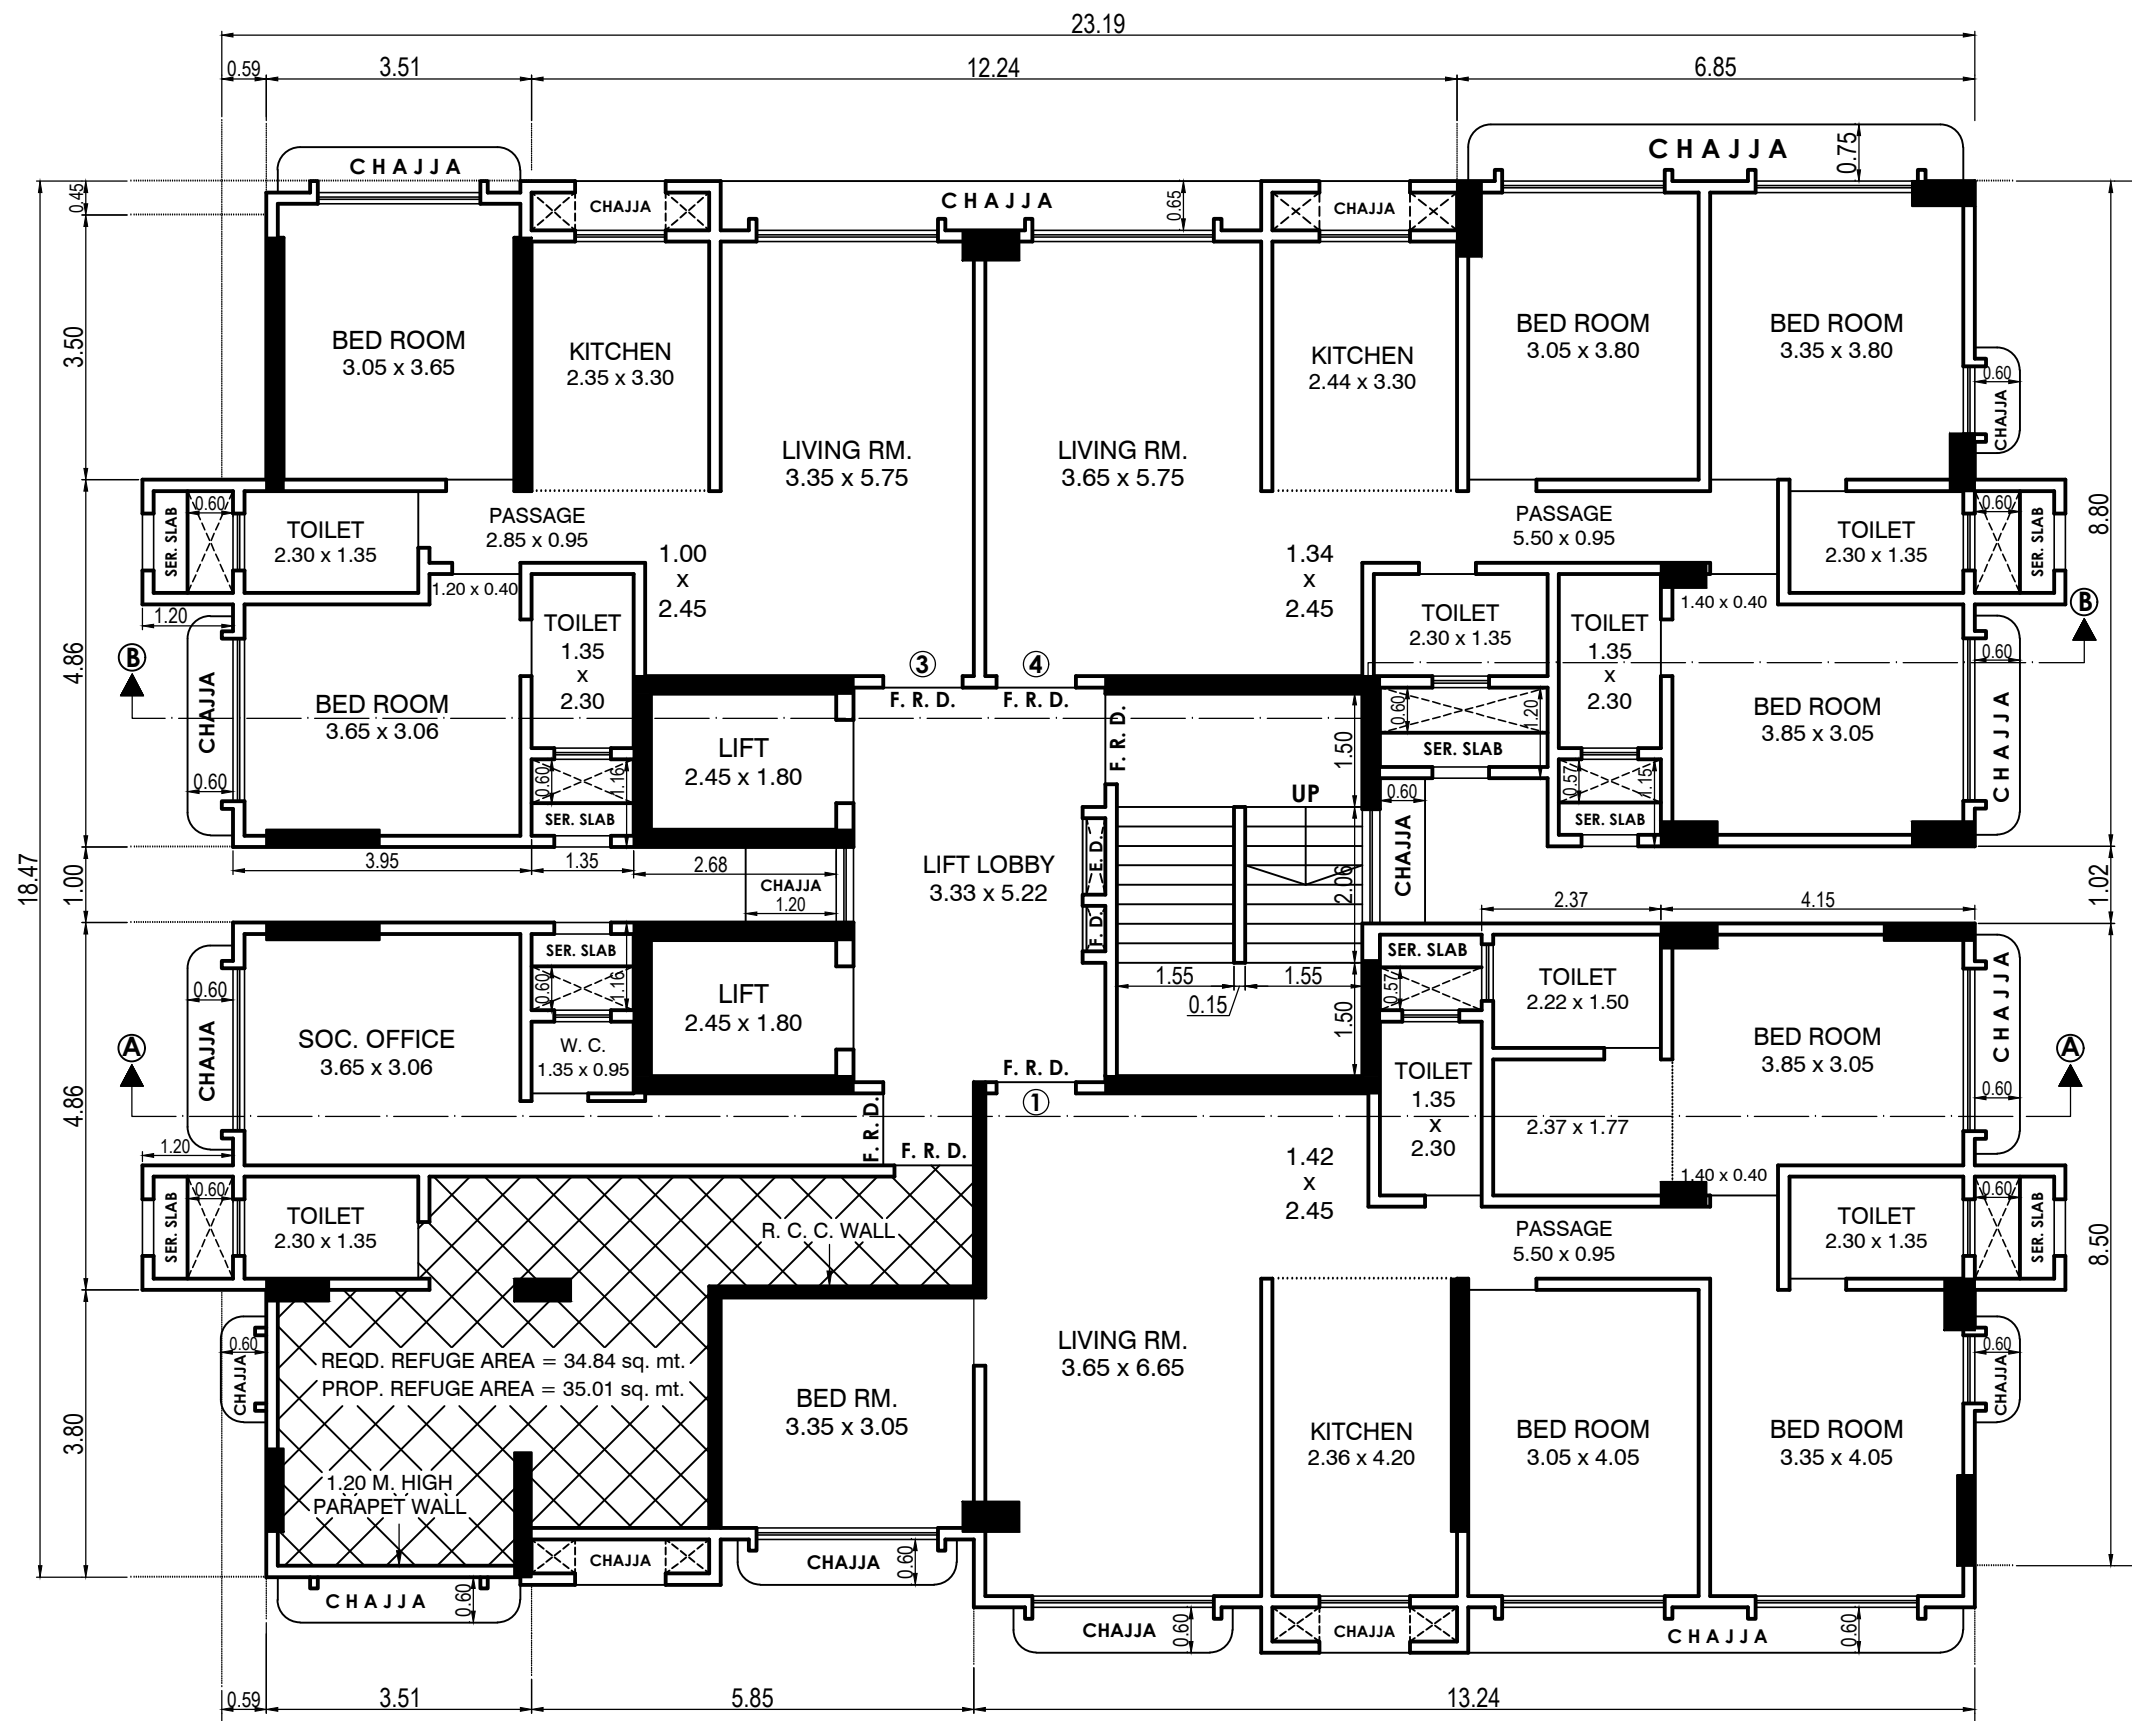


14TH FLOOR PLAN
SCALE :- 1:100

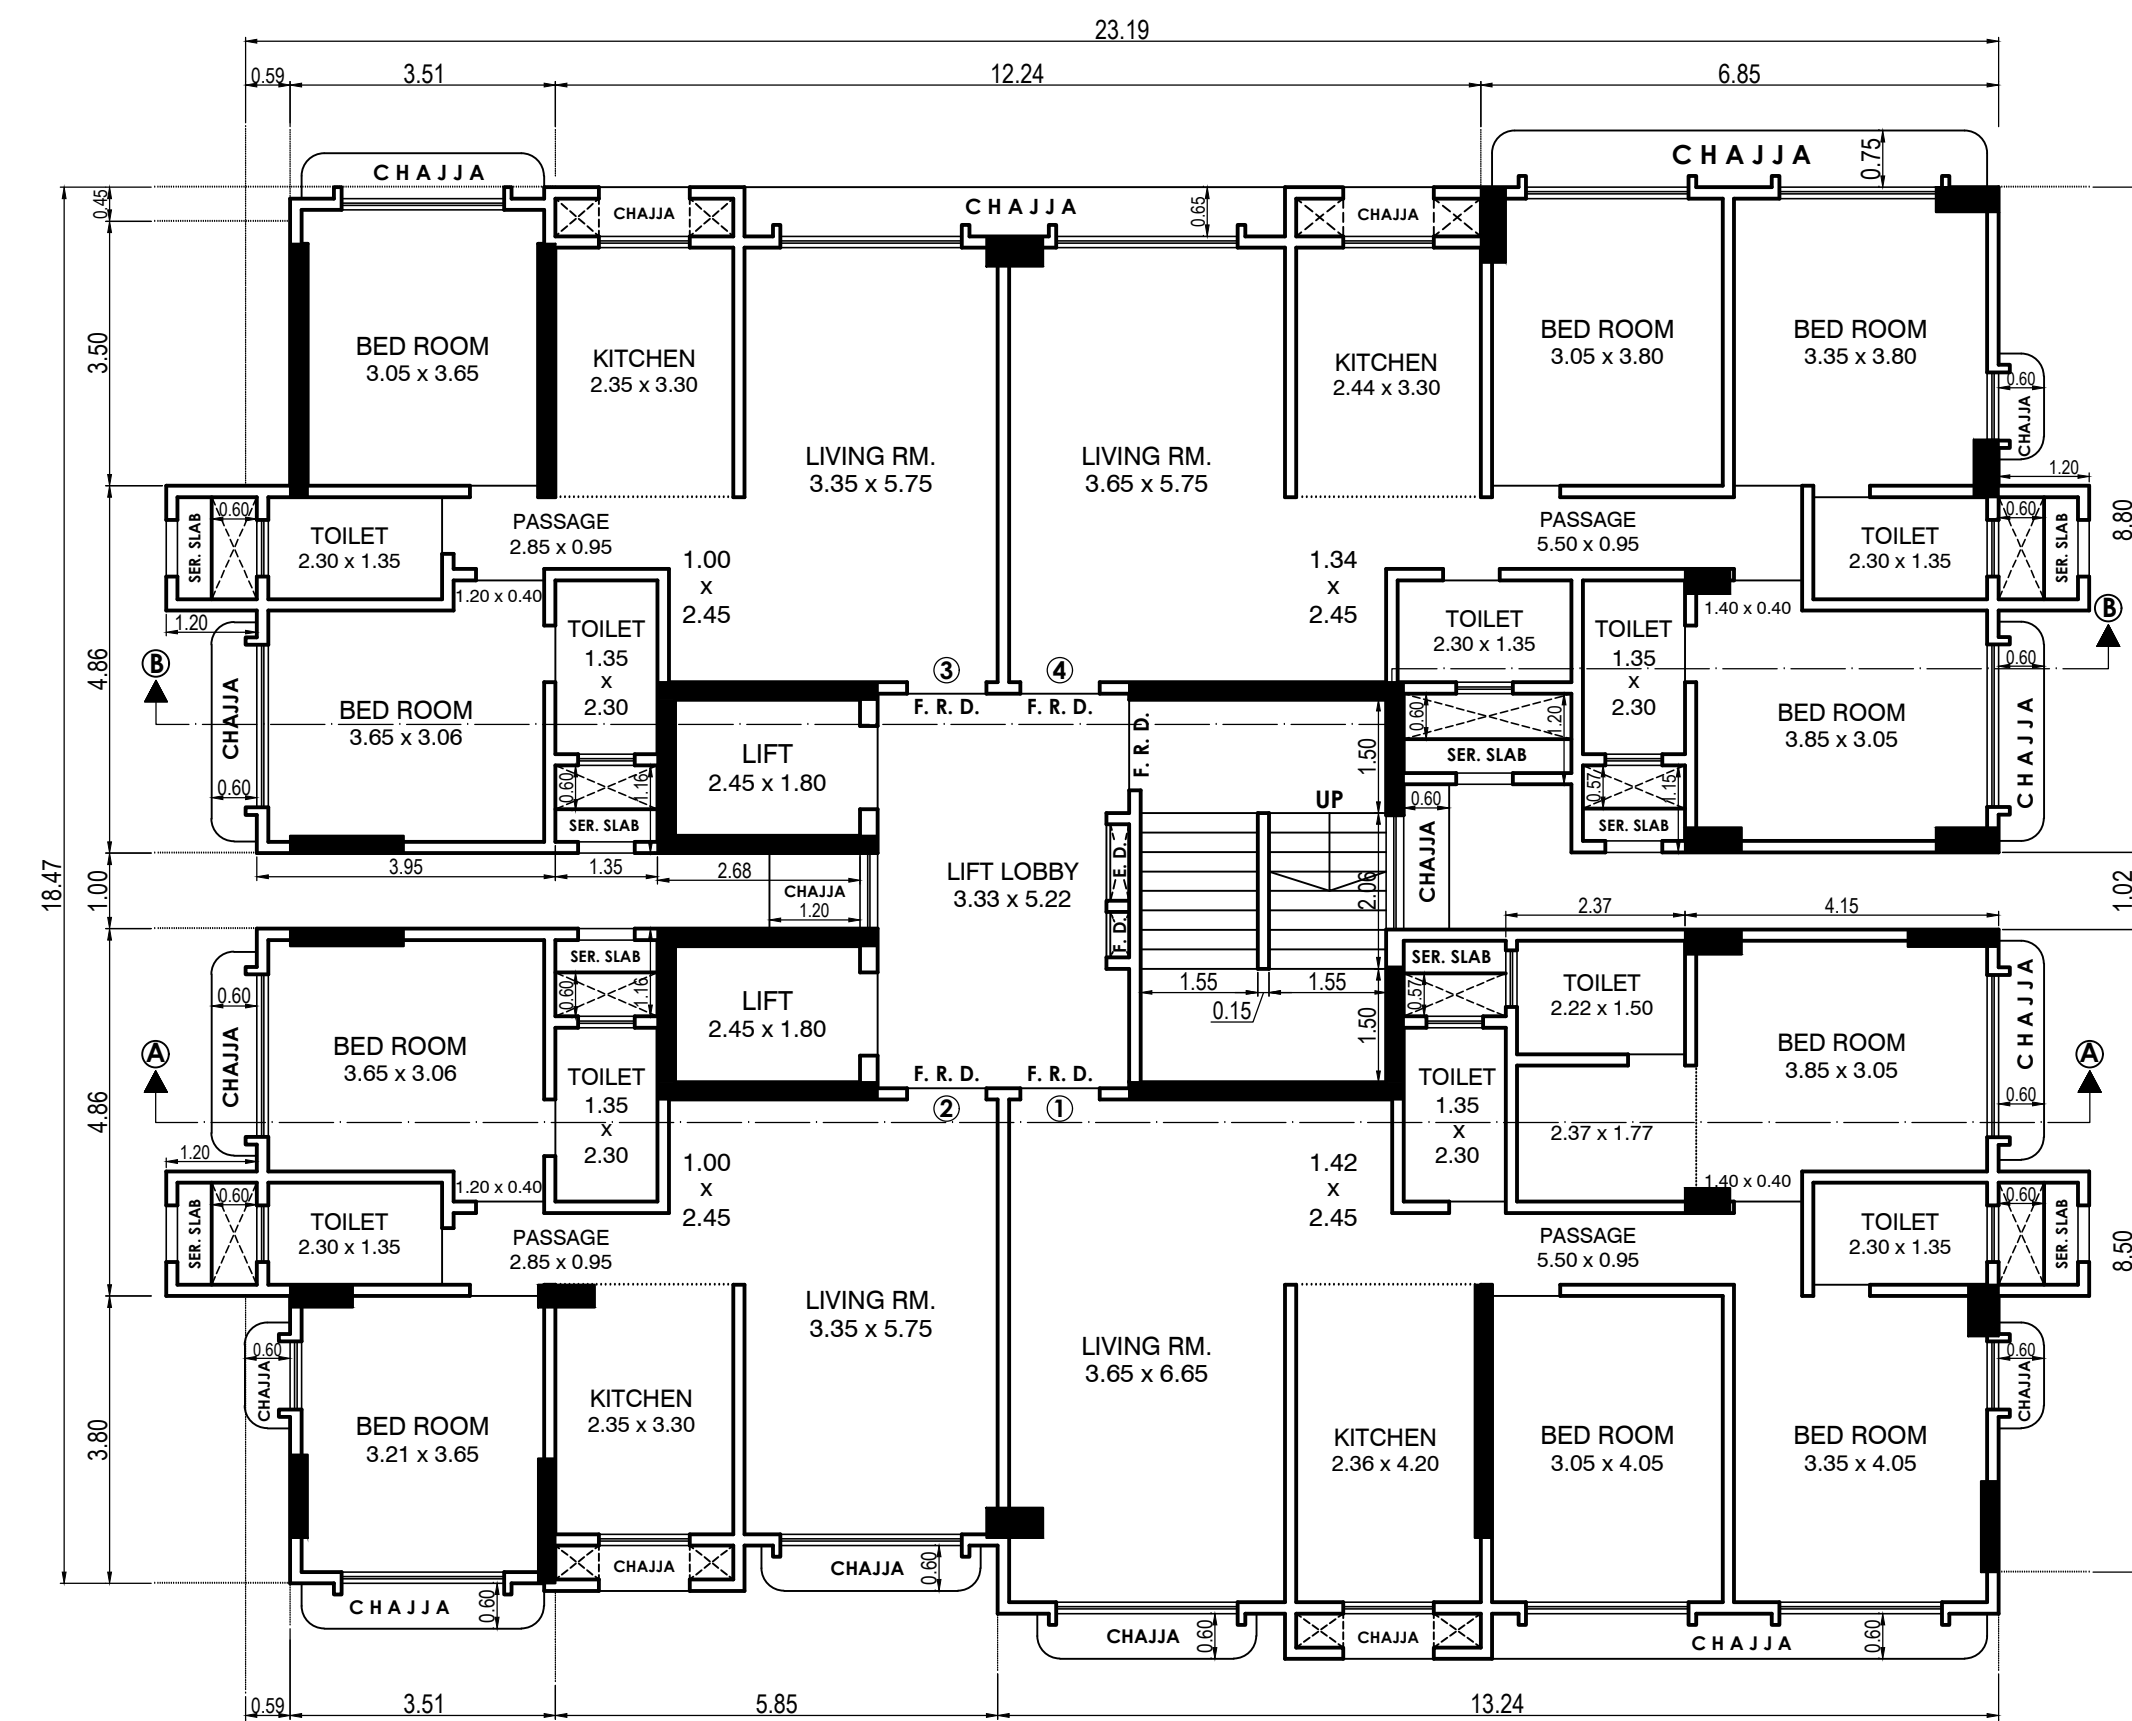


10TH TO 13TH & 15TH FLOOR PLAN
SCALE :- 1:100

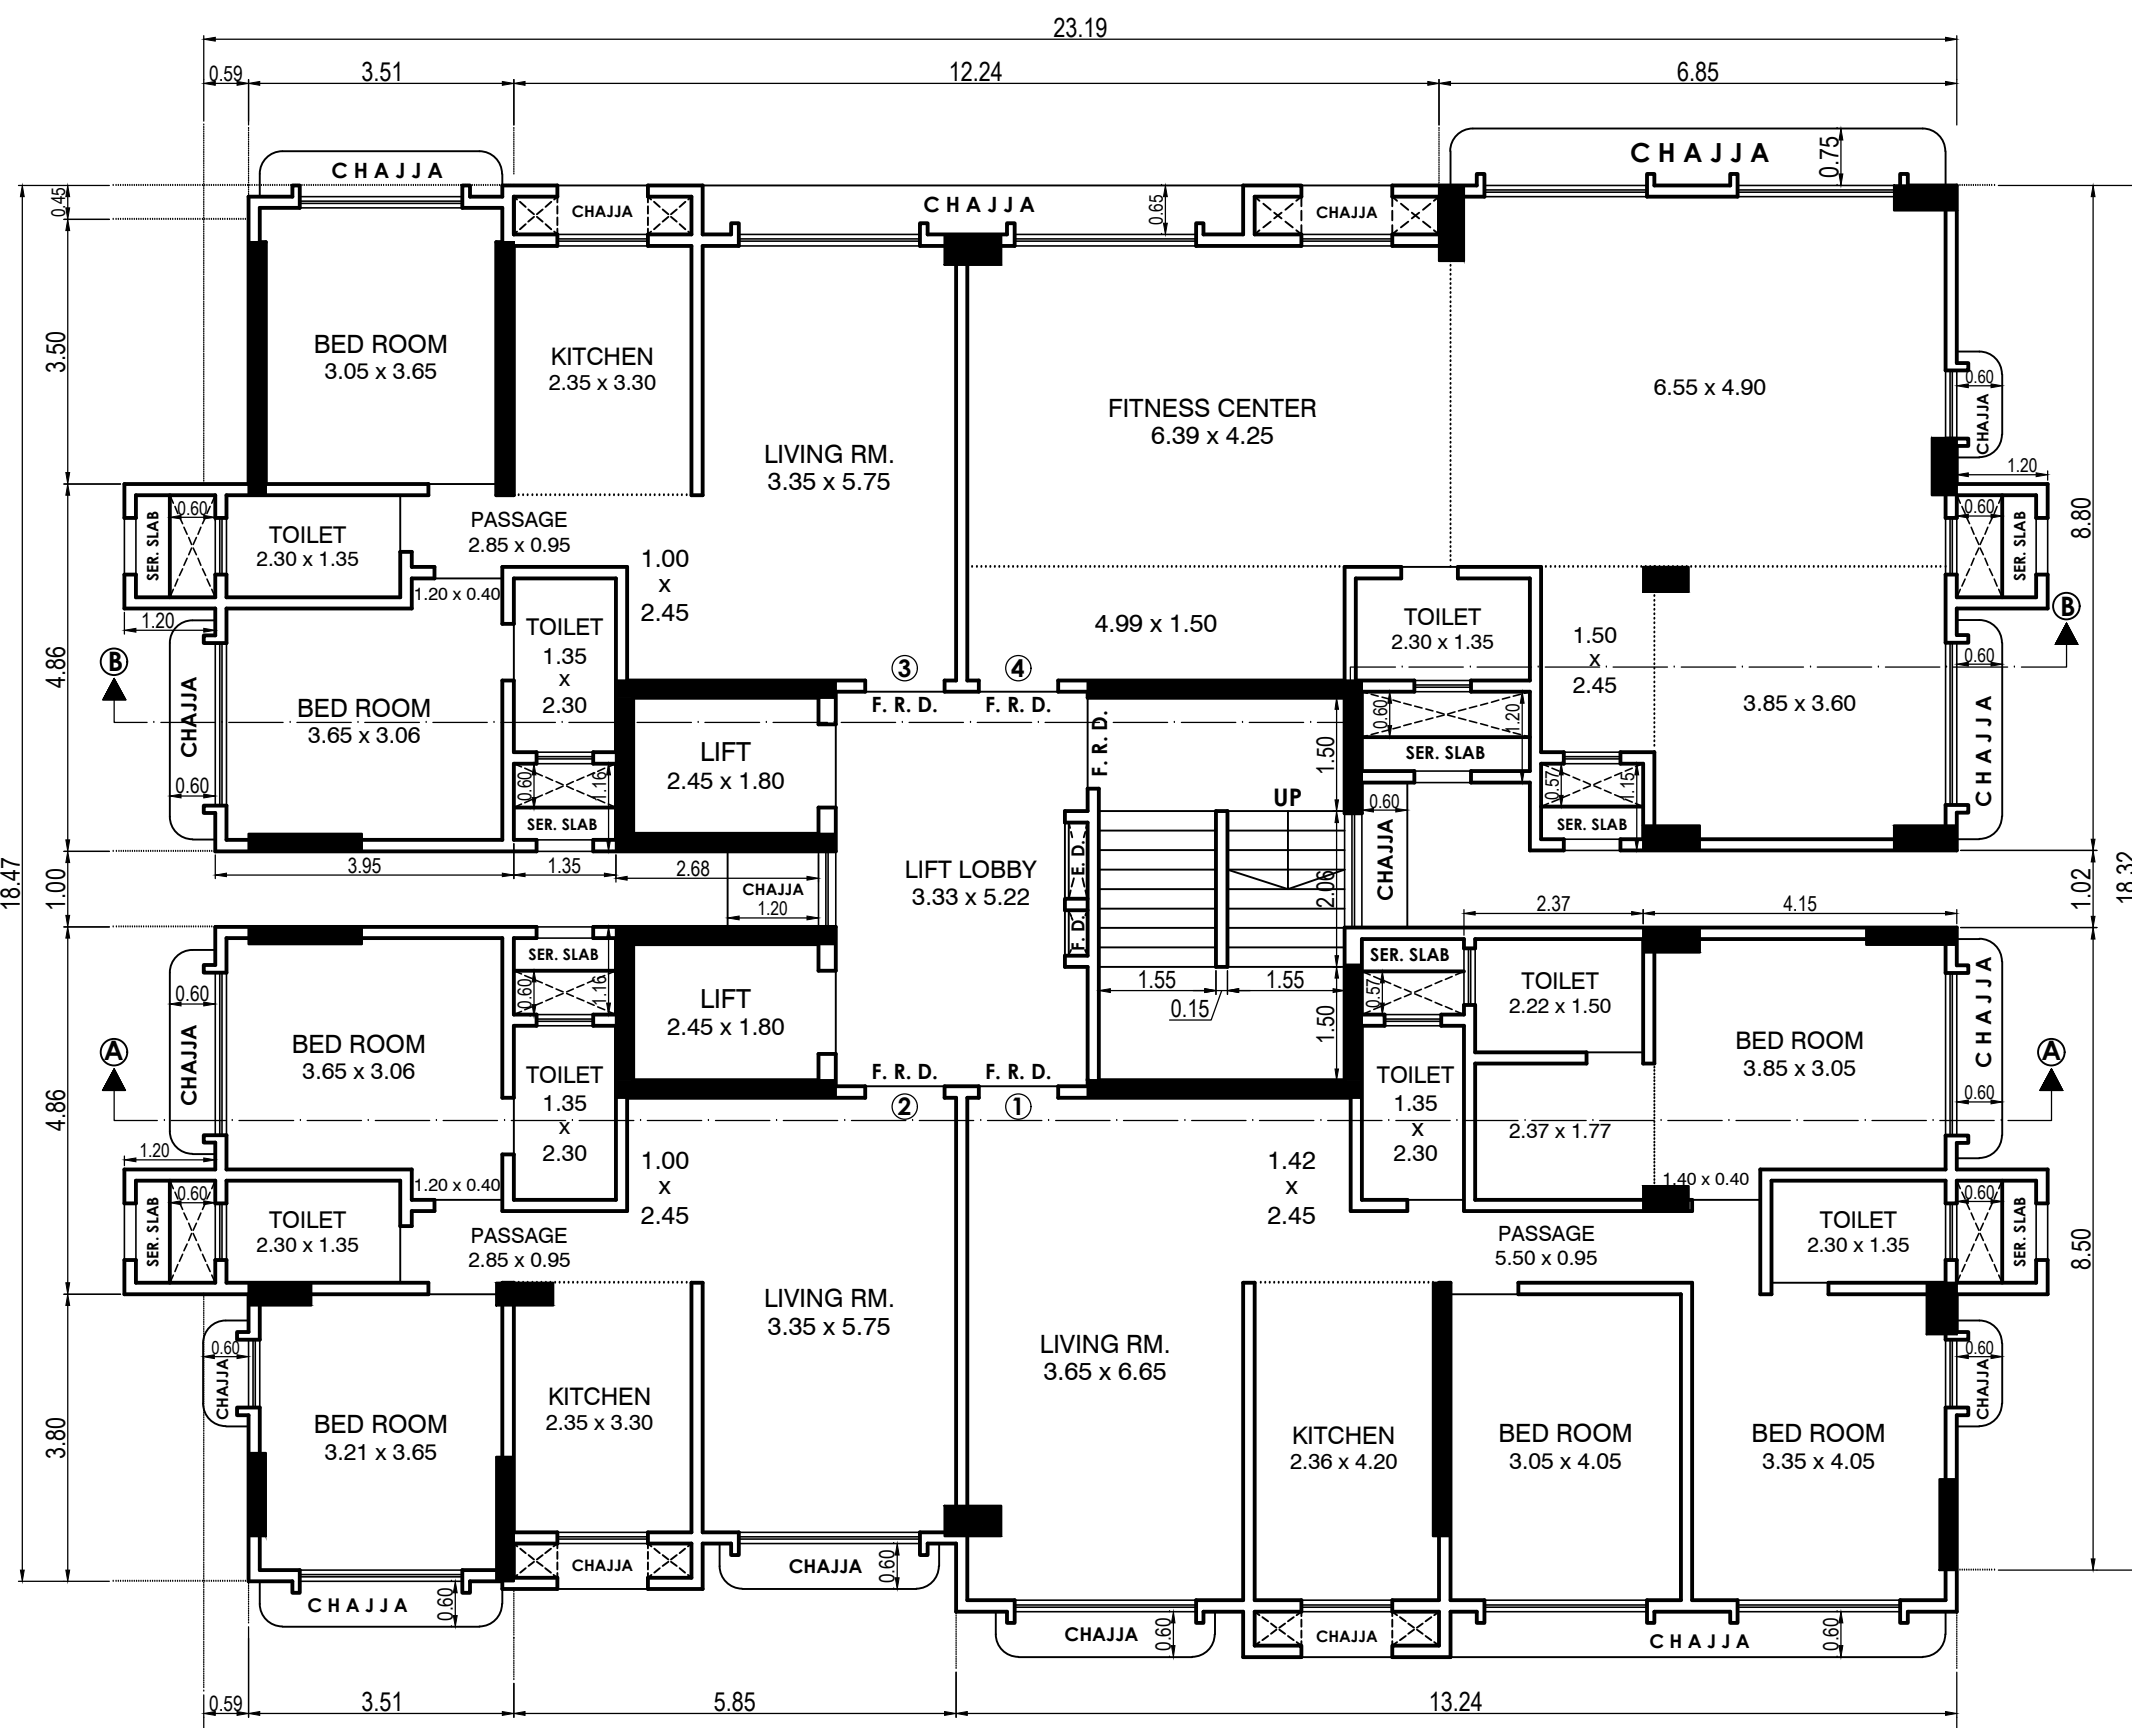

16TH FLOOR PLAN
SCALE :- 1:100

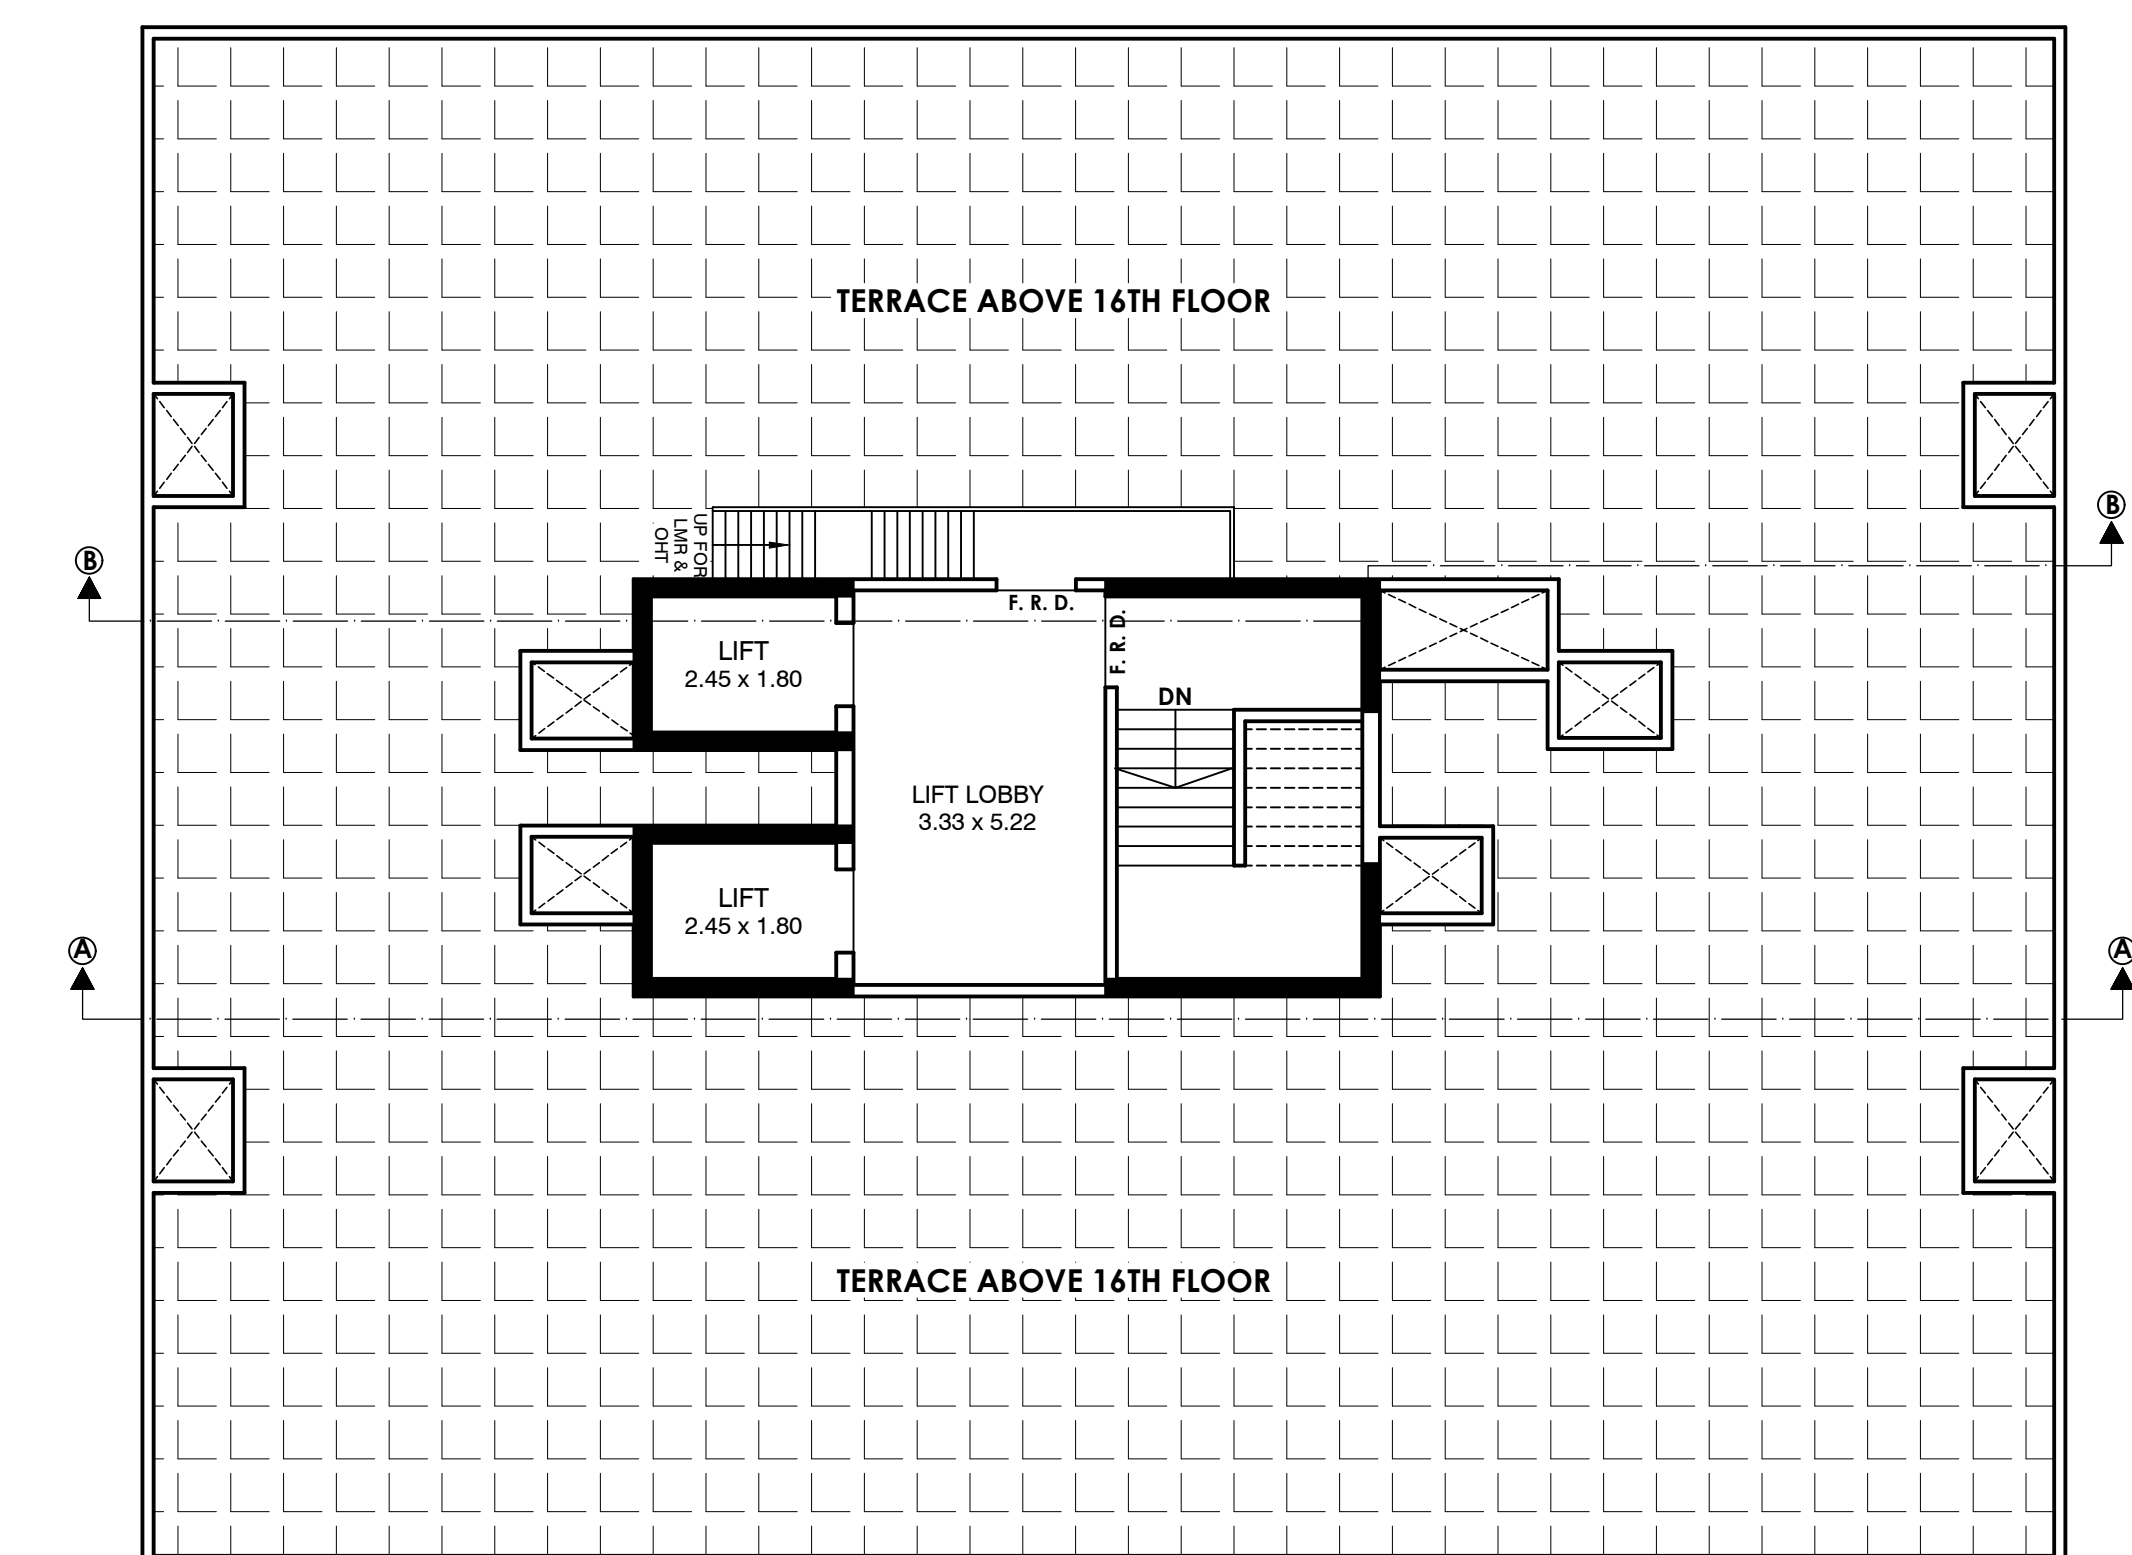


TERRACE FLOOR PLAN
SCALE :- 1:100

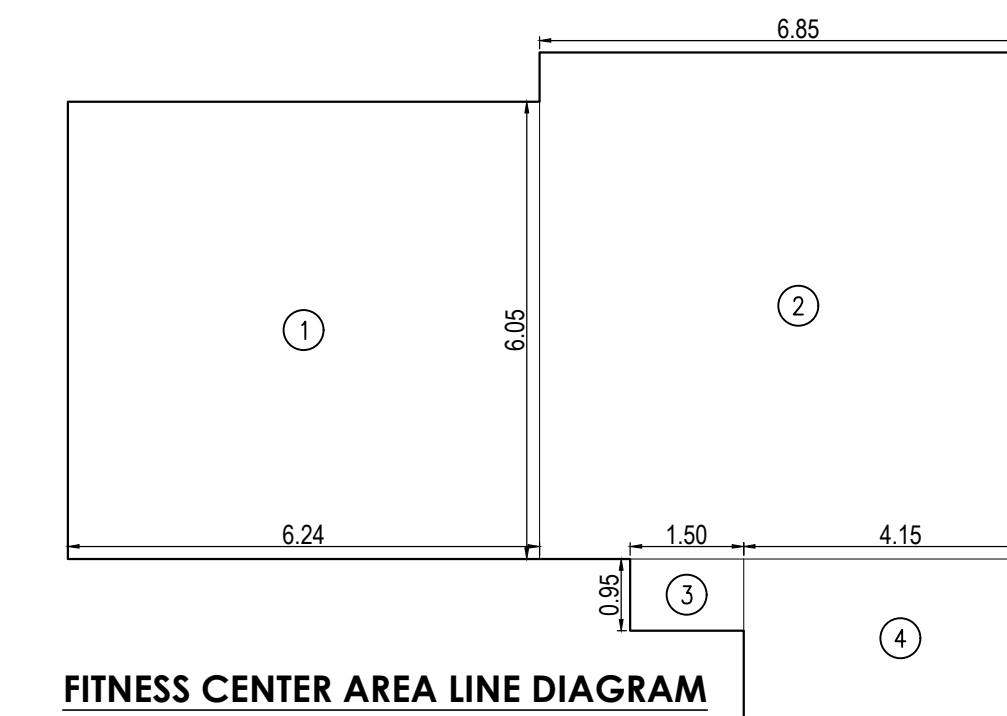

FITNESS CENTER AREA LINE DIAGRAM
(16TH FLOOR)
SCALE :- 1:100

FITNESS CENTER AREA CALCULATION					
16TH FLOOR					
1	6.24	X	6.05	X	1 NO
2	6.85	X	6.70	X	1 NO
3	1.50	X	0.95	X	1 NO
4	4.15	X	2.10	X	1 NO
TOTAL ADDITION					= 93.76 SQ.MT


REQUIRED AREA FOR FITNESS CENTER = 2% OF 4792.25 = 95.84 sq. mt.
PROPOSED AREA OF FITNESS CENTER = 93.76 sq. mt.

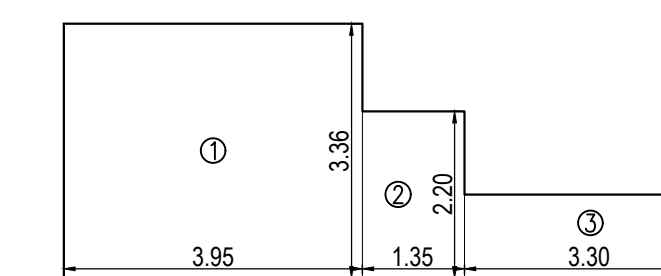

SOC. OFFICE AREA LINE DIAGRAM
(14TH FLOOR)
SCALE :- 1:100

SOC. OFFICE AREA CALCULATION					
14TH FLOOR					
1	3.95	X	3.36	X	1 NO
2	1.35	X	2.20	X	1 NO
3	3.30	X	1.10	X	1 NO
TOTAL ADDITION					= 19.87 SQ.MT

PERMISSIBLE AREA FOR SOCIETY OFFICE = 20.00 sq. mt.
PROPOSED AREA = 19.87 sq. mt.

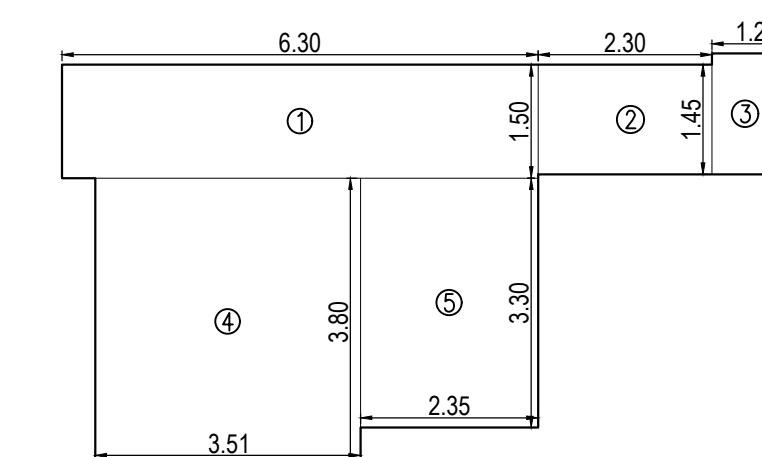

REFUGE AREA LINE DIAGRAM
(14TH FLOOR)
SCALE :- 1:100

REFUGE AREA CALCULATION					
14TH FLOOR					
1	6.30	X	1.50	X	1 NO
2	2.30	X	1.45	X	1 NO
3	1.20	X	1.60	X	1 NO
4	3.51	X	3.80	X	1 NO
5	2.35	X	3.30	X	1 NO
TOTAL ADDITION					= 35.81 SQ.MT

REFUGE AREA STATEMENT	
AT 14TH FLOOR	
14TH FLOOR AREA	= 283.44 sq. mt.
16TH FLOOR AREA	= 340.61 sq. mt.
16TH FLOOR AREA	= 246.85 sq. mt.
TOTAL AREA	= 870.90 sq. mt.
REQUIRED REFUGE AREA	= 4 X 870.90
AT 14TH FLOOR	= 34.84 SQ.MTS
PROPOSED REFUGE AREA	= 35.81 SQ.MTS
PERM. REFUGE AREA	= 37.01 SQ.MTS


PROFORMA-B CONTENT OF SHEET

7TH TO 16TH FLOOR PLAN, TERRACE FLOOR PLAN, FITNESS CENTER AREA CALCULATION, REFUGE AREA CALCULATION OF 7TH & 14TH FLOOR, SOC. OFFICE AREA CALCULATION

STAMP OF APPROVAL OF PLAN

D. F. O.

DY. C. F. O.

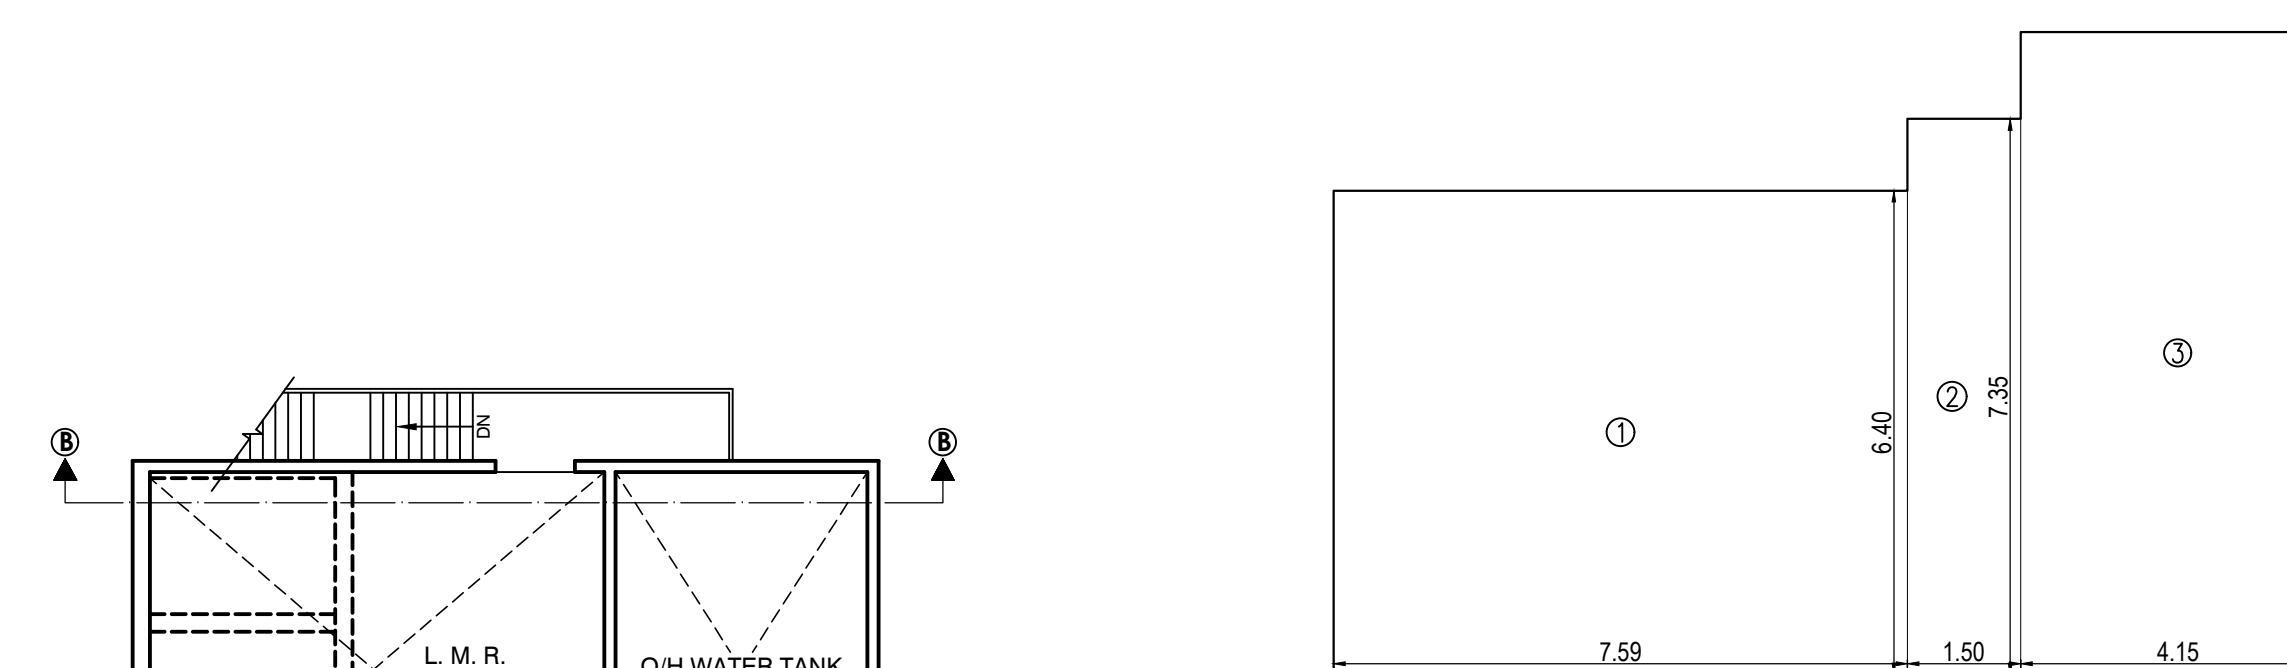


REFUGE AREA LINE DIAGRAM
(7TH FLOOR)
SCALE :- 1:100


REFUGE AREA CALCULATION					
7TH FLOOR					
1	7.59	X	6.40	X	1 NO
2	1.50	X	7.35	X	1 NO
3	4.15	X	6.50	X	1 NO
TOTAL ADDITION					= 94.89 SQ.MT

REFUGE AREA STATEMENT	
AT 7TH FLOOR	
7TH FLOOR AREA	= 283.44 sq. mt.
8TH TO 9TH FLOOR AREA	= 325.28 X 2
	= 650.56 sq. mt.
11TH TO 13TH FLOOR AREA	= 340.61 X 4
	= 1362.44 sq. mt.
TOTAL AREA	= 2296.40 sq. mt.
REQUIRED REFUGE AREA	= 1 X 2296.40
AT 7TH FLOOR	= 66.10 SQ.MTS
PROPOSED REFUGE AREA	= 94.89 SQ.MTS
PERM. REFUGE AREA	= 96.73 SQ.MTS

DESCRIPTION OF PROPOSAL					
PROPOSED DEVELOPMENT ON PLOT BEARING C. T. S. NO. 1386 OF MULLUND (W). AT JUNCTION OF J. N. ROAD & WALJI LADHA ROAD, MUMBAI.					
NAME OF OWNER			SIGNATURE		
MULUND HANSA VILLA CO. OP. HSG. LTD.			MANISH HAWATIL HAWATIL		
JOB No.	DRG. No.	DATE	DRN. BY	CHK. BY	REVISION
	3/4		SHASHI	ASHISH	
NAME SIGN & ADD. OF L. S.					
ASHISH BHATT 802, 8TH FLOOR, VIKAS CENTRE, JUNCTION OF N. S. B. ROAD & S. I. ROAD, MULLUND (WEST) MUMBAI - 400080.					

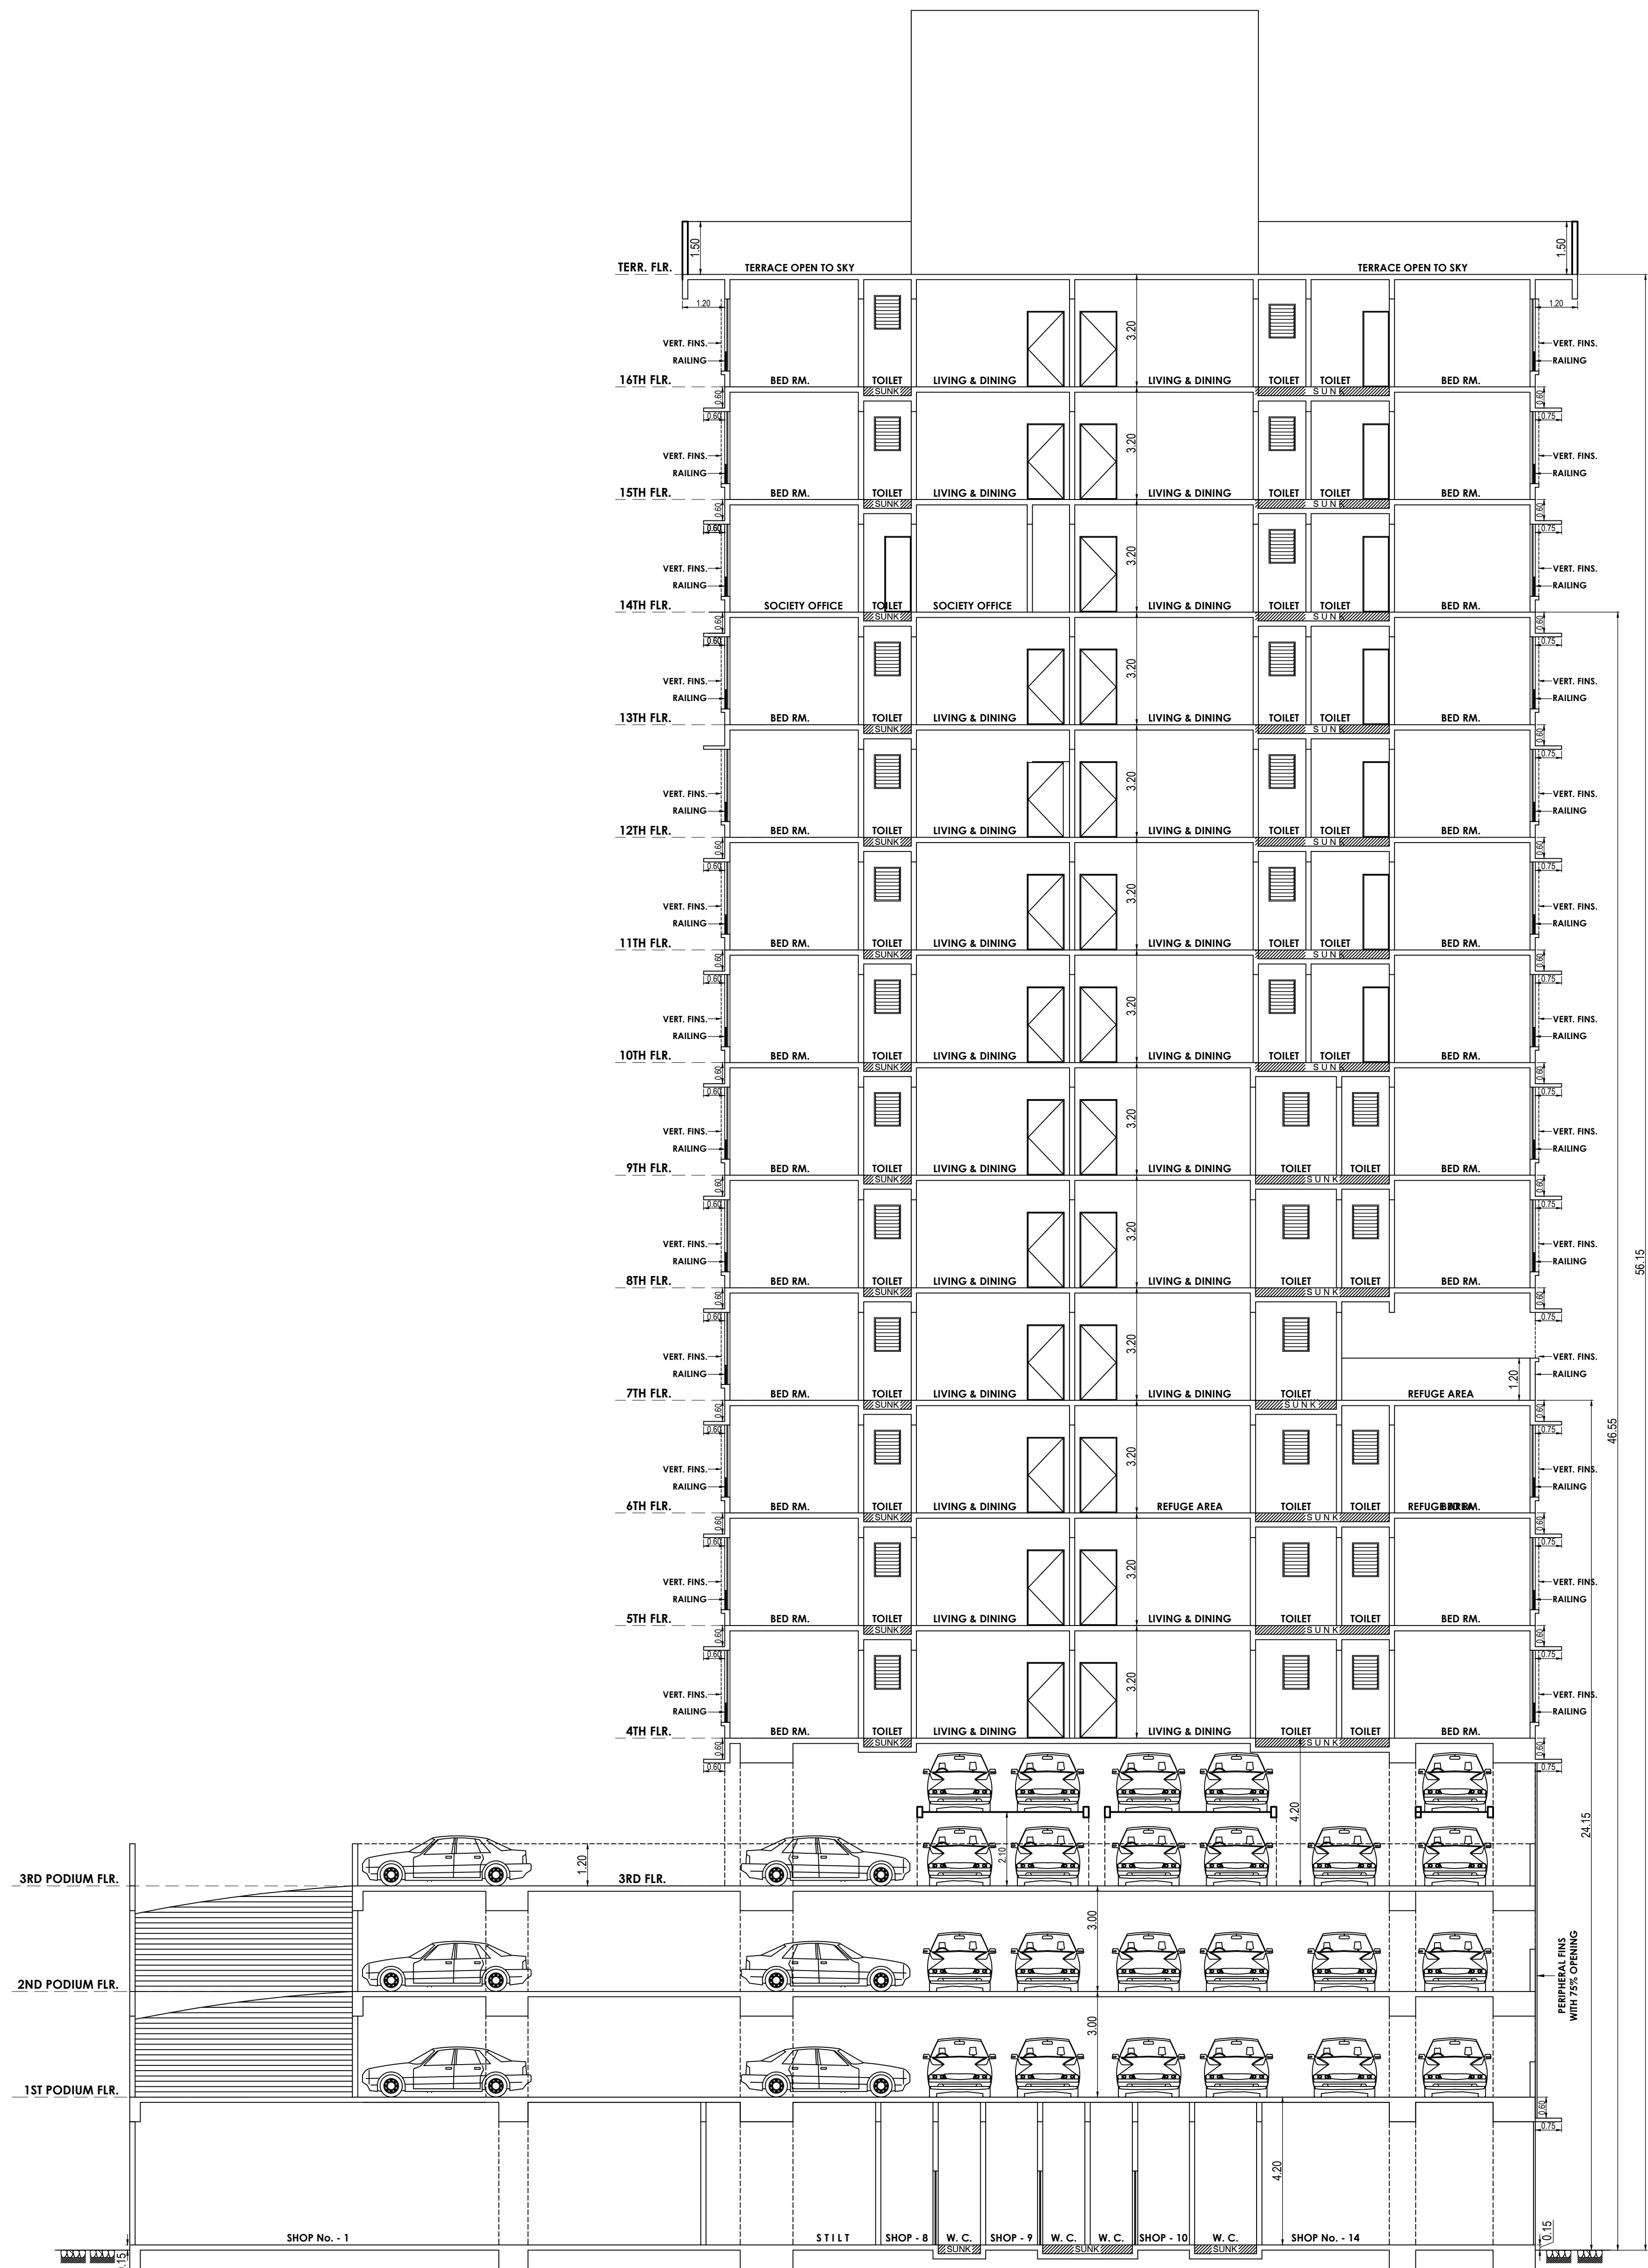

SECTION A - A
SCALE :- 1:100

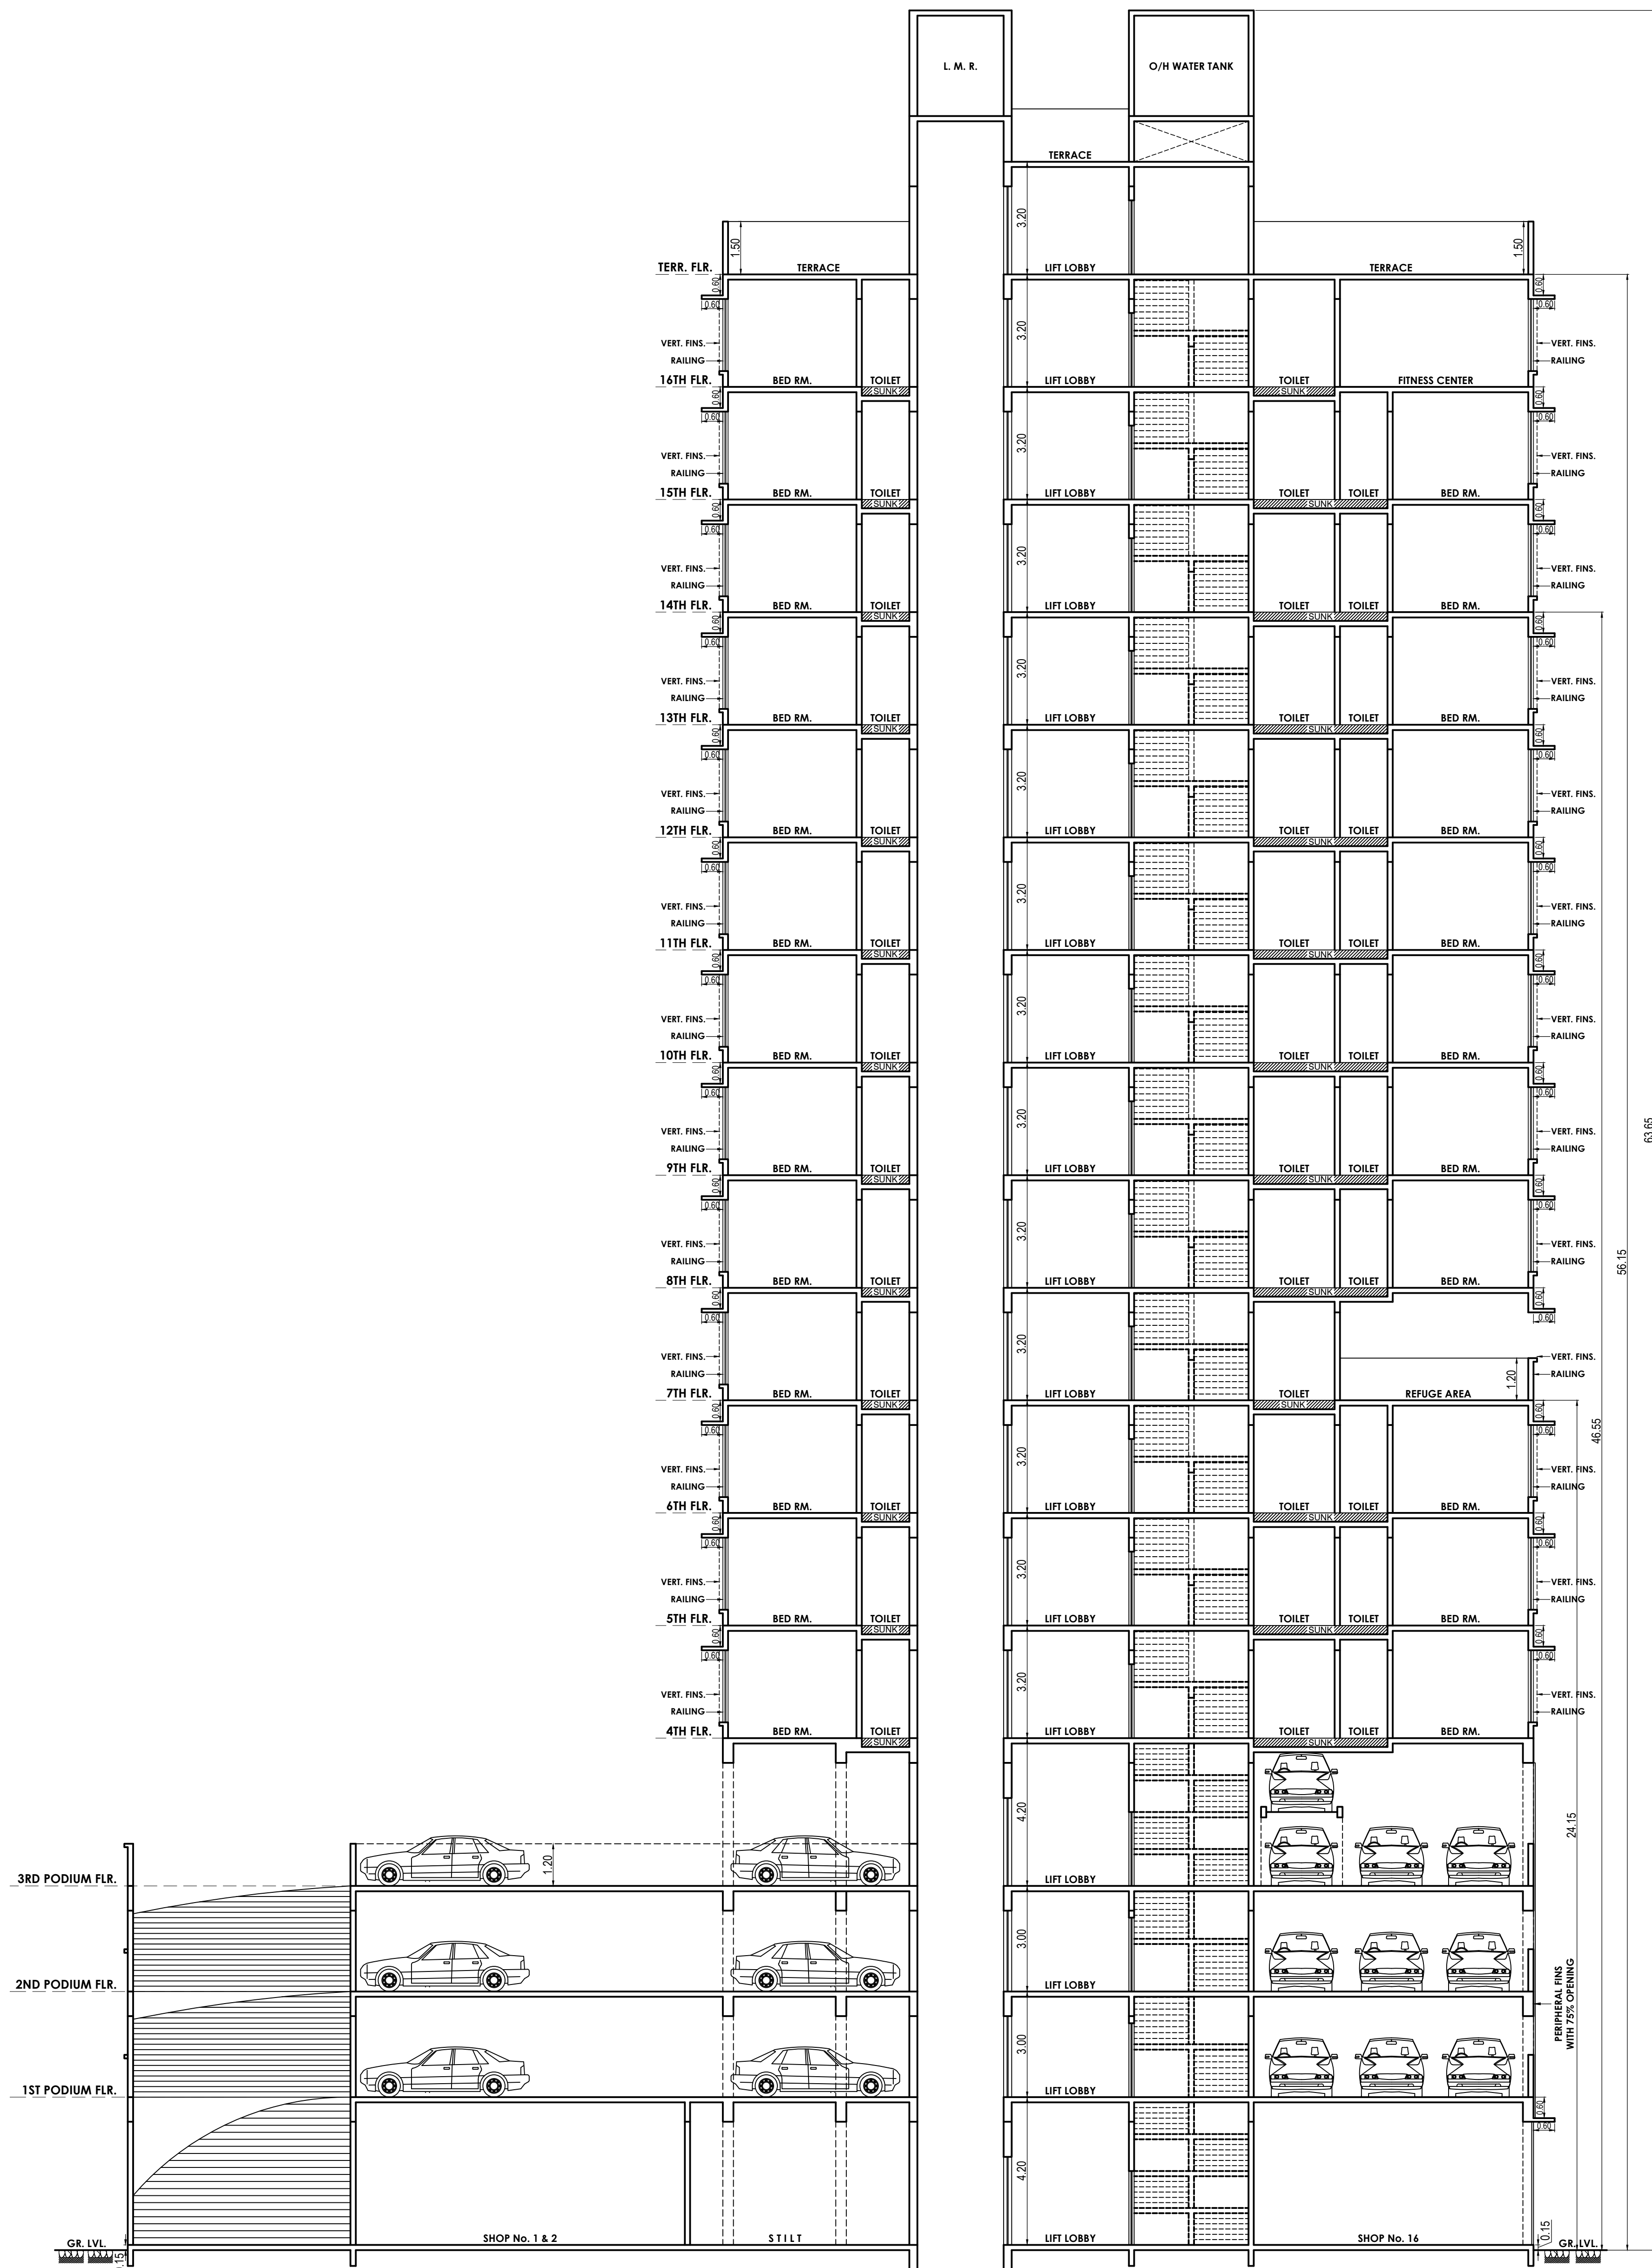

SECTION B - B
SCALE :- 1:100

PROFORMA-B					
CONTENT OF SHEET					
SECTION A - A & B - B					
STAMP OF APPROVAL OF PLAN					
D. F. O.					
DY. C. F. O.					
DESCRIPTION OF PROPOSAL					
PROPOSED DEVELOPMENT ON PLOT BEARING C. T. S. NO. 1386 OF MULUND (W), AT JUNCTION OF J. N. ROAD & WALJI LADHA ROAD, MUMBAI.					
NAME OF OWNER			SIGNATURE		
MULUND HANSA VILLA CO.OP. HSG LTD.			MANISH HIRANJAL HALARI		
JOB No.	DRG. No.	DATE	DRN. BY	CHK. BY	REVISION
	4/4		SHASHI	ASHISH	
NAME SIGN. & ADD. OF L. S.			SIGNATURE		
ASHISH BHATT 852, 8TH FLOOR, VIKAS CENTRE, JUNCTION OF N. S. B. ROAD & S. L. ROAD, MULUND (WEST) MUMBAI - 400060.			Ashish Narendra Bhatt		